


Согласовано

Взам. инв. №
Подп. и дата
Инв. № подл.

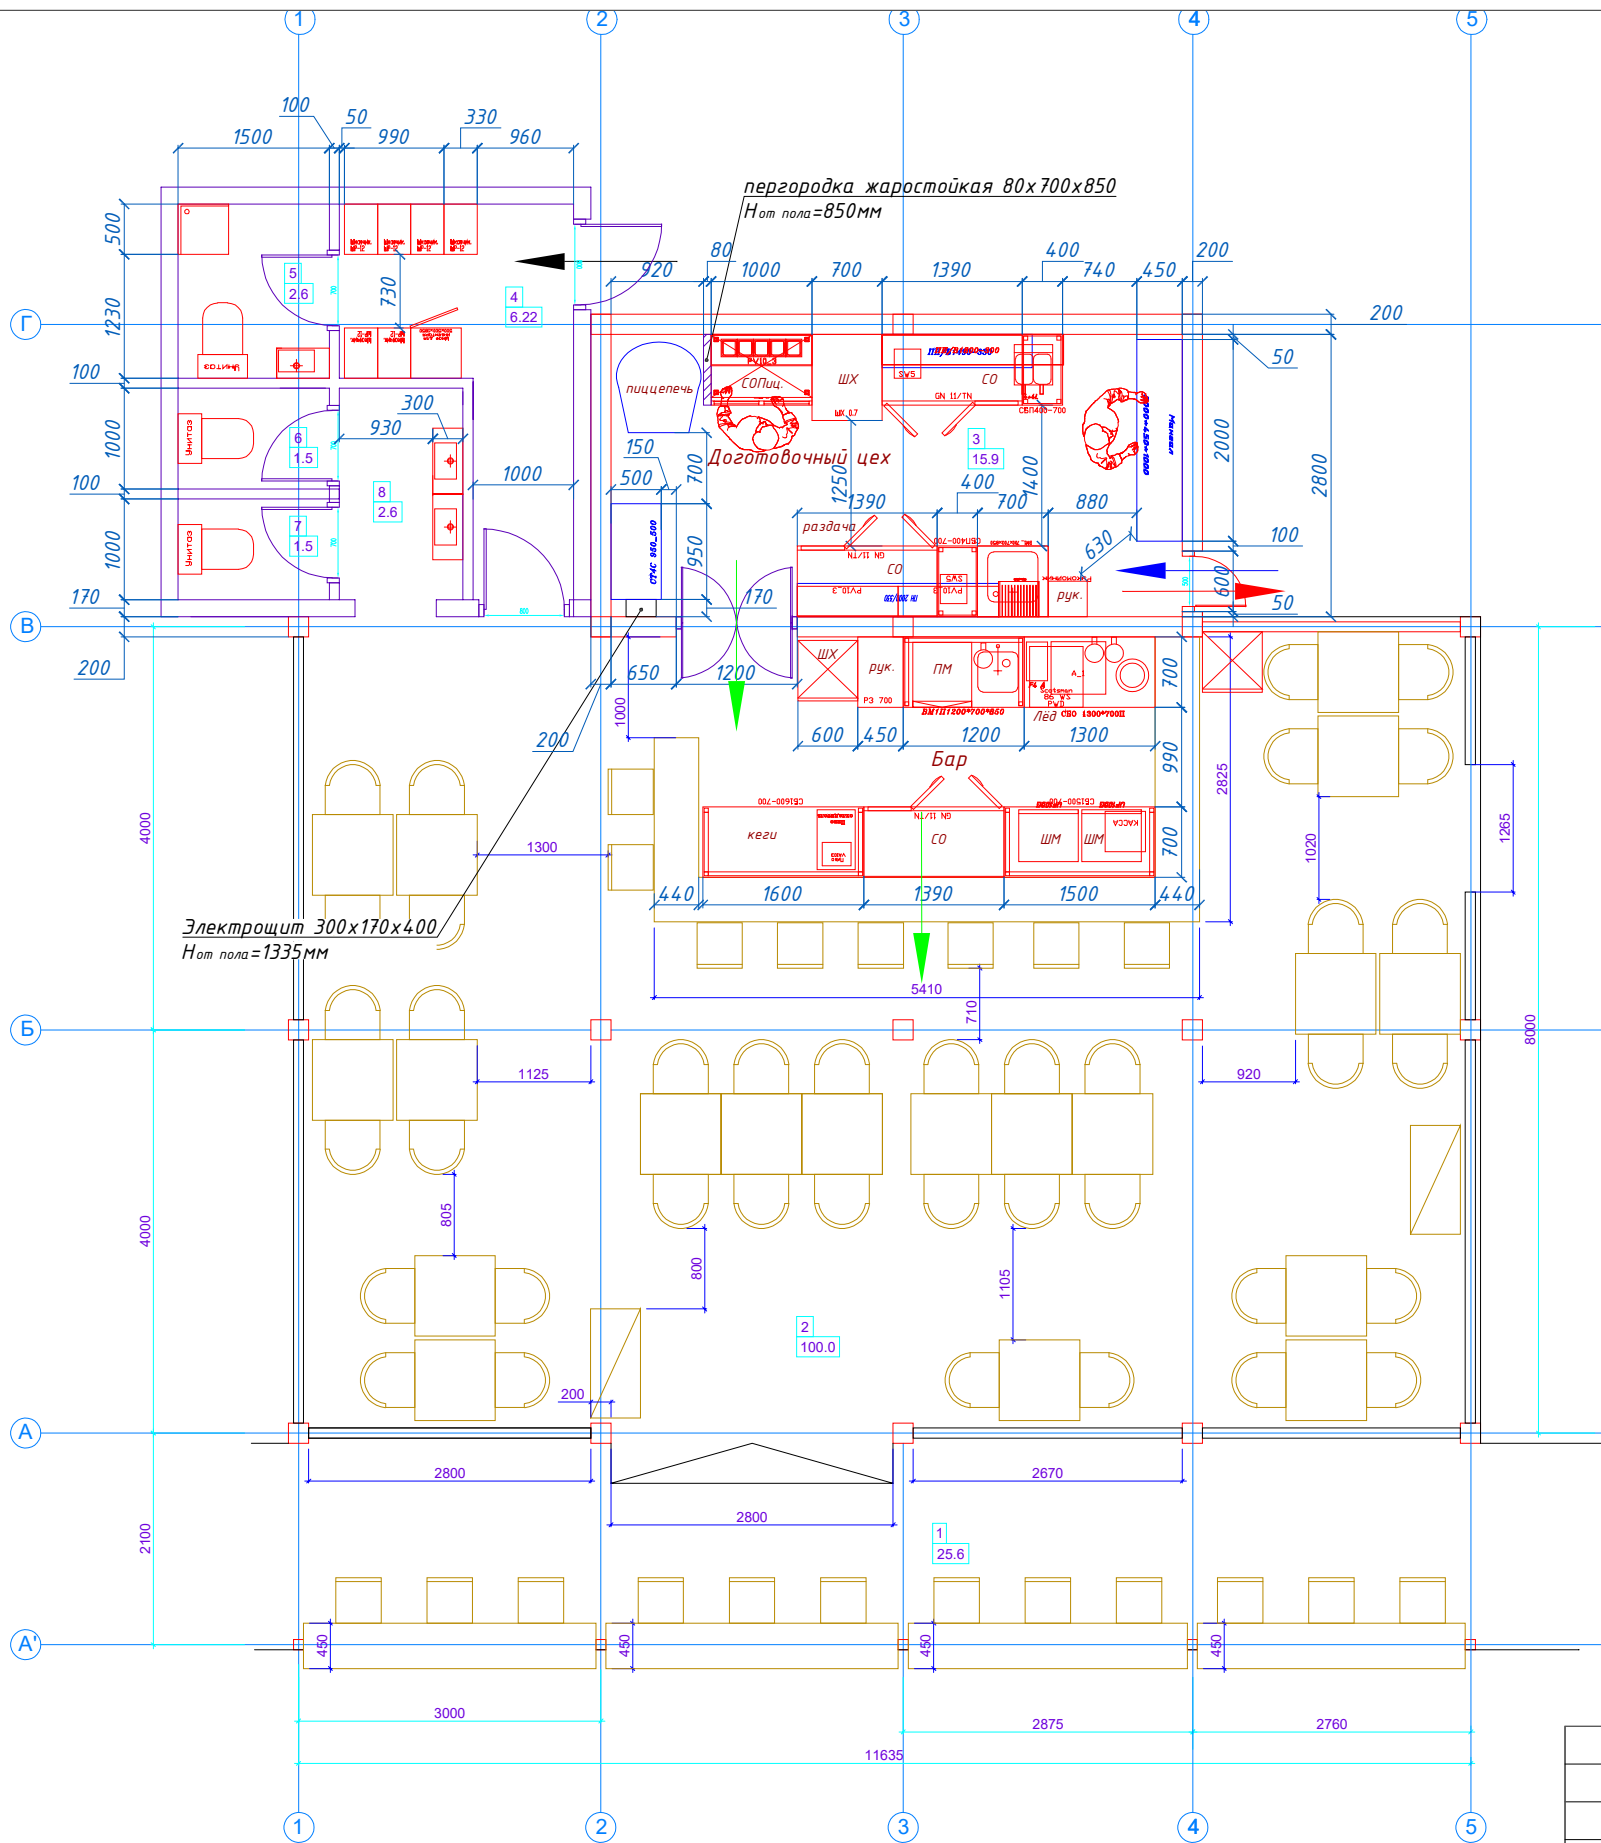

ЭКСПЛИКАЦИЯ ПОМЕЩЕНИЙ:

№	Помещение	Площадь
1	Терраса	25.6
2	Веранда	100.0
3	Догоготовочный цех	15.9
4	Гардероб персонала, КУИ	6.22
5	Сан. узел персонала	2.6
6	Сан. узел посетителей	1.5
7	Сан. узел посетителей	1.5
8	Умывальная	2.6
Общая площадь помещений:		155.92

Схема движения потоков

	Полуфабрикаты
	Готовые блюда
	Сотрудники
	Отходы

Масштаб 1:75

						1001.ТХ		
						Сколково, ЗАО Можайский район, Инновационный центр Сколково, ул. Луговая, вл.4		
Изм.	Кол.уч.	Лист	док.	Подпись	Дата	Летняя веранда Кафе "Дым" на 46 пос. мест	Стадия	Лист
Рук.пр-та.					21.04.2021		П	9
Технолог					21.04.2021	План расстановки технологического оборудования План на отметке +0.000		
Заказчик								

Согласовано

Инв. № подл. Подп. и дата Взам. инв. №

Масштаб 1:40

4000

Догоготовочный цех

Бар


						1001.ТХ			
						Сколково, ЗАО Можайский район, Инновационный центр Сколково, ул. Луговая, вл.4			
						Летняя веранда Кафе "Дым" на 46 пос. мест			
						План расстановки технологического оборудования План на отметке +0.000			
Изм.	Кол.уч.	Лист	док.	Подпись	Дата	Стадия	Лист	Листов	
Рук.пр-та.		Сапарский			21.04.2021	П		9	
Технолог		Савочкин			21.04.2021				
Заказчик									

Согласовано

Взам. инв. №

Подп. и дата

Инв. № подл.

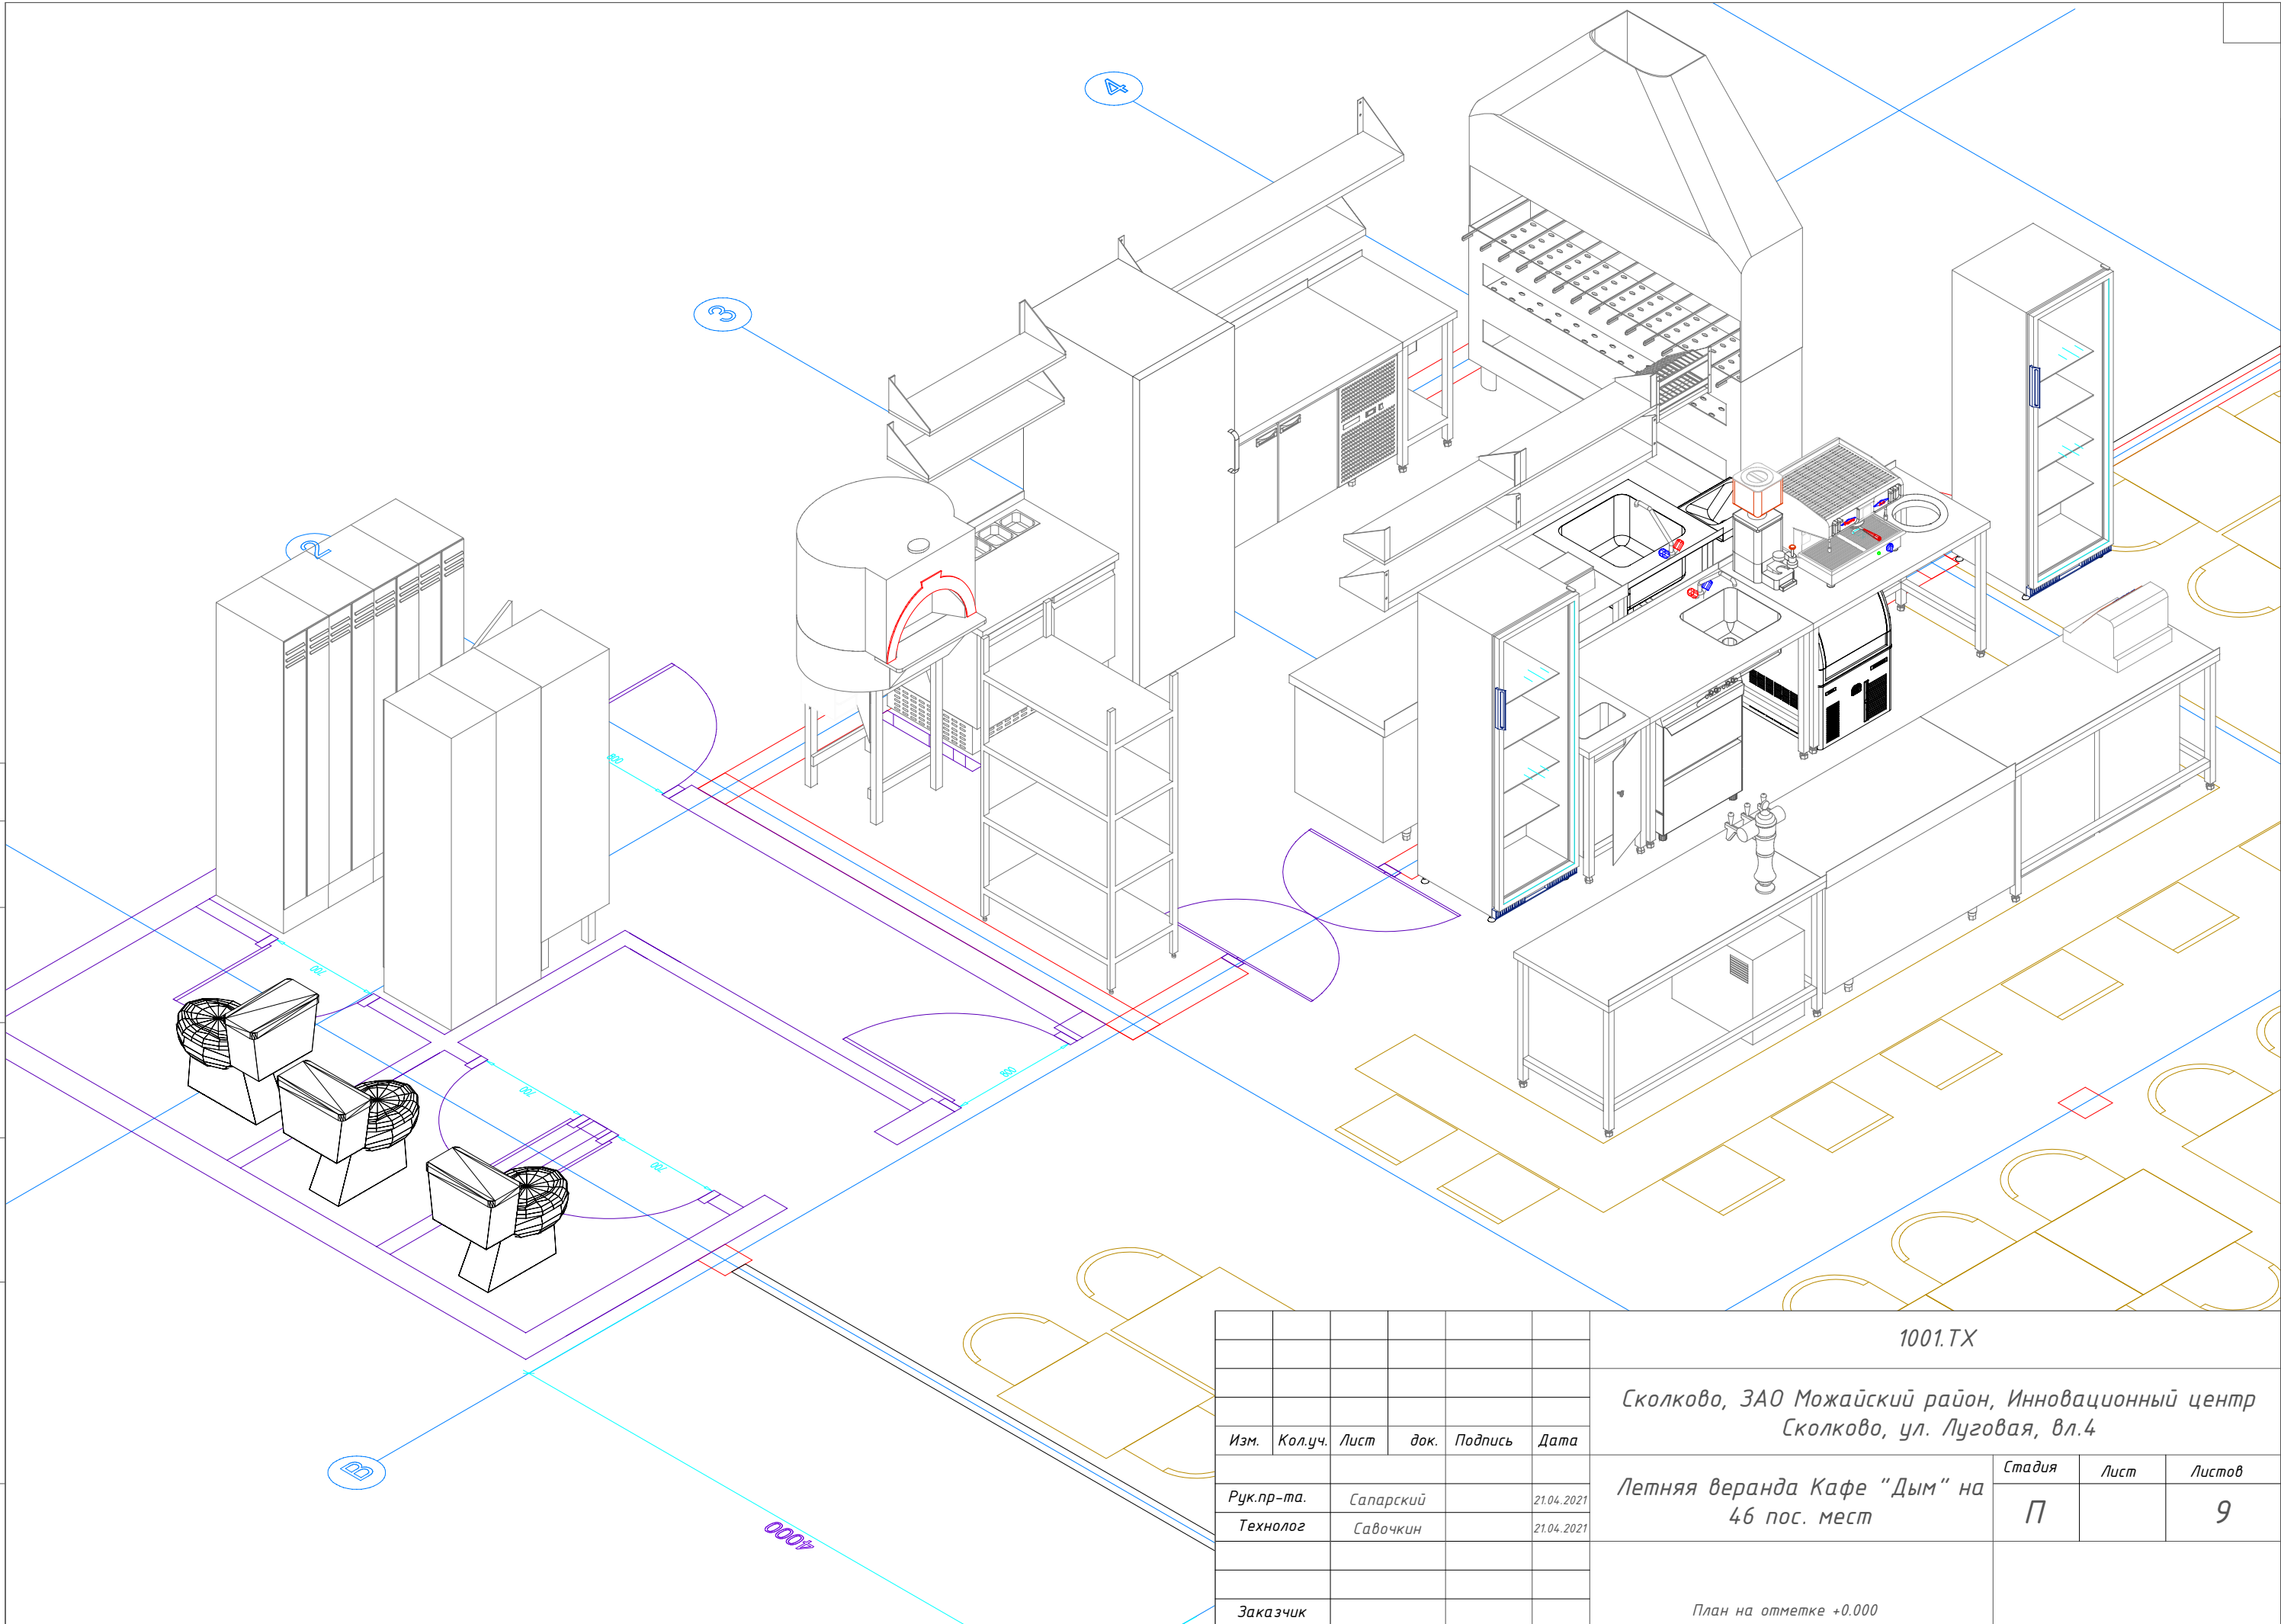

Изм.	Кол.уч.	Лист	док.	Подпись	Дата
Рук.пр-та.		Сапарский			21.04.2021
Технолог		Савочкин			21.04.2021
Заказчик					


1001.TX			
Сколково, ЗАО Можайский район, Инновационный центр Сколково, ул. Луговая, вл.4			
Летняя веранда Кафе "Дым" на 46 пос. мест		Стадия	Лист
		П	9
План на отметке +0.000			

Согласовано

Взам. инв. №

Подп. и дата

Инв. № подл.

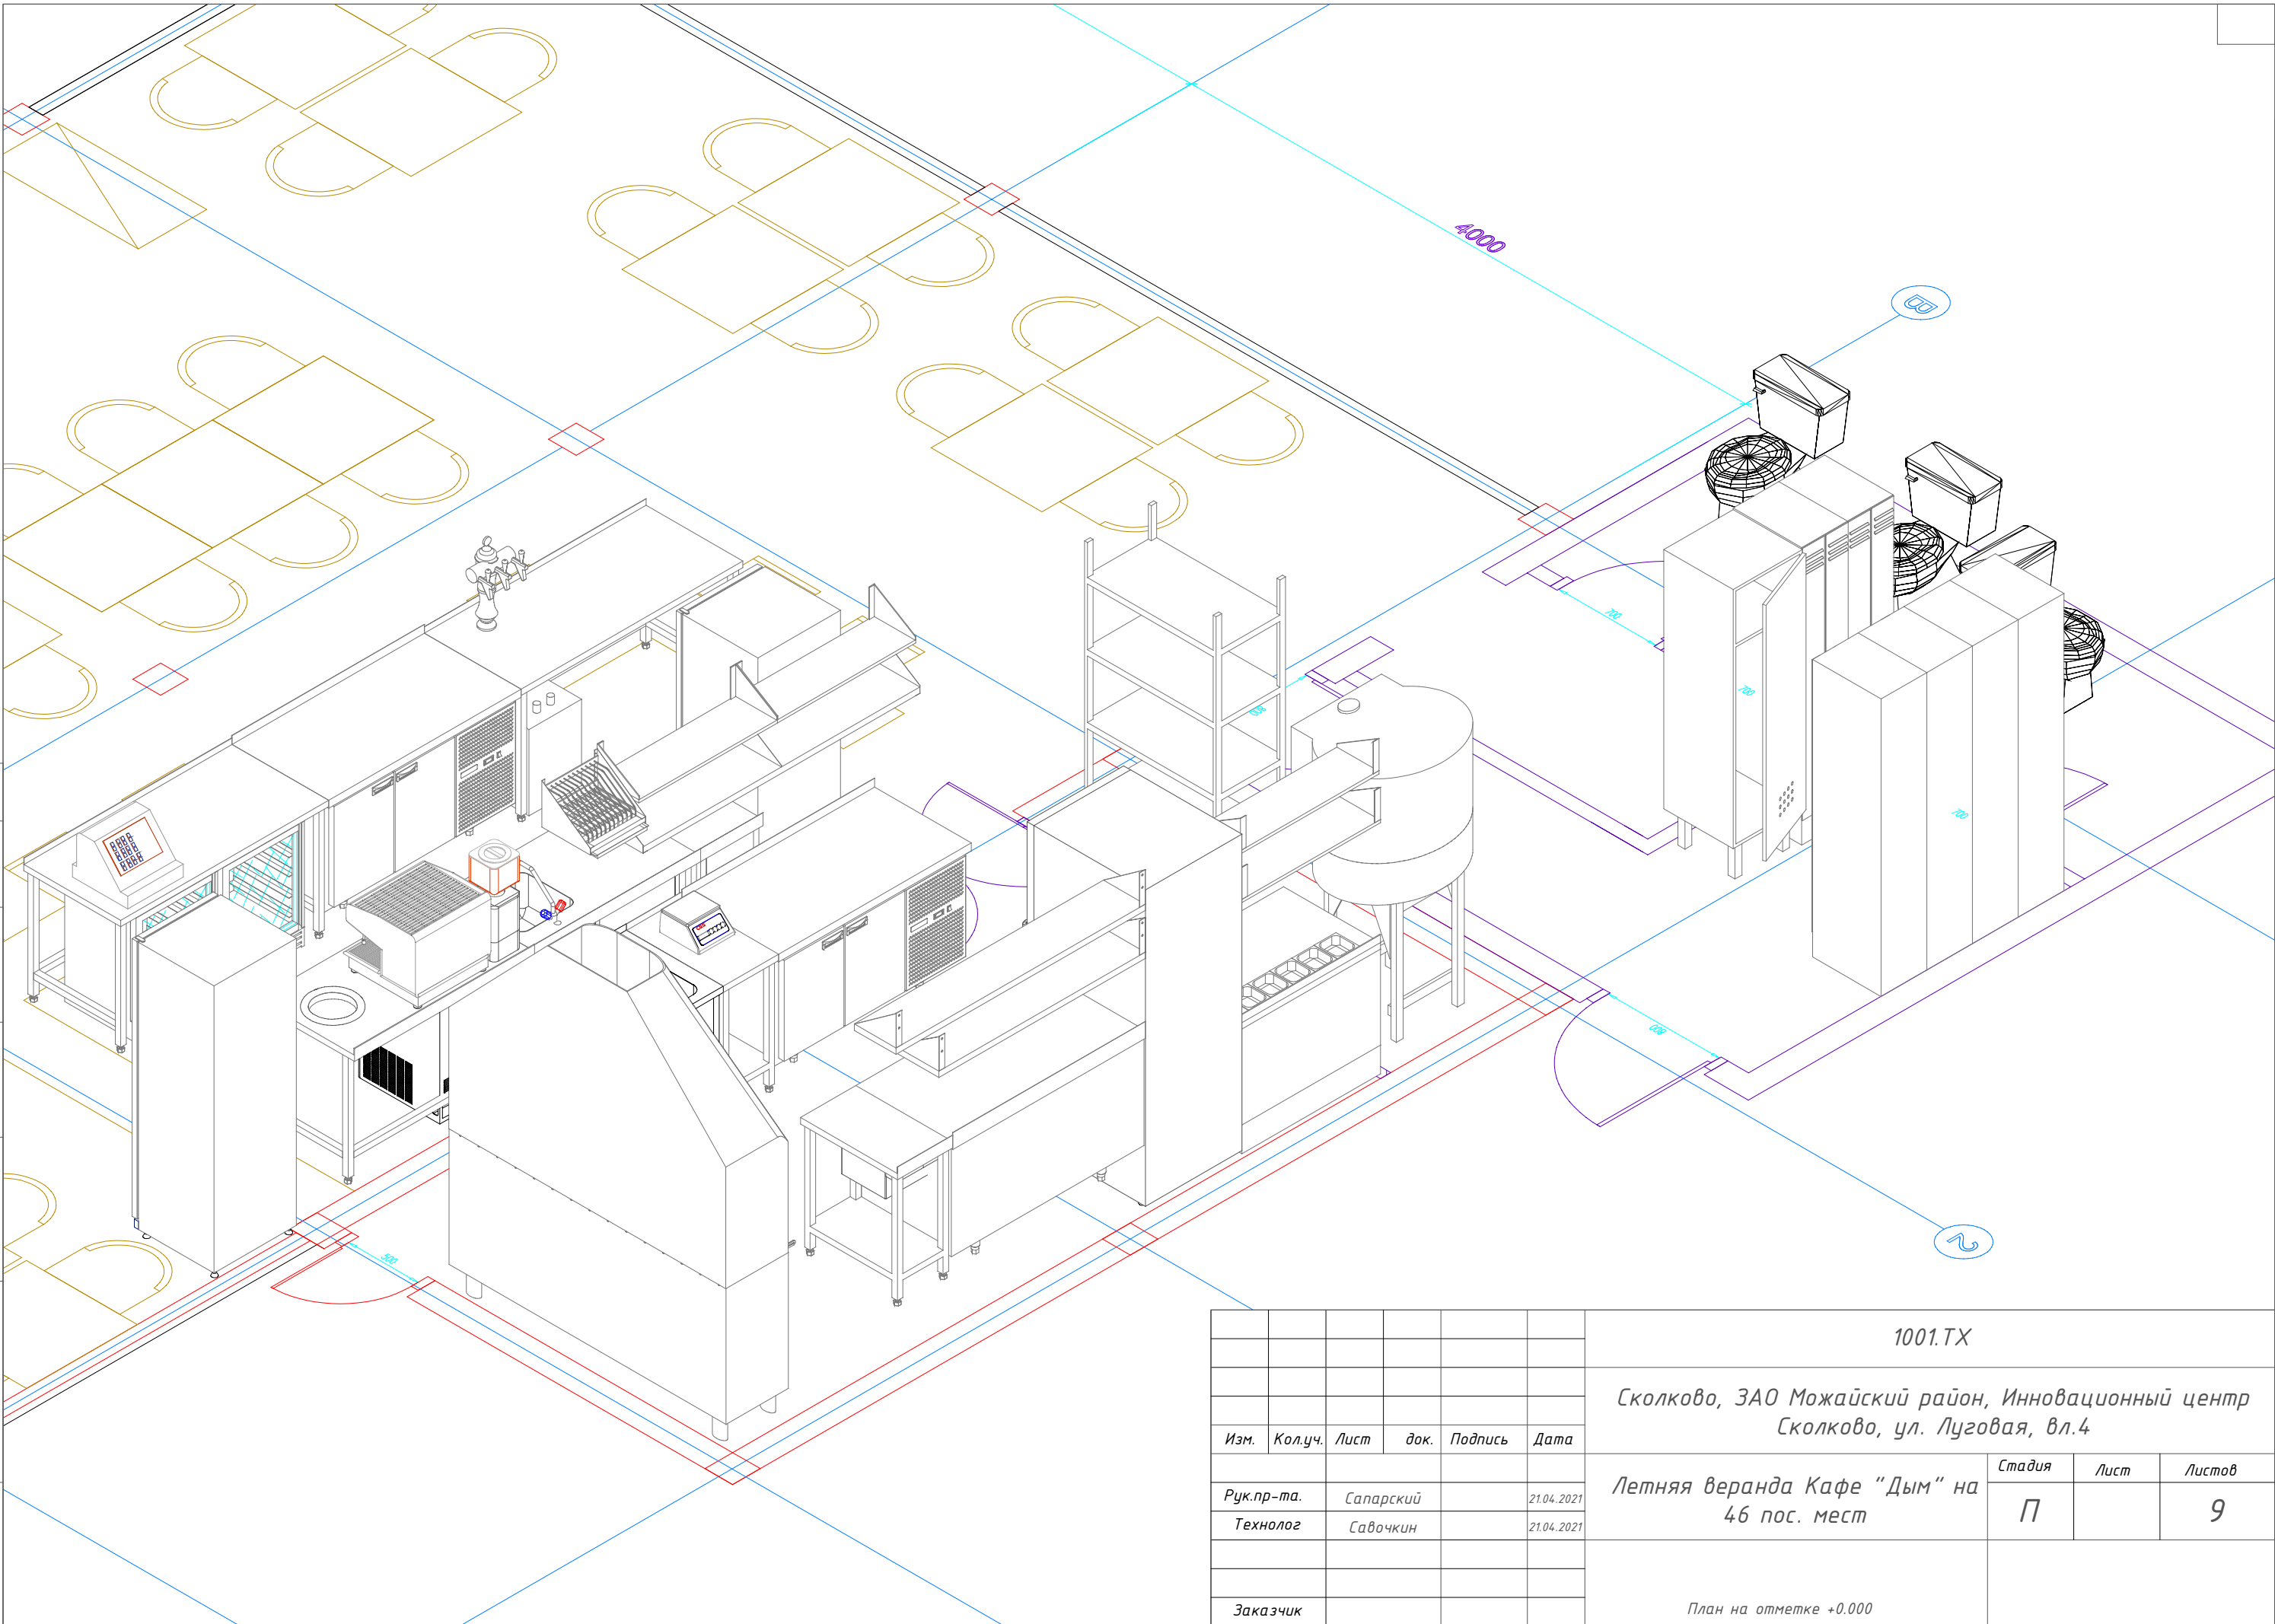


						1001.TX			
						Сколково, ЗАО Можайский район, Инновационный центр Сколково, ул. Луговая, вл.4			
Изм.	Кол.уч.	Лист	док.	Подпись	Дата	Летняя веранда Кафе "Дым" на 46 пос. мест	Стадия П	Лист	Листов 9
Рук.пр-та.		Сапарский			21.04.2021	План на отметке +0.000			
Технолог		Савочкин			21.04.2021				
Заказчик									

Согласовано

Взам. инв. №

Подп. и дата

Инв. № подл.

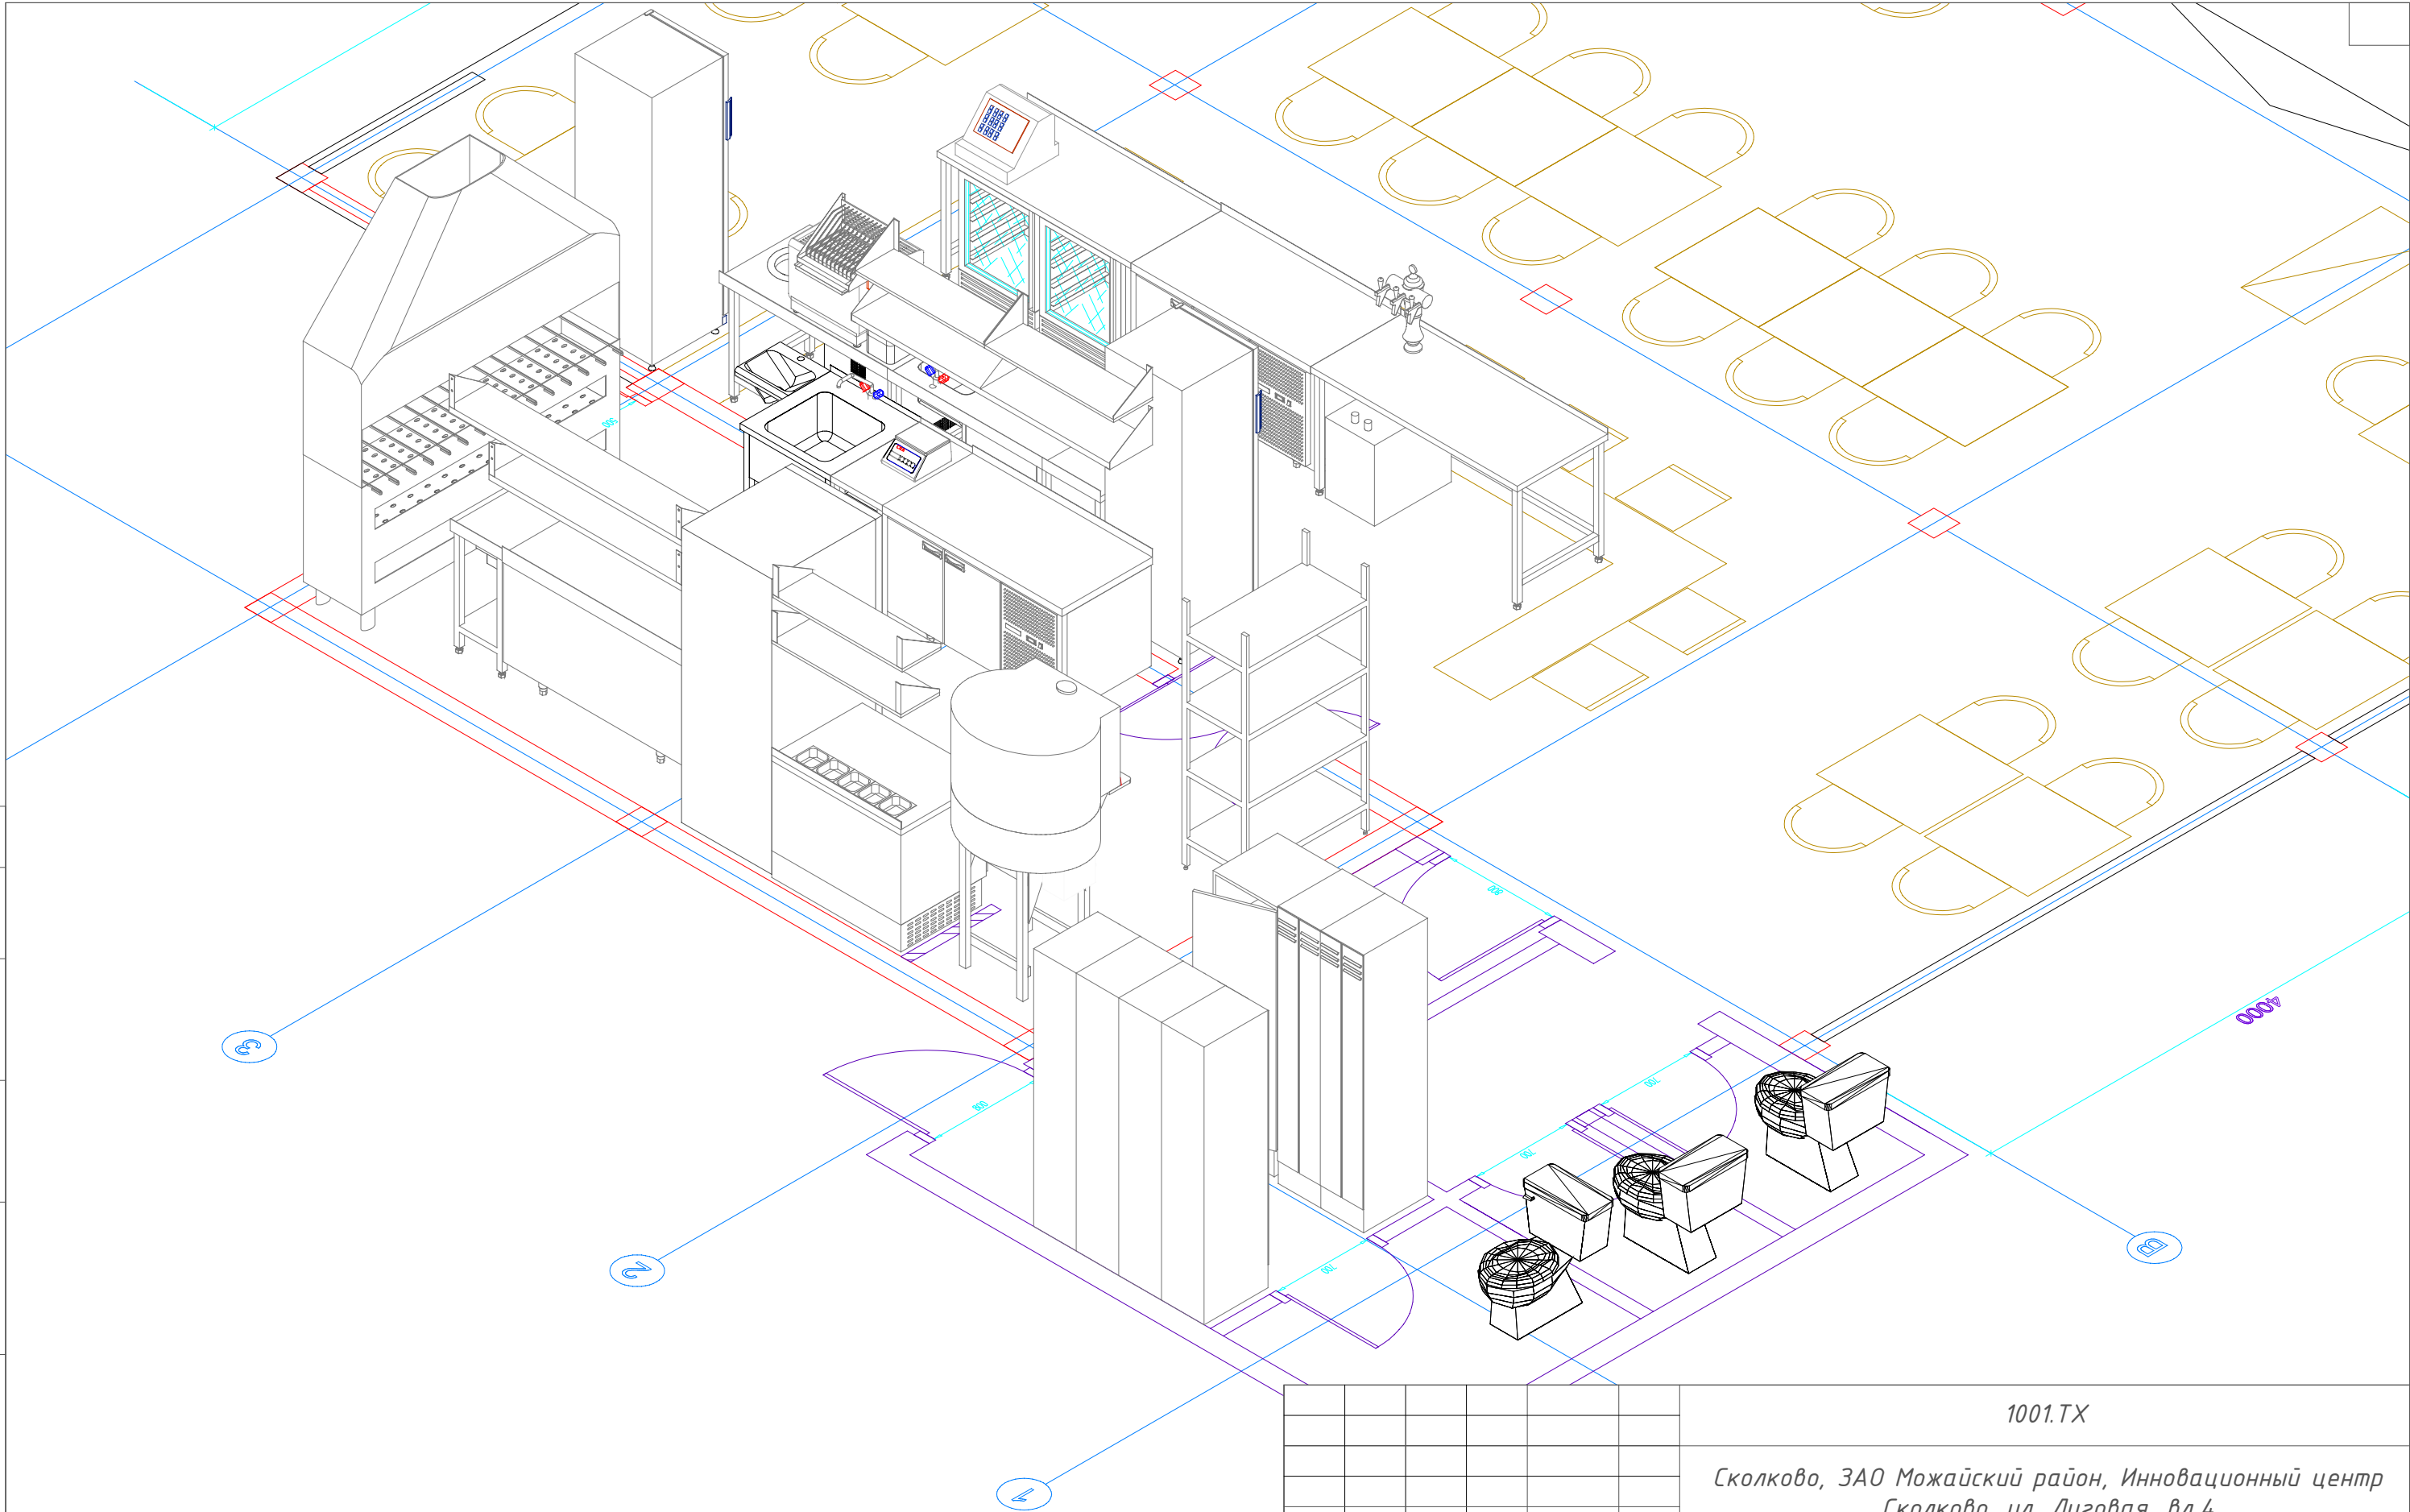


						1001.TX		
						Сколково, ЗАО Можайский район, Инновационный центр Сколково, ул. Луговая, вл.4		
Изм.	Кол.уч.	Лист	док.	Подпись	Дата	Летняя веранда Кафе "Дым" на 46 пос. мест	Стадия П	Лист 9
Рук.пр-та.		Сапарский			21.04.2021	План на отметке +0.000		
Технолог		Савочкин			21.04.2021			
Заказчик								

Согласовано


Взам. инв. №

Подп. и дата

Инв. № подл.

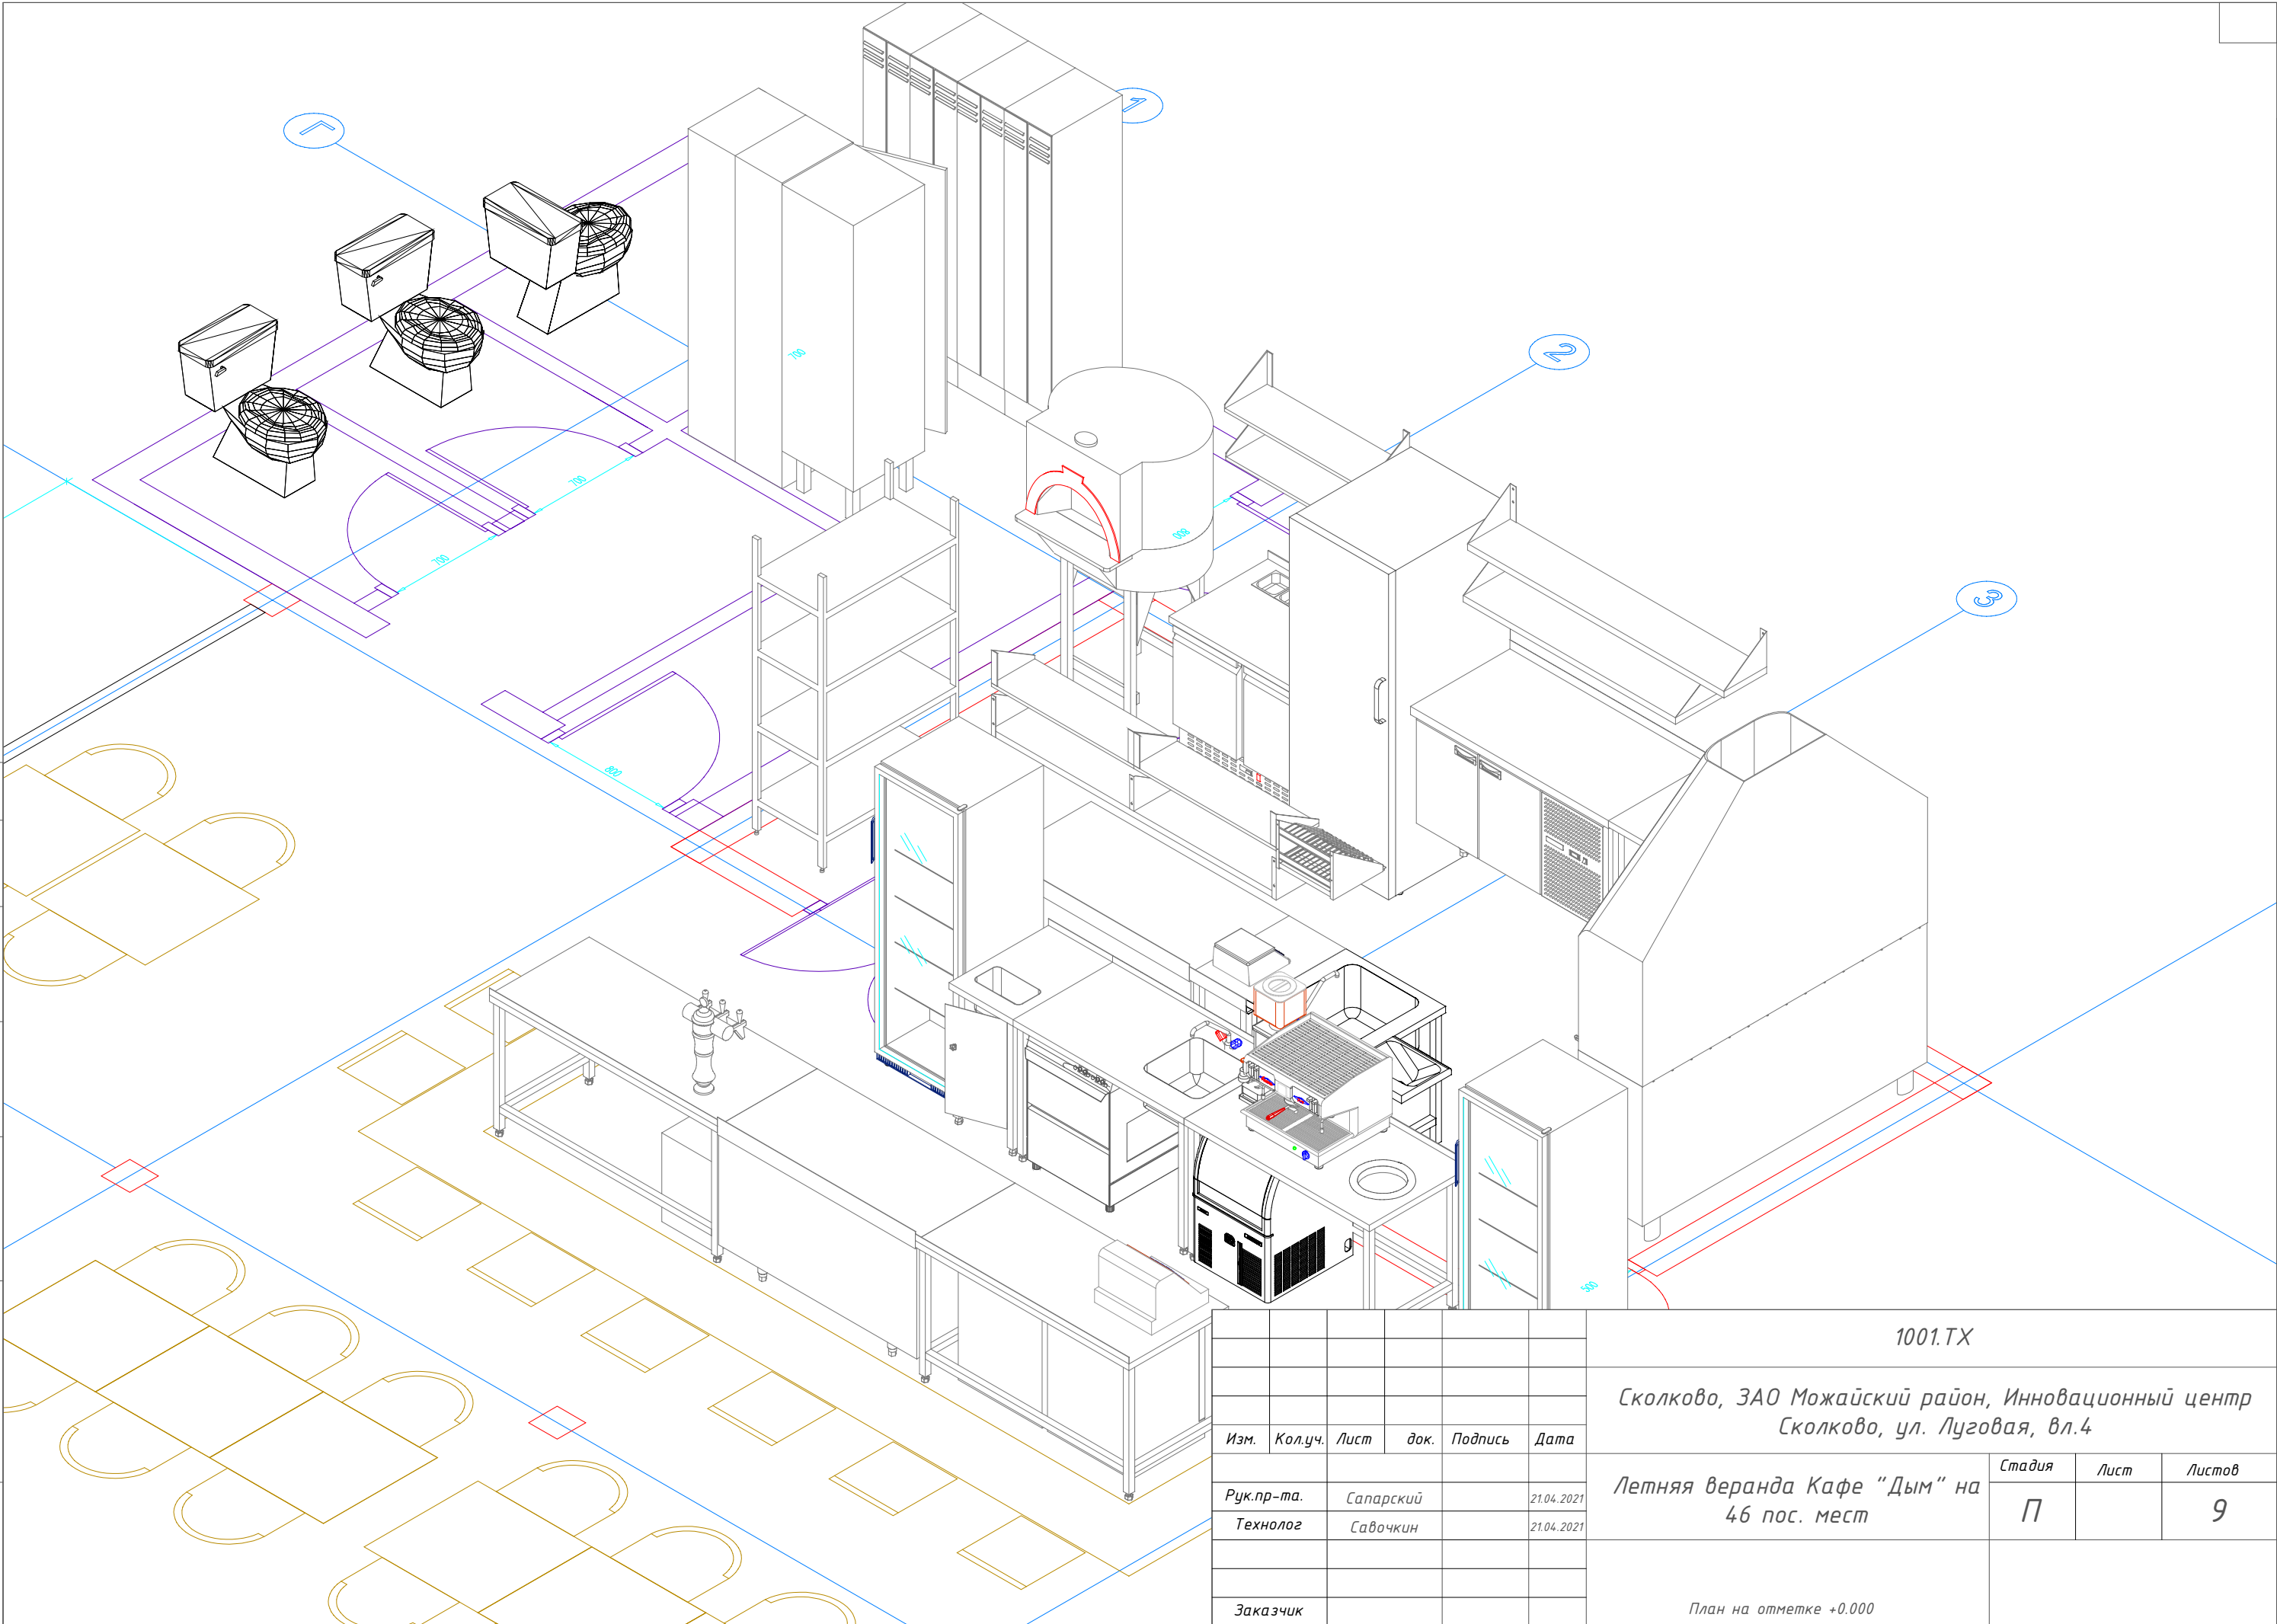

						1001.TX		
						Сколково, ЗАО Можайский район, Инновационный центр Сколково, ул. Луговая, вл.4		
Изм.	Кол.уч.	Лист	док.	Подпись	Дата	Летняя веранда Кафе "Дым" на 46 пос. мест	Стадия П	Лист 9
Рук.пр-та.		Сапарский			21.04.2021	План на отметке +0.000		
Технолог		Савочкин			21.04.2021			
Заказчик								

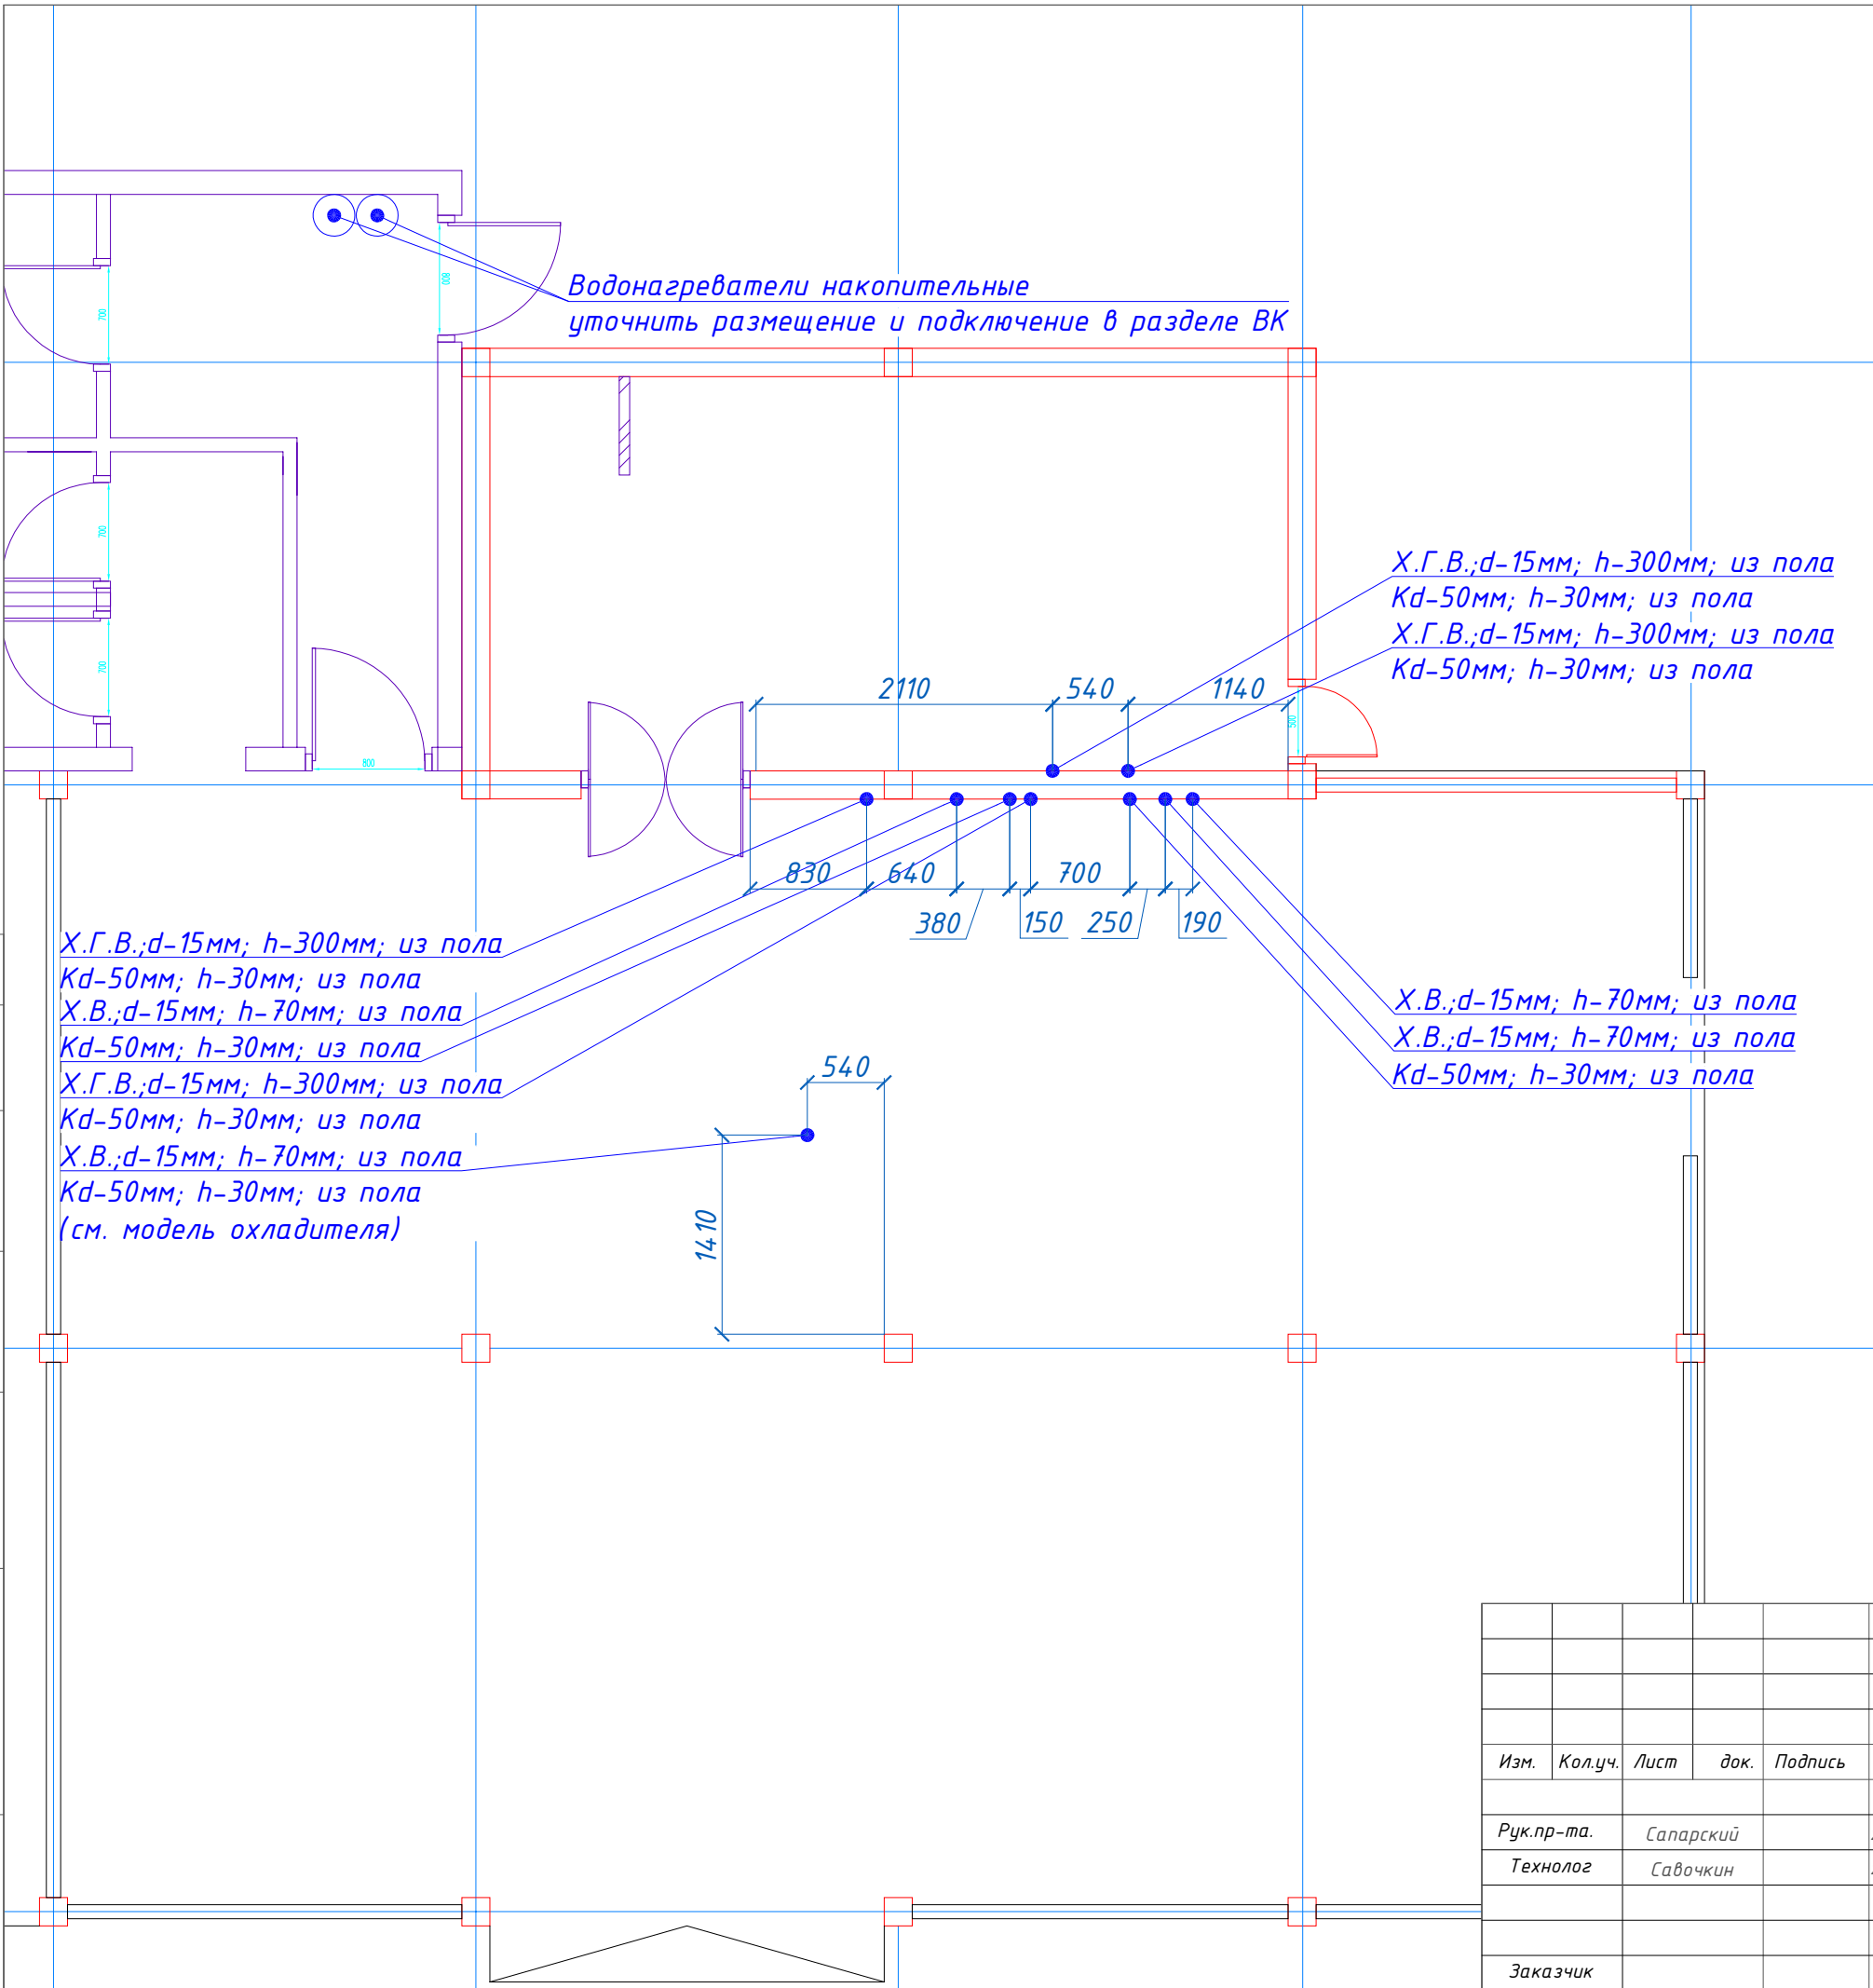

Условные обозначения


- X.B. – подвод холодной воды
- X.Г.B – подвод холодной и горячей воды
- d – диаметр трубопровода
- K – отвод в канализацию
- h – высота подводов от чистого пола в мм
- ⊠ – Трап d=100мм

Примечания

- Прокладка труб водопровода и канализации должна осуществляться в плоскости стен и пола
- Слив от оборудования в канализацию предусмотреть в ближайший трап или канализационную сеть с разрывом струи не менее 20мм.
- Выводы из пола должны быть выполнены максимально приближенными к примыкающей стене, или отнесены от неё на расстояние 150мм.
- Вентиля G 1/2" возможно использовать угловые или прямые полнопроходные, монтировать максимально приближенно к стене
- Давление холодной и горячей воды в системе водоснабжения в пределах 150 кПа ÷ 600 кПа; при необходимости с установкой насоса, повышающего давление либо понижающего редуктора

Согласовано				
Инв. № подл.	Взам. инв. №	Подп. и дата		

						1001.TX			
						Сколково, ЗАО Можайский район, Инновационный центр Сколково, ул. Луговая, вл.4			
Изм.	Кол.уч.	Лист	док.	Подпись	Дата				
						Летняя веранда Кафе “Дым” на 46 пос. мест	Стадия	Лист	Листов
Рук.пр-та.		Сапарский		21.04.2021			П		9
Технолог		Савочкин		21.04.2021		План расположения выводов воды и канализации План на отметке +0.000			
Заказчик									

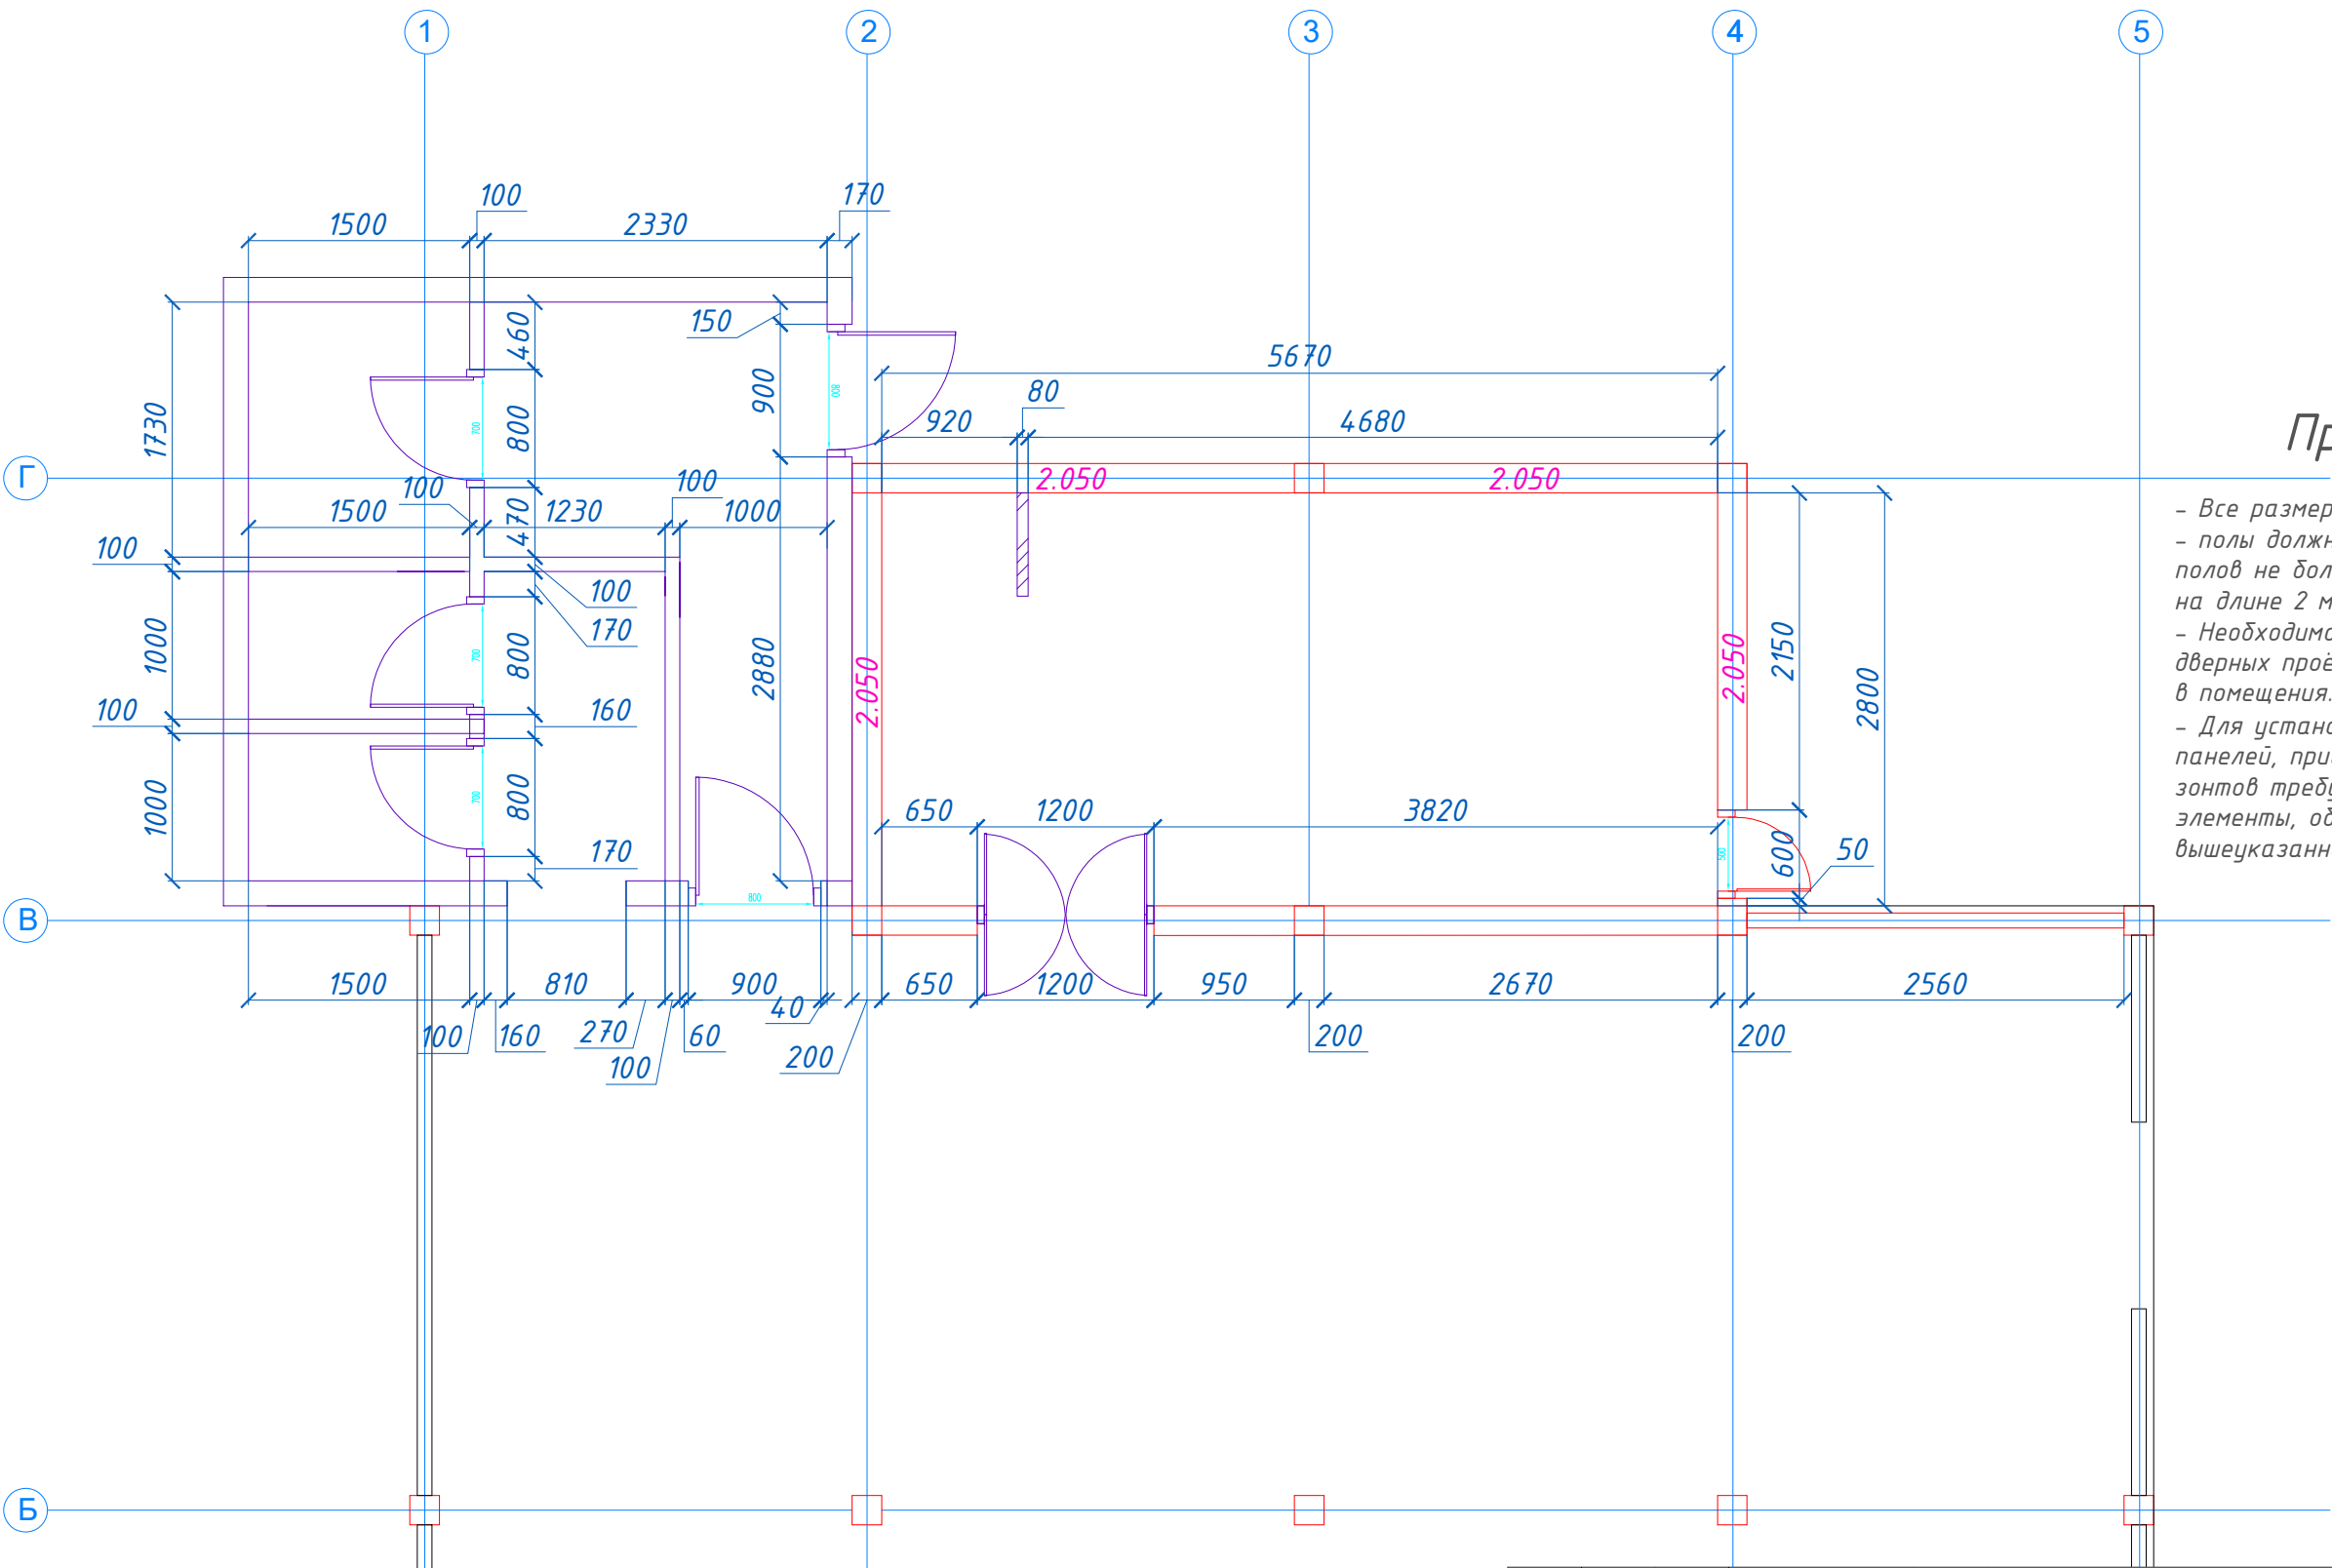

Примечания

- Все размеры указаны в мм от чистого пола и стен.
- полы должны быть строго горизонтальными, уклон полов не более +/- 5 мм относительно нулевой линии на длине 2 м.
- Необходимо предусмотреть требуемые размеры дверных проёмов для обеспечения заноса оборудования в помещения.
- Для установки навесного оборудования (полок, панелей, пристенных и центральных вентиляционных зонтов требуется предусмотреть закладные элементы, обеспечивающие надёжное крепление вышеуказанного оборудования.

Согласовано					
Инв. № подл.	Подп. и дата	Взам. инв. №			

						1001.ТХ			
						Сколково, ЗАО Можайский район, Инновационный центр Сколково, ул. Луговая, вл.4			
Изм.	Кол.уч.	Лист	док.	Подпись	Дата				
						Летняя веранда Кафе “Дым” на 46 пос. мест	Стадия	Лист	Листов
Рук.пр-та.		Сапарский			21.04.2021		П		9
Технолог		Савочкин			21.04.2021	План расположения перегородок План на отметке +0.000			
Заказчик									