



Общество с ограниченной ответственностью "УНИКАЛЬНЫЕ ТЕХНОЛОГИИ"
СРО «ОПОРА» СРО-П-147-09032010, Рег. номер 368

Кафе узбекской и европейской кухни на 36 пос. мест
по адресу: г. Москва, Павелецкая пл., д.1

ПРОЕКТНАЯ ДОКУМЕНТАЦИЯ

Сведения об инженерном оборудовании, о сетях
инженерно-технического обеспечения, перечень
инженерно-технических мероприятий, содержание
технологических решений

Технологические решения. Кафе.

148.TX

Согласованно		

Инов. № подл.	Подп. и дата	Взам. Инов. №

Генеральный директор

Сухов С.А.

Содержание

Обозначение	Наименование	страница
	Титульный лист	
1048.ТХ.	Содержание	1
1048.ТХ.	Справка главного специалиста технолога	2
1048.ТХ.	Пояснительная записка	3
1048.ТХ.	Спецификация оборудования	13
1048.ТХ.	План расстановки технологического оборудования	16
1048.ТХ.	Схема движения технологических потоков	17
1048.ТХ.	План расстановки технологического оборудования изометрические виды	18-21

Согласовано

Взам. Инв. №

Подп. и дата

Инв. № подл.

1048.ТХ.

Кафе узбекской и европейской кухни на 36 пос. мест по адресу: г. Москва, Павелецкая пл., д.1

Технологические решения. Кафе.

Стадия	Лист	Листов
П	1	12

Пояснительная записка

ООО «Уникальные Технологии»

Справка главного специалиста технолога

Технические решения, принятые в проектной документации, соответствуют требованиям экологических, санитарно-гигиенических, противопожарных и других норм, действующих на территории Российской Федерации, и обеспечивают безопасную для гигиены и здоровья людей, эксплуатацию объекта, при соблюдении предусмотренных проектной документацией мероприятий.

Главный специалист технолог



Савочкин Н.А.

Согласовано					
Инв. № подл.	Подп. и дата	Взам. Инв. №			

Пояснительная записка.

Настоящая проектная документация Кафе узбекской и европейской кухни на 36 пос. мест по адресу: г. Москва, Павелецкая пл., д.1, разработана на основании:

- Задания на проектирования, утвержденного Заказчиком;
- Федерального закона от 22 июля 2008 г. № 123-ФЗ «Технический регламент о требованиях пожарной безопасности» с изменениями на 2 июля 2013 г.;
- Федерального закона от 30 декабря 2009 г. № 384-ФЗ «Технический регламент о безопасности зданий и сооружений» с изменениями на 2 июля 2013 г.;
- Федерального закона от 21 декабря 1994 года № 69-ФЗ «О пожарной безопасности» с изменениями на 2 июля 2013 г.;
- Положения о составе разделов проектной документации и требованиях к их содержанию, утвержденного Постановлением Правительства РФ от 16 февраля 2008г. № 87 с изменениями на 8 августа 2013 г.;
- МГСН 4.14-98 «Московские городские строительные нормы»;
- СП 118.13330.2012 «Общественные здания и сооружения»;
- СП 60.13330.2012 Отопление, вентиляция и кондиционирование. Актуализированная редакция СНиП 41-01-2003;
- СП 52.13330.2016 «Естественное и искусственное освещение»;
- ГОСТ 31985-2013 Услуги общественного питания. Термины и определения
- САНПИН 2.3/2.4.3590-20 "Санитарно-эпидемиологические требования к организации общественного питания населения»;
- САНПИН 1.2.3685-21 "Гигиенические нормативы и требования к обеспечению безопасности и (или) безвредности для человека факторов среды обитания»
- другими действующими санитарными и строительными нормами и правилами.

Согласовано

Взам. Инв. №

Подп. и дата

Инв. № подл.

1048.ТХ.

Лист

3

Изм. Кол.уч Лист Подок Подп. Дата

Описание предприятий питания.

1. Описание и обоснование проектных решений, направленных на соблюдение требований технологических регламентов.

1.1 Описание предприятий питания.

Предприятие общественного питания запроектировано на первом этаже жилого здания по адресу: г. Москва, пл. Павелецкая, д. 1, кадастровый номер 77:01:0006042:1273. Помещения, назначение: нежилое, общая площадь 129.2 кв.м., перечень помещений: этаж 1, пом. 1 ком. 1–10. Предприятие относится к типу кафе на 36 посадочных мест. Форма обслуживания посетителей – официанты. Предприятие работает на полуфабрикатах, для обслуживания посетителей используется многоразовая и одноразовая посуда (выдача заказов на вынос). Согласно техническому заданию максимально планируемое количество посетителей в день составляет 300 человек, мощность предприятия в смену составляет – 900 условных блюд в сутки.

В составе предприятия предусмотрены следующие помещения: обеденный зал для посетителей на 36 пос. мест, умывальная и санузел гостевой, приемочная, гардероб персонала, санузел персонала, моечная столовой и кухонной посуды, кладовая суточного запаса, доготовочный цех, цех выпечки мучных изделий, горячий и холодный цеха, раздаточная. Режим работы предприятия: с 09:00 до 21:00, 7 дней в неделю; численность персонала кафе в смену 6 человек, всего – 12 человек.

Таблица 1. Штатное расписание кафе

Наименование подразделения	Наименование должности	Количество в смену	График работы	Группа производственных процессов
Служебный персонал	Администратор	1	2/2 по 12часов	1а
Производственный персонал	Официант	1	2/2 по 12часов	1а
Производственный персонал	Посудомойщица/уборщица	1	2/2 по 12часов	1а
Производственный персонал	Работник буфета-кассир	1	2/2 по 12часов	1а
Производственный персонал	Повар	2	2/2 по 12часов	1а
	Итого человек в смену:	6		
	Всего человек:	12		

Согласовано					
Взам. Инв. №					
Подп. и дата					
Инв. № подл.					

Изм.	Кол.уч	Лист	Подок	Подп.	Дата

1048.ТХ.

Лист

1.2 В составе предприятий предусмотрены следующие помещения (см. графическую часть)

1.3 Обоснование проектных решений, направленных на соблюдение требований технологических регламентов.

Ниже приведено описание основных технологических процессов производства и обслуживания питанием с указанием организации технологических потоков.

Загрузка и полуфабрикатов и продукции осуществляется через вход расположенный на внешней части здания со стороны Павелецкой площади, процедура приемки и загрузки предприятий питания осуществляется до начала работы обеденного зала для посетителей. Данное разделение по времени исключает пресечение потоков загружаемой продукции и посетителей в обеденном зале, а так же потоки персонала и грязной посуды в производственном коридоре. В графической части приведена схема движения потоков на предприятии. Ниже приведен график, по которому осуществляется процедура приемки.

Таблица 2. График приемки и обслуживания

Время осуществления процесса	Описание процесса
08:30–09:00	приемка полуфабрикатов и продукции
09:00–21:00	обслуживание посетителей

Для процессов приемки полуфабрикатов и продукции предусмотрено помещение приемочной, где осуществляется контроль: температуры для быстро портящихся продуктов, упаковка, внешний вид. Далее продукция распределяется в кладовую суточного запаса, которая оборудована холодильным и морозильным шкафами, шкафом купе из нержавеющей стали для хранения сыпучих продуктов. Напитки хранятся на стеллаже, установленном в помещении приемочной.

Персонал попадает на предприятие через отдельный вход, со стороны двора дома. Спец. одежда персонала хранится в шкафчиках в гардеробе персонала, шкафы для производственного персонала предусмотрены согласно штатному расписанию и имеют 2 ячейки для раздельного хранения домашней и рабочей одежды. Шкафчик для верхней одежды служебного персонала, на две секции, предусмотрен в помещении приемочной. В помещении приемочной оборудовано не постоянное рабочее место для администратора кафе.

Ассортиментный перечень реализуемой продукции включает: готовые пищевые продукты и напитки промышленного производства в заводской индивидуальной упаковке; приготовление кулинарных изделий и блюд, таких как: первые и вторые блюда, холодные закуски и салаты, напитки, изделия из теста, приготовленные на

Согласовано					
Инов. № подл.	Подп. и дата	Взам. Инов. №			

основе полуфабрикатов поступающих на предприятие в индивидуальной заводской упаковке. Полуфабрикаты поступают на предприятие в одноразовой упаковке.

Для приготовления блюд используется следующая продукция: порционные мясные, рыбные, а также полуфабрикаты из птицы в индивидуальной упаковке, очищенные овощи в индивидуальной вакуумной упаковке, обработанное яйцо. Свежие овощи и зелень. Хранение полуфабрикатов и готовой продукции осуществляется в помещении кладовой суточного запаса с учетом товарного соседства и требуемых температурных режимов. Мука и сыпучие товары размещаются на полках закрытого шкафа купе.

Для процессов распаковки полуфабрикатов, мытья зелени и свежих овощей, а так же перетаривания продукции из индивидуально заводской упаковки предусмотрено отдельное помещение – доготовочный цех. Для данных процессов предусмотрены отдельные рабочие столы и моечные ванны. Затем, подготовленные полуфабрикаты подаются в горячий и холодный цех и цех выпечки мучных изделий, которые имеют связь с раздаточной. На раздаче блюда выдаются официанту или посетителю в обеденный зал. Тепловая обработка продуктов осуществляется при помощи плиты с духовым шкафом, жарочной поверхности, фритюра. Для приготовления мучных изделий из теста предусмотрен электрический тандыр.

Выдача блюд осуществляется через раздаточную стойку, оснащённую холодильным столом и тепловыми лампами. Для выдачи и демонстрации изделий из теста предусмотрена нейтральная витрина с подсветкой. В зоне раздаточной так же осуществляется приготовление и выдача напитков, установлен кассовый аппарат.

Мытье и хранение столовой и кухонной посуды осуществляется в отдельном помещении, при помощи моечных ванн и посудомоечной машины. Моечная посуды имеет удобную связь с обеденным залом, для приема грязной посуды и передаточное окно смежное с раздачей для выдачи чистой посуды.

Для хранения моющих и дезинфицирующих средств, инвентаря для санитарной обработки общественной и производственной зоны установлен отдельный шкафчик (КУИ). Инвентарь для мытья туалетов имеет сигнальную окраску и хранится отдельно, в шкафчике, установленном в санузле персонала.

Все помещения кафе с мокрыми процессами оборудуются сливными трапами с уклоном к ним.

Удаление пищевых отходов осуществляется после окончания работы предприятия или по мере необходимости, при заполнении бака отходами на 2/3,

Согласовано			
Взам. Инв. №			
Подп. и дата			
Инв. № подл.			

Изм.	Кол.уч	Лист	Нодок	Подп.	Дата	1048.ТХ.	Лист
							6

Вывоз отходов с площадки производится специализированным транспортом в соответствии с утвержденным графиком.

Планировка помещений, их конструкция, размещение и размер обеспечивает последовательность (поточность) технологических процессов, исключаются встречные потоки полуфабрикатов и готовой продукции, использованной и продезинфицированной посуды, а также встречное движение посетителей и персонала, участвующего в приготовлении продукции.

Установленная суммарная потребляемая мощность по технологическому оборудованию составит согласно спецификации оборудования: 55,54 кВт/час. Коэффициент одновременного использования оборудования в предприятии 0,8.

Твёрдые и бытовые отходы (ТБО) образуются в служебно-бытовых помещениях персонала, производственных помещениях предприятий общепита обеденных залах.

Содержание основных компонентов ТБО: органические соединения. Агрегатное состояние: твёрдое, класс опасности – IV.

Пищевые отходы образуются при приготовлении пищи и обслуживании посетителей в предприятиях общественного питания. Для сбора пищевых отходов в помещениях моечных предусматривается установка герметично закрывающегося бака для отходов, с установленным в нём полиэтиленовым пакетом. Содержание основных компонентов пищевых отходов: органические соединения. Агрегатное состояние: твёрдое. Класс опасности – IV. Ориентировочное количество пищевых отходов составит:

где: 900 – производительность предприятия общественного питания (условных блюд столовых и изделий в сутки); Средняя плотность пищевых отходов принимается 190 кг/м³.

Осуществляются на основании постоянных договоров заключенных со специализированными и аккредитованными организациями. Во всех производственных помещениях установлены инсектицидные лампы для борьбы с летучими насекомыми.

						1048.ТХ.	Лист
							7
Изм.	Кол.уч	Лист	№ док	Подп.	Дата		

5. Охрана труда, техника безопасности и производственная объекта.

В соответствии с санитарными правилами и нормами технологического проектирования, а также с учетом действующих ведомственных инструкций для профильных предприятий охрана труда и техника безопасности обеспечивается следующими мероприятиями:

6.1. Для компенсации физических факторов:

6.1.1. Применением сертифицированного оборудования;

6.1.2. Проектные мероприятия по предотвращению поражением электротоком разработаны согласно действующим нормам; в проекте выполнено заземление всего оборудования; для местного освещения применено пониженное напряжение;

6.1.3. Для работы используется специализированные инструменты, облегчающие техпроцесс; проводится профессиональный отбор и обучение работников;

6.1.4. Тепловое оборудование оснащено световой системой сигнализации свидетельствующей о нарушении его работы;

6.1.5. Запыленность воздуха рабочей среды, температура, влажность и подвижность воздуха приняты в соответствии с нормами и учтены при разработке вентиляции; для поддержания нормативного состояния микроклимата в помещениях запроектированы соответствующие инженерные системы;

6.1.6. В соответствии с нормами предусмотрено естественное и искусственное освещение;

6.2. Для компенсации химических факторов:

6.2.1. Рабочие места с избыточным выделением тепла и влаги оборудованы местной вытяжной вентиляцией.

6.3. Для компенсации психофизиологических факторов:

6.3.1. Режим работы и отдыха персонала по проекту соответствует действующему законодательству;

6.3.2. Согласно действующим нормам и численности им обеспечены соответствующие санитарно-бытовые помещения.

Дополнительные мероприятия в процессе эксплуатации предусматривают:

- вывешивание предупредительных плакатов, правил выполнения работ, инструкций по технике безопасности для всех категорий работников, номеров телефонов аварийных, пожарных служб и медицинских учреждений;

- прохождение производственным персоналом инструктажа по технике безопасности;

- технический ремонт и обслуживание применяемого оборудования предусматривается специализированными организациями;

Согласовано

Взам. Инв. №

Подп. и дата

Инв. № подл.

1048.TX.

Лист

8

Изм. Кол.уч Лист Недок Подп. Дата

- расстояния между оборудованием и проходы обеспечивают легкую доступность при работе и обслуживании;

- обеспечена бесплатная выдача спецодежды.

Благоприятные условия труда на объекте также обеспечиваются устройством:

- отопления и вентиляции, выполнены в соответствии с действующими нормами;

- цветового решения интерьеров;

- применения отделочных и строительных материалов с учетом технологии и условий труда;

- обеспечением связью и сигнализацией;

- рациональной планировкой основных и вспомогательных помещений.

Для обеспечения пожарной безопасности проектом разработаны пути эвакуации, система оповещения о пожаре. Предприятия должны оснащаться первичными средствами пожаротушения.

Внутренние и внешние поверхности технологического оборудования предприятия общественного питания по мере их загрязнения и в конце смены очищаются, промываются горячей водой и дезинфицируются. Производственные столы в конце смены моют с применением моющих и дезинфицирующих средств, промывают горячей водой (40–50 С) и насухо протирают сухой чистой ветошью.

В конце рабочего дня во всех помещениях производится влажная уборка с применением моющих и дезинфицирующих средств. Текущая уборка помещений производится постоянно, своевременно и по мере необходимости.

Для хранения уборочного инвентаря и дез. средств предусмотрены отдельные шкафы, в санузле для персонала установлен комбинированный рукомойник со специальной низкой ванной с возможностью забора холодной и горячей воды, применяемой для уборки производственных помещений.

7. Освещение

Для производства высококачественной продукции необходимо обеспечить освещение не менее 300 люкс в горячем, холодном, помещении для мучных изделий. В доготовочных и моечных посуды не менее 200 люкс. В помещении приемочной необходимо обеспечить люминесцентное либо светодиодное освещение 300 люкс.

В обеденной зоне предприятия желательно иметь освещение от 300 до 500 люкс над линией раздачи и столиками принятия пищи.

В остальных бытовых и производственных помещениях для установки уровня освещения использовать типовые требования. В качестве осветительных приборов во всех производственных и складских помещениях, использовать светильные приборы со спец. защитой для предотвращения попадания стекла в продукты.

Согласовано					
Изм. № подл.	Подп. и дата	Взам. Инв. №			
Изм.	Кол.уч	Лист	Подп.	Дата	

Светильники IP50 для пыльных сред, защищенные от быстрого внутреннего загрязнения. Снаружи светильники IP50 могут легко очищаться. На объектах пищевой промышленности следует применять закрытые светильники, в которых предусмотрена защита от попадания осколков стекла от случайно разбитых ламп в рабочую зону. Хотя степень защиты предусматривает обеспечение работоспособности самого светильника, она также означает, что отдельные частицы не могут выпасть из корпуса, что соответствует требованиям пищевой промышленности.

Светильники IP54 можно мыть без каких-либо отрицательных последствий. Такие светильники также часто используются для освещения цехов пищевой промышленности, рабочих помещений с повышенным содержанием пыли и влаги, а также под навесами.

8.1 Вентиляция.

Проектом должна быть предусмотрена вытяжная вентиляция с механическим и естественным побуждением в помещениях во всех производственных и бытовых помещениях.

Во всех температурных зонах должны быть установлены листы контроля температуры и термометры. Согласно системе производственного контроля не реже 1 раза в 4 часа ответственный дежурный персонал должен осуществлять контроль температуры и делать запись в рабочих листах.

Систему отопления запроектировать согласно решений базового проекта. Приточно-вытяжную вентиляцию запроектировать с учетом объемов приточного воздуха, подаваемого непосредственно в производственные помещения, а также учесть все тепловыделения от технологического оборудования, технических систем,

						1048.ТХ.	Лист
							10
Изм.	Кол.уч	Лист	№док	Подп.	Дата		

1048.TX.

Согласовано

Взам. Инв. №

Подп. и дата

ИНВ. № подл.

электроприборов и освещения (по данным смежных разделов), горячей пищи, поступлений от солнечной радиации через оконные проемы, а так же влаговыделения пищи и мойки посуды, количества посадочных мест и работающего персонала.

Коэффициент одновременности работы технологического оборудования принять согласно требований норм.

Количество приточного воздуха в зале должно составлять не менее 60% от кухонной вытяжки, для того, чтобы организовать движение воздуха из зала в помещение кухни, во избежание запахов.

Запроектировать приточно-вытяжные системы помещений, исходя из условий их размещения и разделения (общеобменной, производственной, санитарно-технической и т.п.).

Движение воздуха в помещениях производственной группы принимать не более 0,2–0,5 м/сек (в зависимости от времени года и назначения помещения).

Требования к отдельным помещениям:

А) Помещения для посетителей:

1) Залы для посетителей

Выполнить приточно-вытяжную вентиляцию на основании теплотехнического и аэродинамических расчетов. Расход воздуха на посетителей и персонал принимать согласно требований нормативной документации. Расчетное количество посетителей в залах равно количеству посадочных мест.

2) Прочие помещения для посетителей

Выполнить общеобменную вентиляцию для подпора воздуха в необходимом объеме согласно требований нормативной документации

Б) Помещения зоны технологии предприятия

1) Раздаточная (дуфетная стойка)

Выполнить общеобменную вентиляцию с учетом единого объема с залами и тепловыделениями от установленного оборудования на основании теплотехнического и аэродинамических расчетов. Предусмотреть воздухораспределение с учетом нераспространения запахов в зале для посетителей.

2) Доготовочный цех, горячая зона

Выполнить приточно-вытяжную вентиляцию на основании теплотехнического и аэродинамических расчетов. Системы вентиляции запроектировать с применением вытяжных локализирующих устройств. Для расчета воздухообмена принимать: температуру воздуха, удаляемого через зонты, и локализирующие устройства над

Согласовано					
Инд. № подл.	Взам. Инв. №	Подп. и дата			
Изм.	Кол.уч	Лист	Нодок	Подп.	Дата

технологическим оборудованием, выделяющим тепло, 42 градуса, температуру воздуха под потолком 30 градусов. В горячей зоне должно быть обеспечено разряжение, достигаемое подачей в обеденный зал около 60% приточного воздуха, предназначенного для вентиляции горячего цеха. Подачу приточного воздуха следует осуществлять в рабочую зону.

3) Зона моечной столовой и кухонной посуды

Выполнить приточно-вытяжную вентиляцию на основании теплотехнического и аэродинамических расчётов. Локализовать тепловыделения и влаговыведения установкой вытяжных решеток над моечными ваннами и посудомоечной машины. Кратность воздухообмена принять по расчету, но не менее:

- приток 4 Крат.
- вытяжка 6 Крат.

4) Приемочная

Количество подаваемого воздуха рассчитать по количеству людей, работающих и находящихся в зоне помещения.

5)Кладовые

Выполнить общеобменную систему вентиляции в помещении из расчета:

- вытяжка 2 крат.

6) Служебно-бытовые помещения, санузел для персонала

Запроектировать в объеме санитарно-технической системы вентиляции вытяжные системы из туалетов находящихся в рабочих зонах из расчета 75 м.куб/час на один унитаз и писсуар.

7) Раздевалка для персонала

Выполнить общеобменную вентиляцию для подпора воздуха в необходимом объеме, согласно требований нормативной документации.

8) Коридоры, тамбуры, шлюзы, технические помещения

Выполнить общеобменную вентиляцию в необходимом объеме для компенсации из сопряженных помещений.

Согласовано

Взам. Инв. №

Подп. и дата

Инв. № подл.

1048.ТХ.

Лист

12


Изм.	Кол.уч	Лист	Подок	Подп.	Дата
------	--------	------	-------	-------	------

		1	2	3	4	5	6	7	8	9	14
Взам.инв.№	Подп. и дата	19	Сифон одинарный D-52мм. со шлангом D-40мм. 0,8 м.	3795		Россия	шт.	2	0	0	
		20	Ловушка для насекомых КТ ВТ-20W. Габариты (ДхШхВ) 410х110х320мм	ВТ-20W		КТ, Финляндия	шт.	1	220	0,035	
		21	Водонагреватель проточный ЭВПЗ-15. Габариты (ДхШхВ) 315х225х530мм	ЭВПЗ-15		ГродТоргМаш, Беларусь	шт.	1	380	15	
			11.Кладовая суточного запаса, КУИ								
		23	Шкаф металлический Шк/Р 1С. Габариты (ДхШхВ) 500х500х1850мм	Шк-37728		КАМИК, Россия	шт.	1	0	0	
		24	Шкаф металлический Шк/К 3С. Габариты (ДхШхВ) 1000х600х1800мм	Шк-5554		КАМИК, Россия	шт.	1	0	0	
		25	Шкаф холодильный Carbotra R700. Габариты (ДхШхВ) 825х755х2050мм	R700		ПОЛЮС, Россия	шт.	1	220	0,4	
		26	Шкаф морозильный Carbotra F700. Габариты (ДхШхВ) 825х755х2050мм	F700		ПОЛЮС, Россия	шт.	1	220	0,6	
			12.Доготовочный цех								
		28	Полка настенная д/досок ПН. Габариты (ДхШхВ) 400х350х300мм	ПН-312143		КАМИК, Россия	шт.	1	0	0	
		29	Весы CAS SW I-5 эл.порционные. Габариты (ДхШхВ) 260х287х137мм	SW-5		CAS, Корея	шт.	1	220	0,01	
		30	Ловушка для насекомых КТ ВТ-20W. Габариты (ДхШхВ) 410х110х320мм	ВТ-20W		КТ, Финляндия	шт.	1	220	0,035	
		31	Рукомойник Компакт настенный бедренный (Смеситель в комплекте). Га- бариты (ДхШхВ) 390х385х310мм	Рн-3604		КАМИК, Россия	шт.	1	0	0	
		32	Слайсер RGV LUSO 22 GS. Габариты (ДхШхВ) 448х363х335мм	LUSO 22 GS		RGV, Италия	шт.	1	220	0,14	
		33	Стол производственный СБП 900*700*850. Габариты (ДхШхВ) 900х700х850мм	С-4268		КАМИК, Россия	шт.	1	0	0	
		34	Ванна моечная ВМ1Р 1200*700*850. Габариты (ДхШхВ) 1200х700х850мм	ВМ-0743		КАМИК, Россия	шт.	1	0	0	
		35	Ванна моечная ВМ1 700*700*850. Габариты (ДхШхВ) 700х700х850мм	ВМ-0726		КАМИК, Россия	шт.	1	0	0	
		36	Стол охлаждаемый GNE 11/TN 1000*700*850. Габариты (ДхШхВ) 1000х700х850мм	GNE 11/TN		HI-COLD, Россия	шт.	1	220	0,42	
		37	Овощерезка Robot Coupe CL 40. Габариты (ДхШхВ) 320х304х590мм	24383		Robot Coupe, Франция	шт.	1	220	0,5	
		38	Смеситель кухонный BISARO Mixer tap H.	176		BISARO, Италия	шт.	2	0	0	
		39	Сифон одинарный D-52мм. со шлангом D-40мм. 0,8 м.. Габариты	3795		Россия	шт.	3	0	0	
		40	Полка настенная ПН 12/3-Р. Габариты (ДхШхВ) 1200х300х250мм	ПН-11594		КАМИК, Россия	шт.	5	0	0	
		41	Контейнер для мусора Rubbermaid . Габариты (ДхШхВ) 559х279х762мм	FG354060GRAY		Россия	шт.	1	0	0	
			13.Цех выпечки мучных изделий								
		42	Стол охлаждаемый GN 11/TN столешница камень. Габариты (ДхШхВ) 1390х700х850мм	GN 11/TN (камень)		HI-COLD, Россия	шт.	1	220	0,42	
		43	Зонт вытяжной пристенный ВП 1300*1300*350. Габариты (ДхШхВ) 1300х1300х350мм	ВП-0964		КАМИК, Россия	шт.	1	0	0	
		44	Стол производственный СБ 1000*700*850. Габариты (ДхШхВ) 1000х700х850мм	С-15119		КАМИК, Россия	шт.	1	0	0	
		45	Сифон одинарный D-52мм. со шлангом D-40мм. 0,8 м.	3795		Россия	шт.	1	0	0	
		46	Смеситель кухонный BISARO Mixer tap H.	176		BISARO, Италия	шт.	1	0	0	
		47	Тестомес спиральный GAM S-16TSV. Габариты (ДхШхВ) 400х620х730мм	IMPS16TR400TSV		GAM, Италия	шт.	1	380	0,55	
Инв. № подл.											Лист
											2
								ИР.2-2021-РЦ-047-ИОС7.1			
		Изм.	Кол.уч	Лист	№ док.	Подп.	Дата				

		1	2	3	4	5	6	7	8	9	15
		48	Ванна моечная М1 6/7-Р. Габариты (ДхШхВ) 600х700х850мм	ВМ-11579		КАМИК, Россия	шт.	1	0	0	
		49	Полка настенная ПН 12/3-Р. Габариты (ДхШхВ) 1200х300х250мм	ПН-11594		КАМИК, Россия	шт.	2	0	0	
		50	Полка настенная ПН 15/3-Р. Габариты (ДхШхВ) 1500х300х250мм	ПН-11624		КАМИК, Россия	шт.	3	0	0	
		51	Контейнер для мусора Rubbermaid . Габариты (ДхШхВ) 559х279х762мм	FG354060GRAY		Россия	шт.	1	0	0	
		52	Стол охлаждаемый GNE 11/TN. Габариты (ДхШхВ) 1000х700х850мм	GNE 11/TN		HI-COLD, Россия	шт.	1	220	0,42	
		53	Тандыр электрический. Габариты (ДхШхВ) 1300х1300х1100мм			Торговая сеть	шт.	1	380	6	
		54	Витрина нейтральная UNIS Georgia Square Neutral 1000 inox. Габариты (ДхШхВ) 1000х750х1320мм	1436010		UNIS, Чехия	шт.	1	220	0	
		55	Весы CAS SW I-5 эл .порционные. Габариты (ДхШхВ) 260х287х137мм	SW-5		CAS, Корея	шт.	1	220	0,01	
			14.Горячий и холодный цех								
		57	Ванна моечная ВМ1 700*700*850. Габариты (ДхШхВ) 700х700х850мм	ВМ-0726		КАМИК, Россия	шт.	1	0	0	
		58	Стол производственный С. Габариты (ДхШхВ) 800х700х850мм	С-22689		КАМИК, Россия	шт.	1	0	0	
		59	Ловушка для насекомых КТ ВТ-20W. Габариты (ДхШхВ) 410х110х320мм	ВТ-20W		КТ, Финляндия	шт.	1	220	0,035	
		60	Облучатель бактерицидный настенный ОБН-35 (одноламповый). Габариты (ДхШхВ) 482х54х120мм	ОБН-35		Азов, Российская федерация	шт.	1	220	0,15	
				61	Стол СП. Габариты (ДхШхВ) 500х700х850мм	С-6835		КАМИК, Россия	шт.	1	0
62	Зонт вытяжной центральный ВЦ. Габариты (ДхШхВ) 1800х1200х350мм			ВЦ-1148		КАМИК, Россия	шт.	1	0	0	
63	Плита со сплошной поверхностью и жарочным шкафом TECNOINOX RPF70E7. Габариты (ДхШхВ) 700х700х850мм			616013		ТЕCNOINOX, Италия	шт.	1	380	13	
64	Поверхность жарочная TECNOINOX FTL35E7. Габариты (ДхШхВ) 350х700х280мм			616026		ТЕCNOINOX, Италия	шт.	1	380	0	
65	Фритюрница TECNOINOX FR35E7. Габариты (ДхШхВ) 350х700х280мм			616033		ТЕCNOINOX, Италия	шт.	1	380	6	
66	Стол морозильный GNE 11/ВТ. Габариты (ДхШхВ) 1000х700х850мм			GNE 11/ВТ		HI-COLD, Россия	шт.	1	220	0,52	
67	Полка настенная ПН 15/3-Р. Габариты (ДхШхВ) 1500х300х250мм			ПН-11624		КАМИК, Россия	шт.	3	0	0	
68	Подставка ПДО TECNOINOX БН-Т7. Габариты (ДхШхВ) 350х640х570мм			Пд-18915		КАМИК, Россия	шт.	2	0	0	
69	Стол охлаждаемый SLE1-111GN с крышкой. Габариты (ДхШхВ) 1485х700х850мм			SLE1-111GN		HI-COLD, Россия	шт.	1	220	0,71	
70	Весы CAS SW I-5 эл. порционные. Габариты (ДхШхВ) 260х287х137мм			SW-5		CAS, Корея	шт.	1	220	0,01	
		71	Смеситель кухонный BISARO Mixer tap Н.	176		BISARO, Италия	шт.	1	0	0	
		72	Сифон одинарный D-52мм. со шлангом D-40мм. 0,8 м.	3795		Россия	шт.	1	0	0	
		73	Контейнер для мусора Rubbermaid . Габариты (ДхШхВ) 559х279х762мм	FG354060GRAY		Россия	шт.	1	0	0	
		74	Полка настенная д/досок ПН. Габариты (ДхШхВ) 400х350х300мм	ПН-312143		КАМИК, Россия	шт.	1	0	0	
		75	Стол производственный С 500*700*850. Габариты (ДхШхВ) 500х700х850мм			КАМИК, Россия	шт.	1	0	0	
			15.Раздаточная (буфетная стойка)								
		78	Полка настольная ПС. Габариты (ДхШхВ) 1000х300х400мм	ПС-3283		КАМИК, Россия	шт.	1	0	0	
Инв. № подл.											Лист
								ИР.2-2021-РЦ-047-ИОС7.1			3
		Изм.	Кол.уч	Лист	№ док.	Подп.	Дата				

Инв. № подл.	Подп. и дата	Взам.инв.№

1	2	3	4	5	6	7	8	9	16
79	Кофемашина Saeco Royal Cappuccino Redesign (серебр-черный). Габариты (ДхШхВ) 390х410х395мм	Royal Cap Redes с/ч		Saeco, Италия	шт.	1	220	2,3	
80	Кипятильник STARFOOD WB-10A. Габариты (ДхШхВ) 280х310х395мм	WB-10A		STARFOOD, Тайвань	шт.	1	220	2	
81	Шкаф холодильный СО СТЕКЛОМ TEFCOLD BC85. Габариты (ДхШхВ) 503х560х775мм	114879		TEFCOLD, Дания	шт.	1	220	0,075	
82	Шкаф морзильный СО СТЕКЛОМ TEFCOLD UF100G. Габариты (ДхШхВ) 610х540х670мм	114243		TEFCOLD, Дания	шт.	1	220	0,23	
83	Стол производственный СБП. Габариты (ДхШхВ) 500х700х850мм	C-4391		КАМИК, Россия	шт.	1	0	0	
84	Hatco Corporation Лампа-мармит подвесная серии DL, мод. DL-400-RL. Габариты (ДхШхВ) 156х156х216мм	DL-400-RL		НАТСО, США	шт.	2	220	0,25	
85	Стол охлаждаемый GNE 11/TN 1000*700*850. Габариты (ДхШхВ) 1000х700х850мм	GNE 11/TN		HI-COLD, Россия	шт.	1	220	0,42	
86	Стол производственный СБ 1250*700*850. Габариты (ДхШхВ) 1250х700х850мм	C-4246		КАМИК, Россия	шт.	1	0	0	
	01.Обеденный зал								
87	Стол обеденный прямоугольный. Габариты (ДхШхВ) 1200х800х730мм	Стол_120х80		Торговая сеть	шт.	8	0	0	
88	Сту обеденный. Габариты (ДхШхВ) 450х420х830мм	Стул_45х42		Торговая сеть	шт.	36	0	0	
89	Стол обеденный прямоугольный. Габариты (ДхШхВ) 600х600х730мм	Стол_60х60		Торговая сеть	шт.	2	0	0	
Суммарная мощность кВт:								55,54	
						ИР.2-2021-РЦ-047-ИОС7.1			Лист
									4
Изм.	Кол.уч	Лист	№ док.	Подп.	Дата				

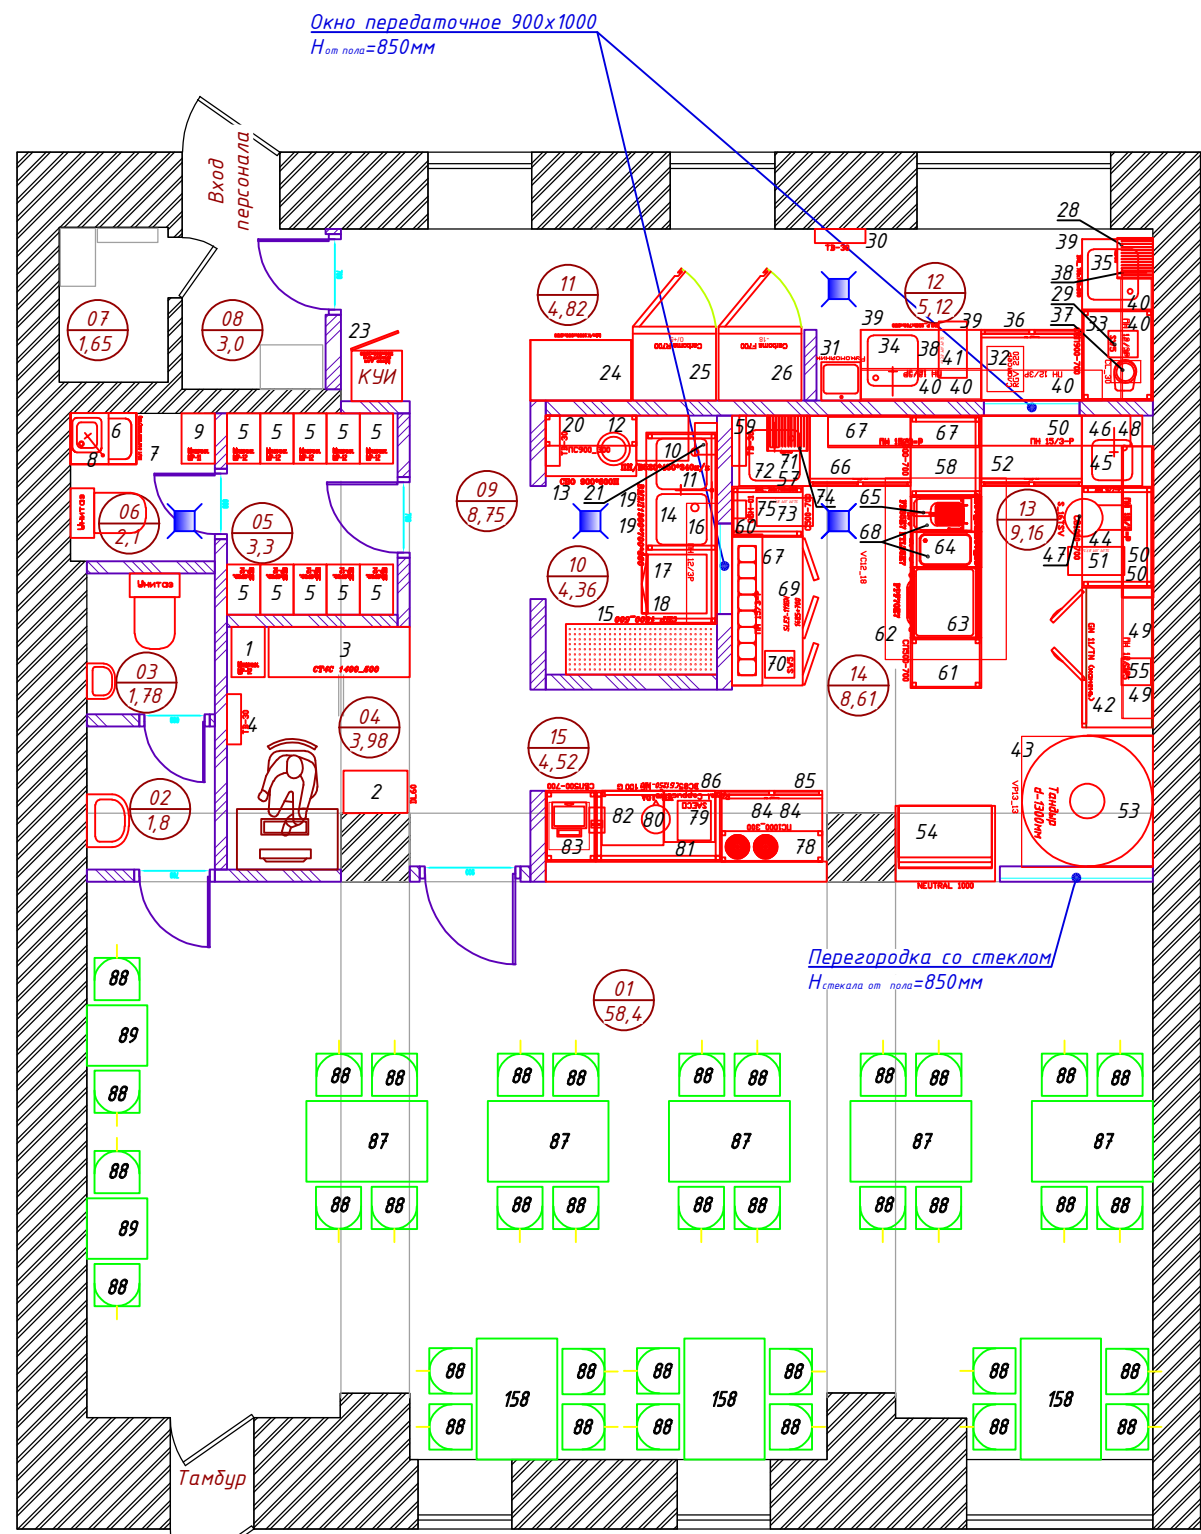


Экспликация помещений


Номер помещ ения	Наименование	Площадь, м ²
1	Обеденный зал на 36 пос. мест	58,4
2	Умывальная	1,8
3	Сан. узел гостевой	1,78
4	Приемочная	3,98
5	Гардероб персонала	3,3
6	Сан. узел персонала	2,1
7	Электрощит	1,65
8	Тамбур	3,0
9	Коридор	8,75
10	Моечная столовой и кухонной посуды	4,36
11	Кладовая суточного запаса	4,82
12	Доготовочный цех	5,12
13	Цех выпечки мучных изделий	9,16
14	Горячий и холодный цех	8,61
15	Раздаточная (буфетная стойка)	4,52
ИТОГО:		121.4

Масштаб 1:75

Условные обозначения

✕ - Трап d=50мм

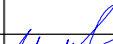						1048.ТХ			
						Кафе узбекской и европейской кухни на 36 пос. мест по адресу: г. Москва, Павелецкая пл., д.1			
Изм.	Кол.уч.	Лист	док.	Подпись	Дата	Технологические решения. Кафе.	Стадия	Лист	Листов
Разработал		Савочкин			15.12.2021		П	1	6
Проверил		Ложкомоев			15.12.2021				
						План расстановки технологического оборудования План на отметке +0.000	ООО «Уникальные Технологии»		
Н.контр		Савочкин			15.12.2021				

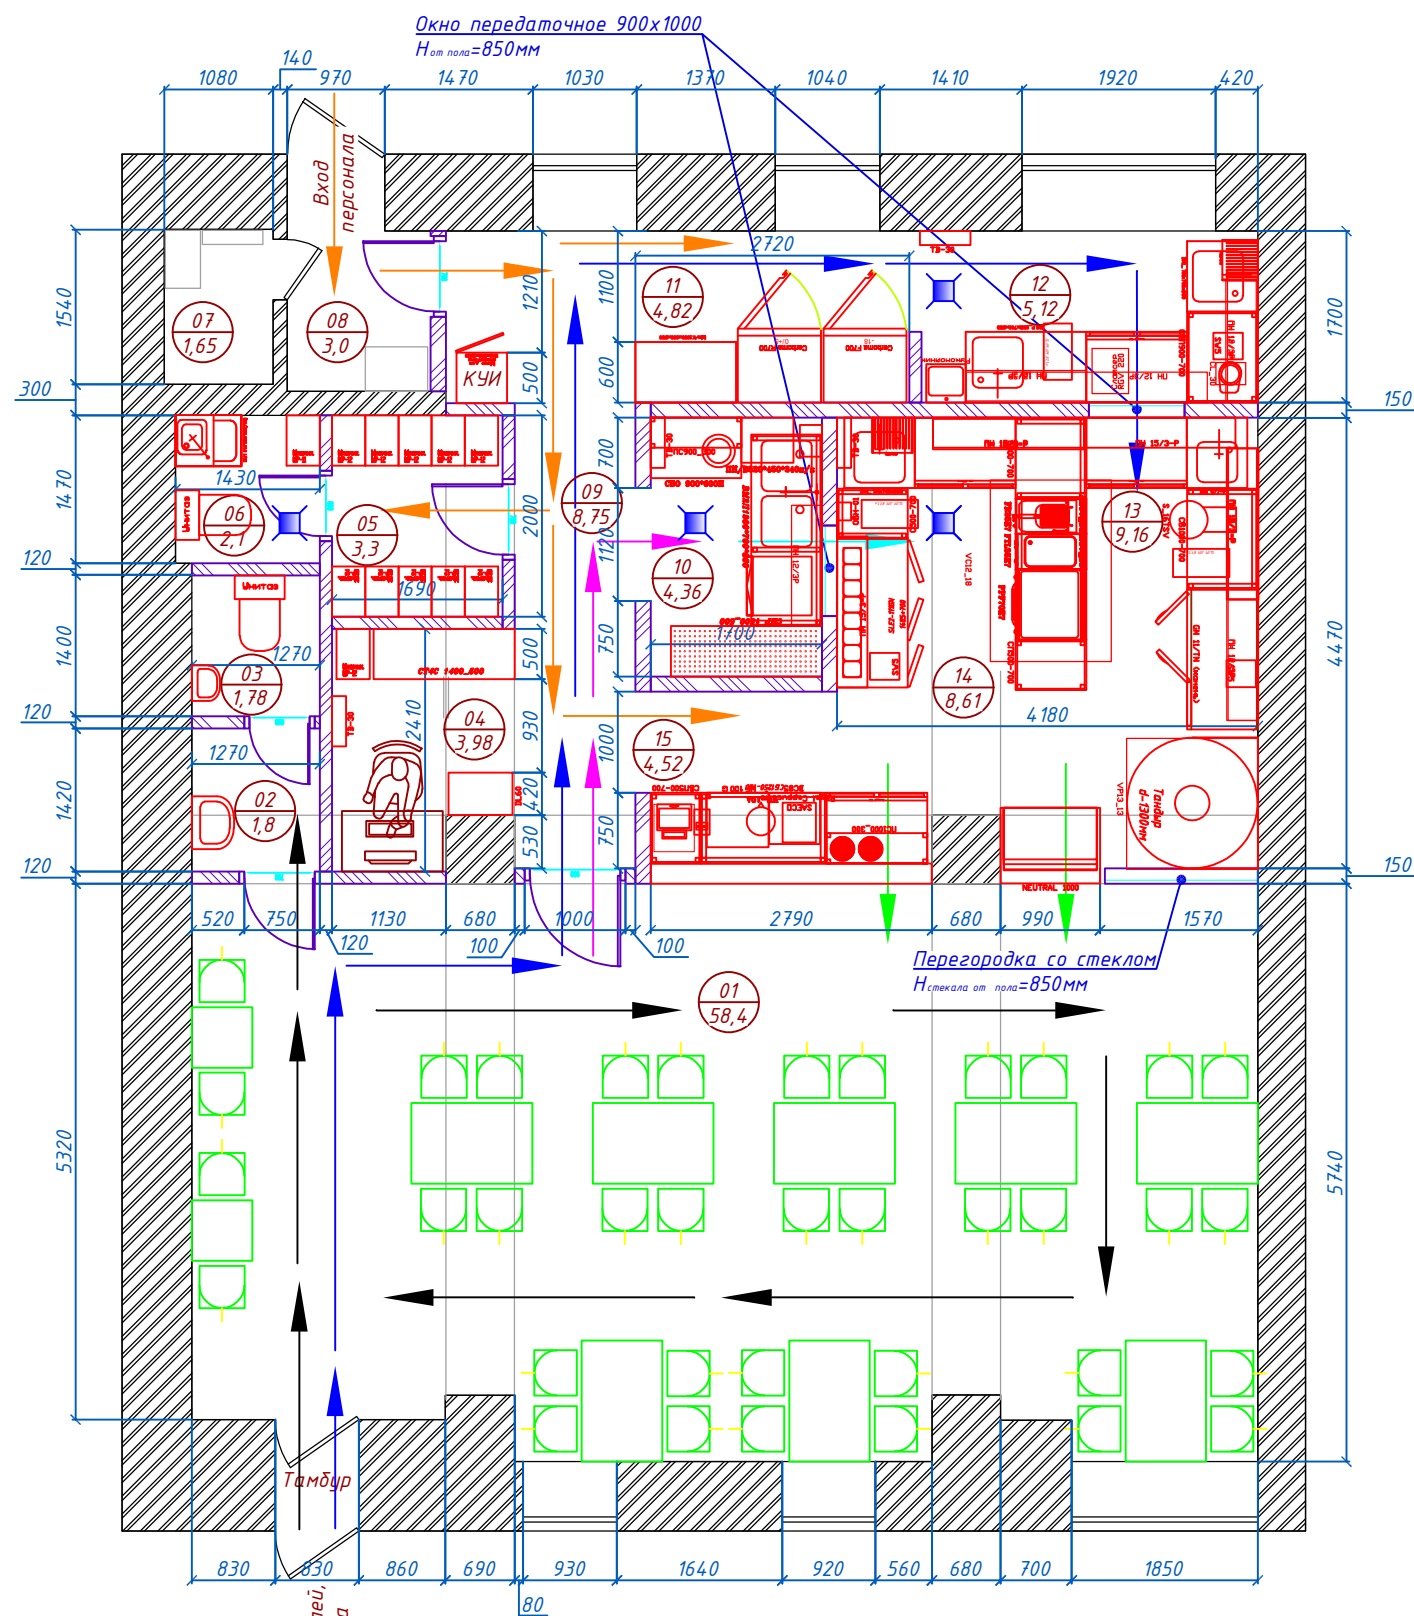

Условные обозначения
✕ - Трап d=50mm

Экспликация помещений


Номер помещ ения	Наименование	Площадь, м ²
1	Обеденный зал на 36 пос. мест	58,4
2	Умывальная	1,8
3	Сан. узел гостевой	1,78
4	Приемочная	3,98
5	Гардероб персонала	3,3
6	Сан. узел персонала	2,1
7	Электрощит	1,65
8	Тамбур	3,0
9	Коридор	8,75
10	Моечная столовой и кухонной посуды	4,36
11	Кладовая суточного запаса	4,82
12	Доготовочный цех	5,12
13	Цех выпечки мучных изделий	9,16
14	Горячий и холодный цех	8,61
15	Раздаточная (буфетная стойка)	4,52
ИТОГО:		121.4

Масштаб 1:75

						1048.ТХ			
						Кафе узбекской и европейской кухни на 36 пос. мест по адресу: г. Москва, Павелецкая пл., д.1			
Изм.	Кол.уч.	Лист	док.	Подпись	Дата	Технологические решения. Кафе.	Стадия	Лист	Листов
Разработал		Савочкин			15.12.2021		П	2	6
Проверил		Ложкомяев			15.12.2021				
						Схема движения технологических потоков План на отметке +0.000	ООО «Уникальные Технологии»		
Н.контр		Савочкин			15.12.2021				

Согласовано


Инв. № подл. Подп. и дата. Взам. инв. №

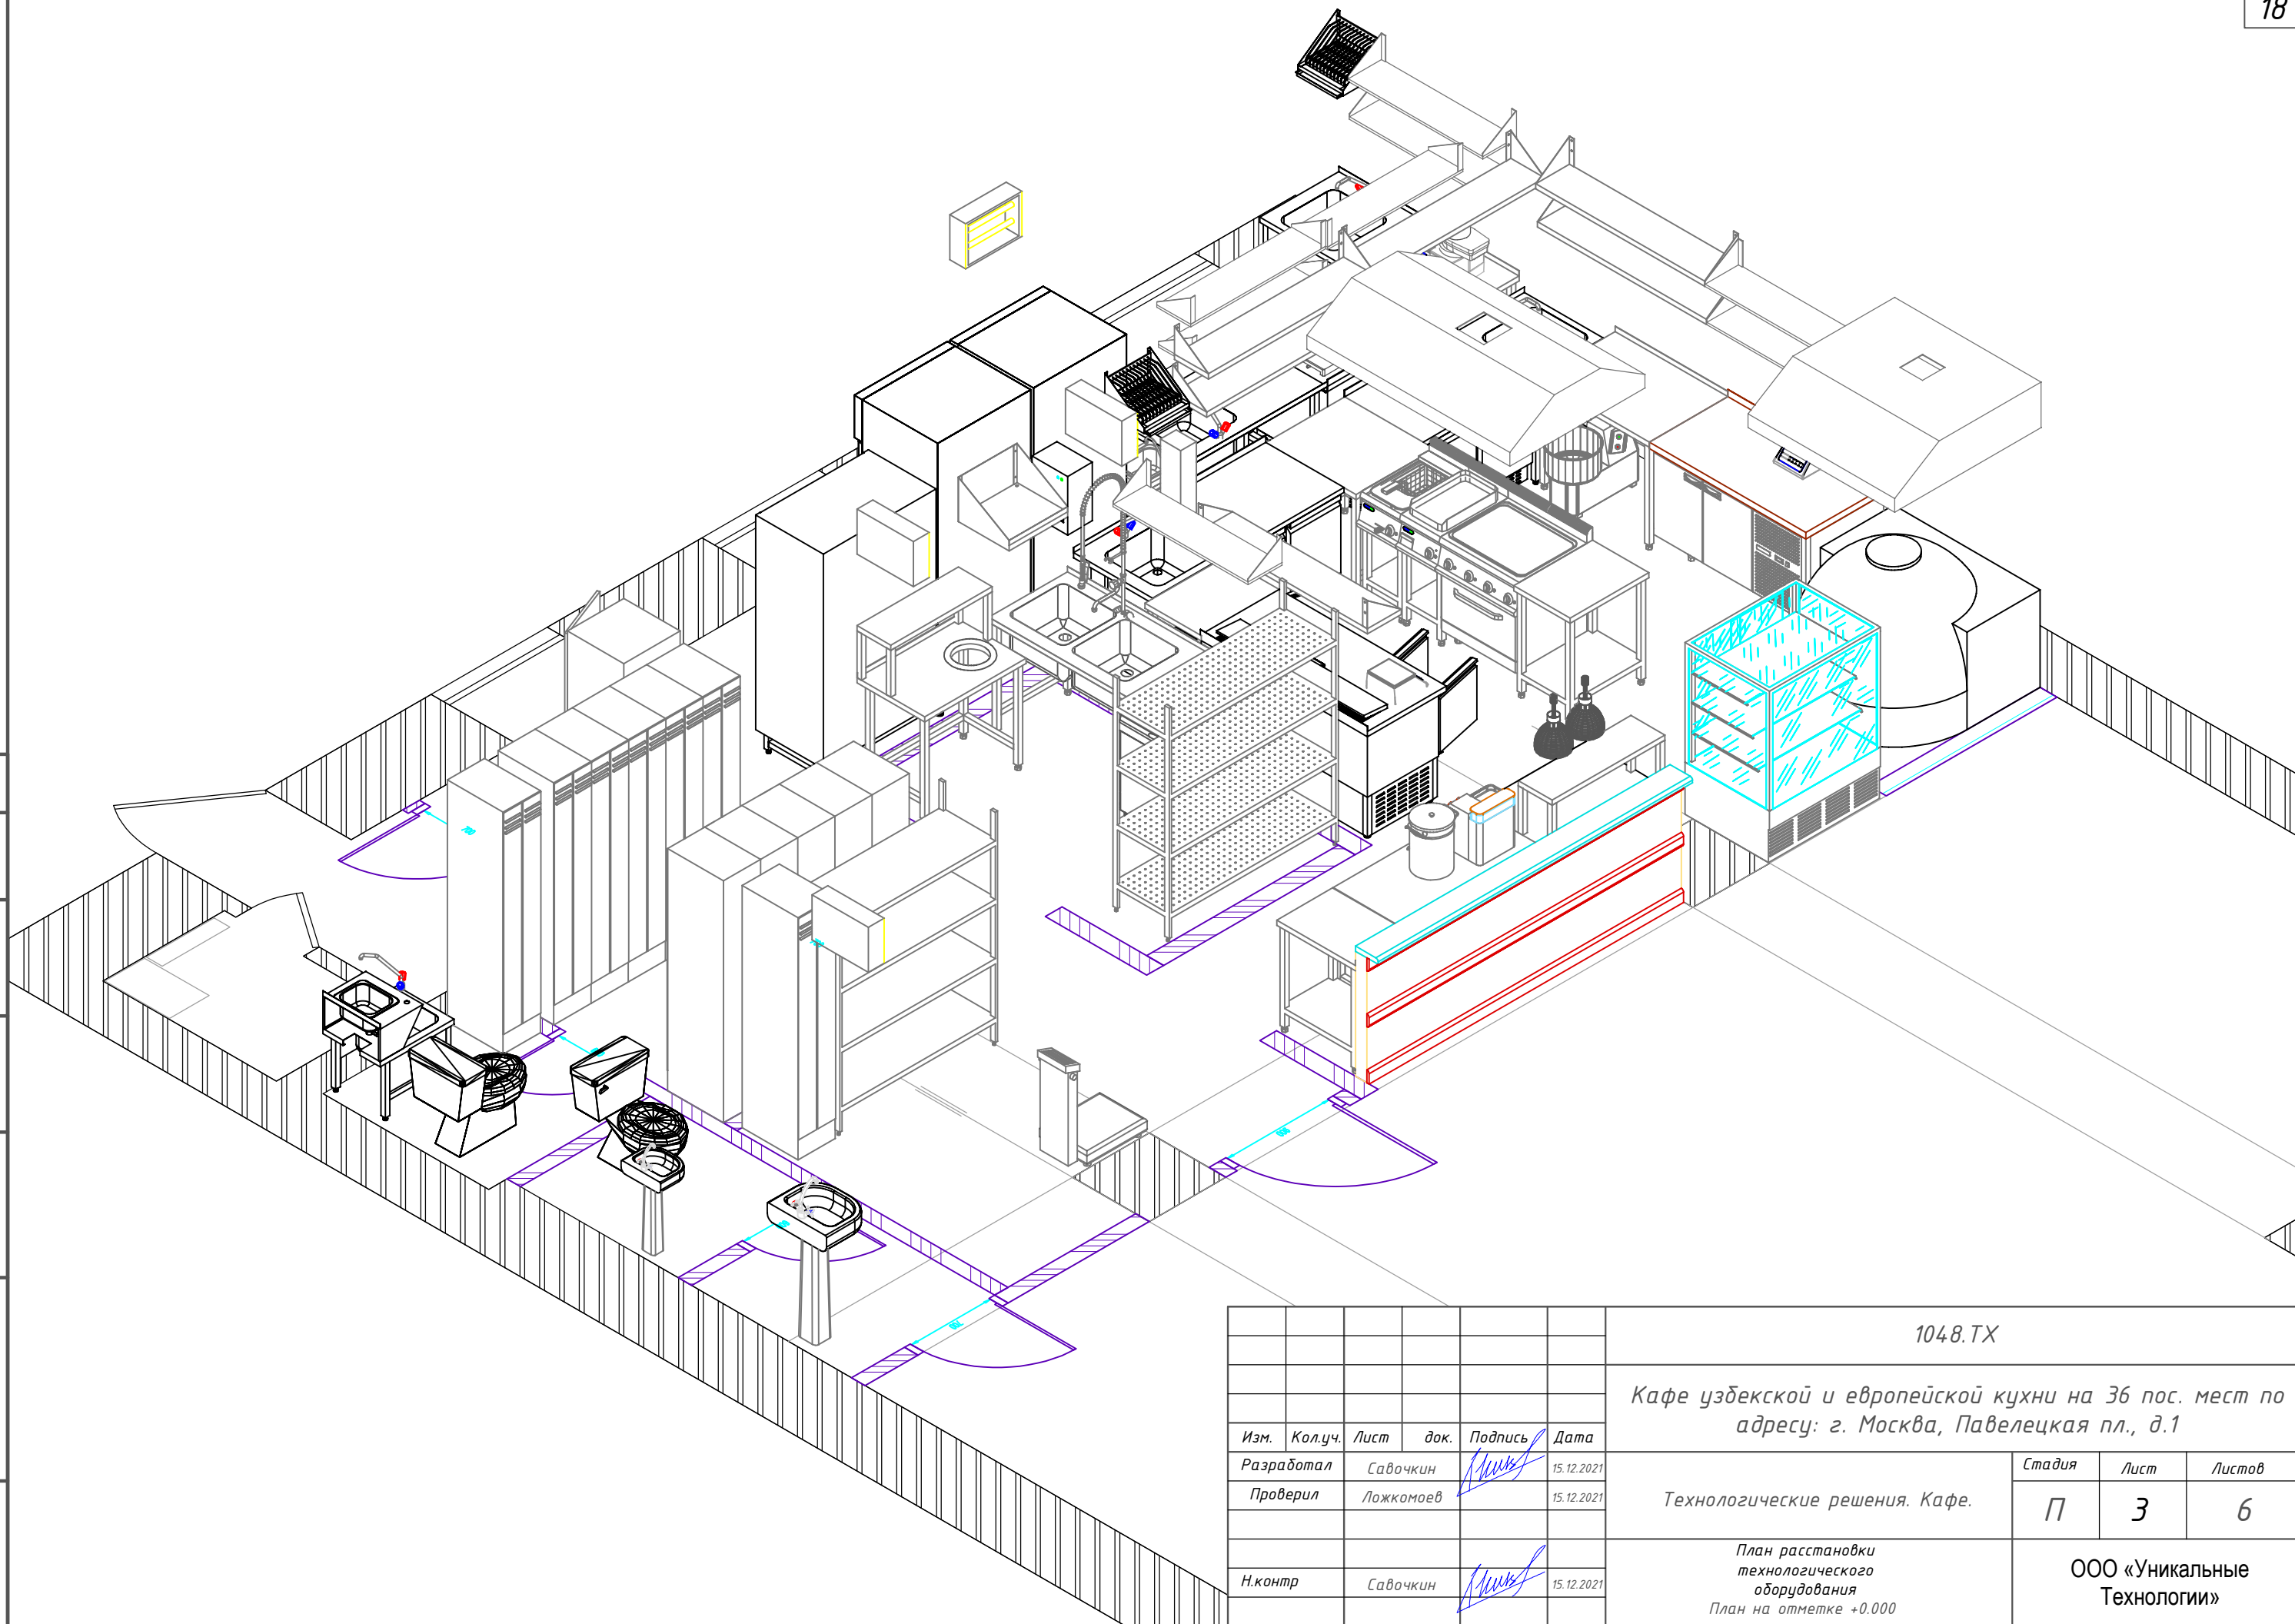


						1048.TX		
						Кафе узбекской и европейской кухни на 36 пос. мест по адресу: г. Москва, Павелецкая пл., д.1		
Изм.	Кол.уч.	Лист	док.	Подпись	Дата	Технологические решения. Кафе.	Стадия	Лист
Разработал		Савочкин			15.12.2021		П	3
Проверил		Ложконоев			15.12.2021			6
						План расстановки технологического оборудования План на отметке +0.000		
Н.контр		Савочкин			15.12.2021	ООО «Уникальные Технологии»		

Согласовано

Инв. № подл. Подп. и дата. Взам. инв. №

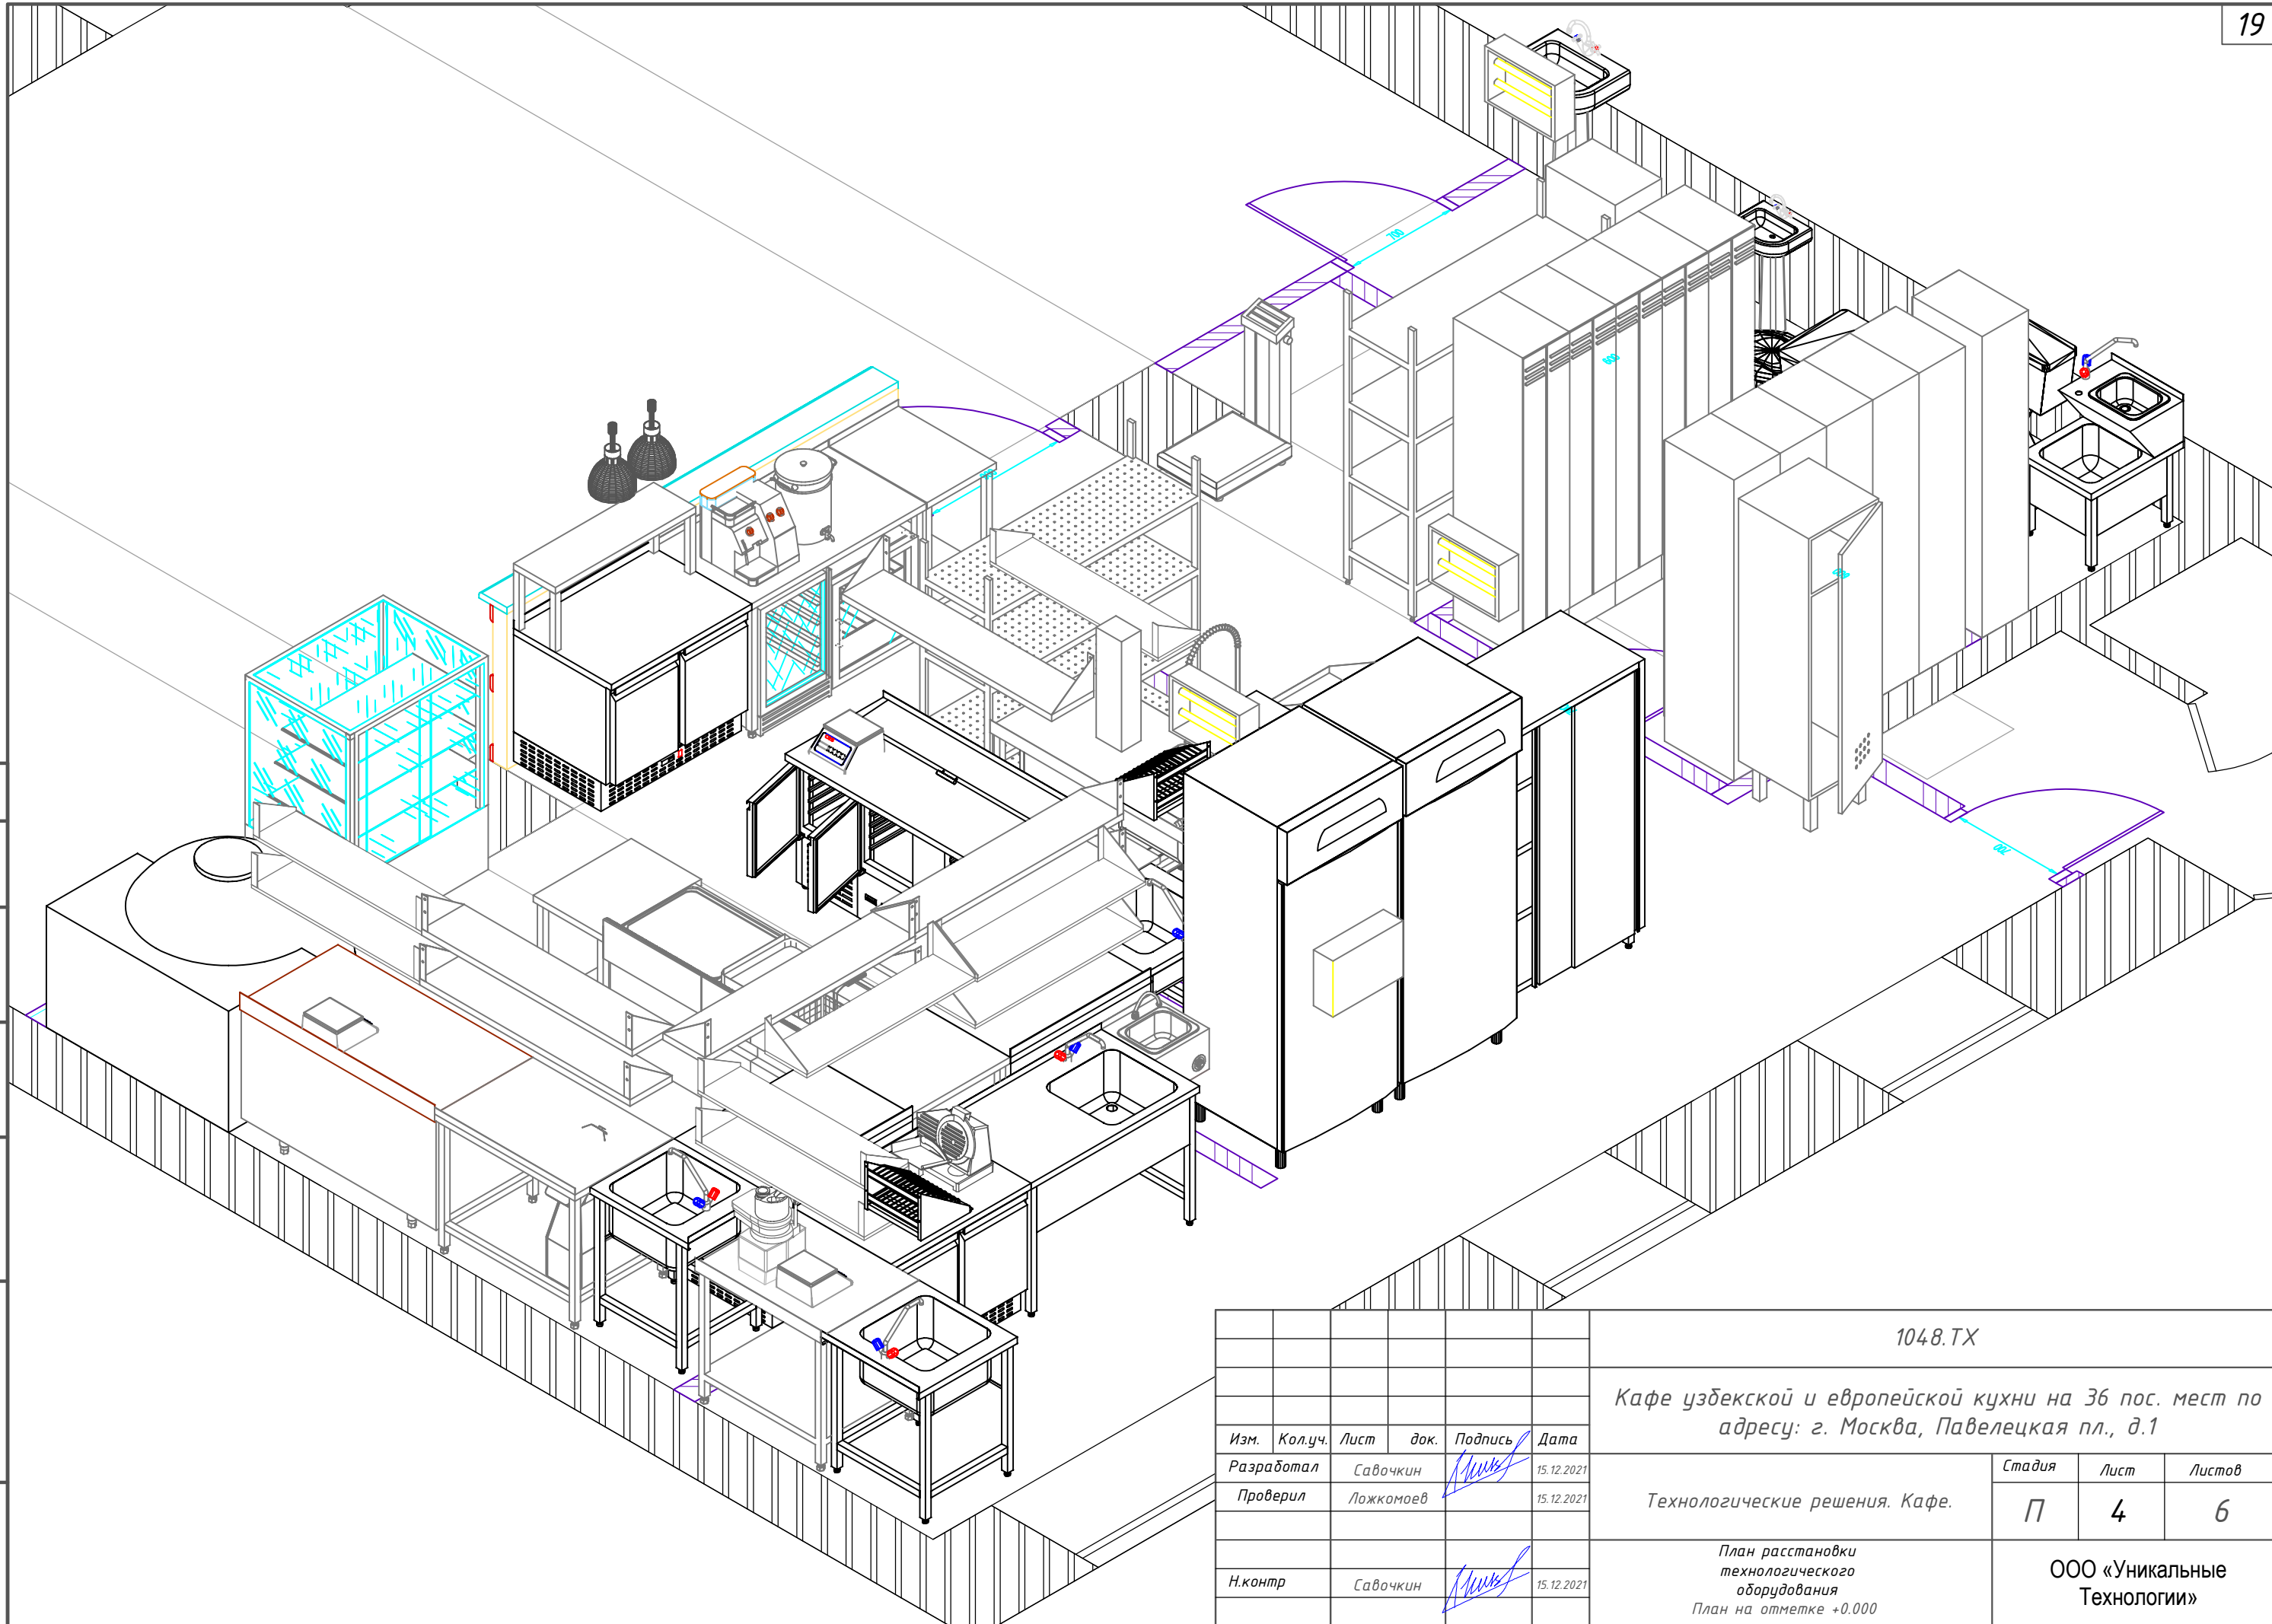


						1048.ТХ			
						Кафе узбекской и европейской кухни на 36 пос. мест по адресу: г. Москва, Павелецкая пл., д.1			
Изм.	Кол.уч.	Лист	док.	Подпись	Дата	Технологические решения. Кафе.	Стадия	Лист	Листов
Разработал		Савочкин			15.12.2021		П	4	6
Проверил		Ложконоев			15.12.2021				
						План расстановки технологического оборудования План на отметке +0.000	ООО «Уникальные Технологии»		
Н.контр		Савочкин			15.12.2021				

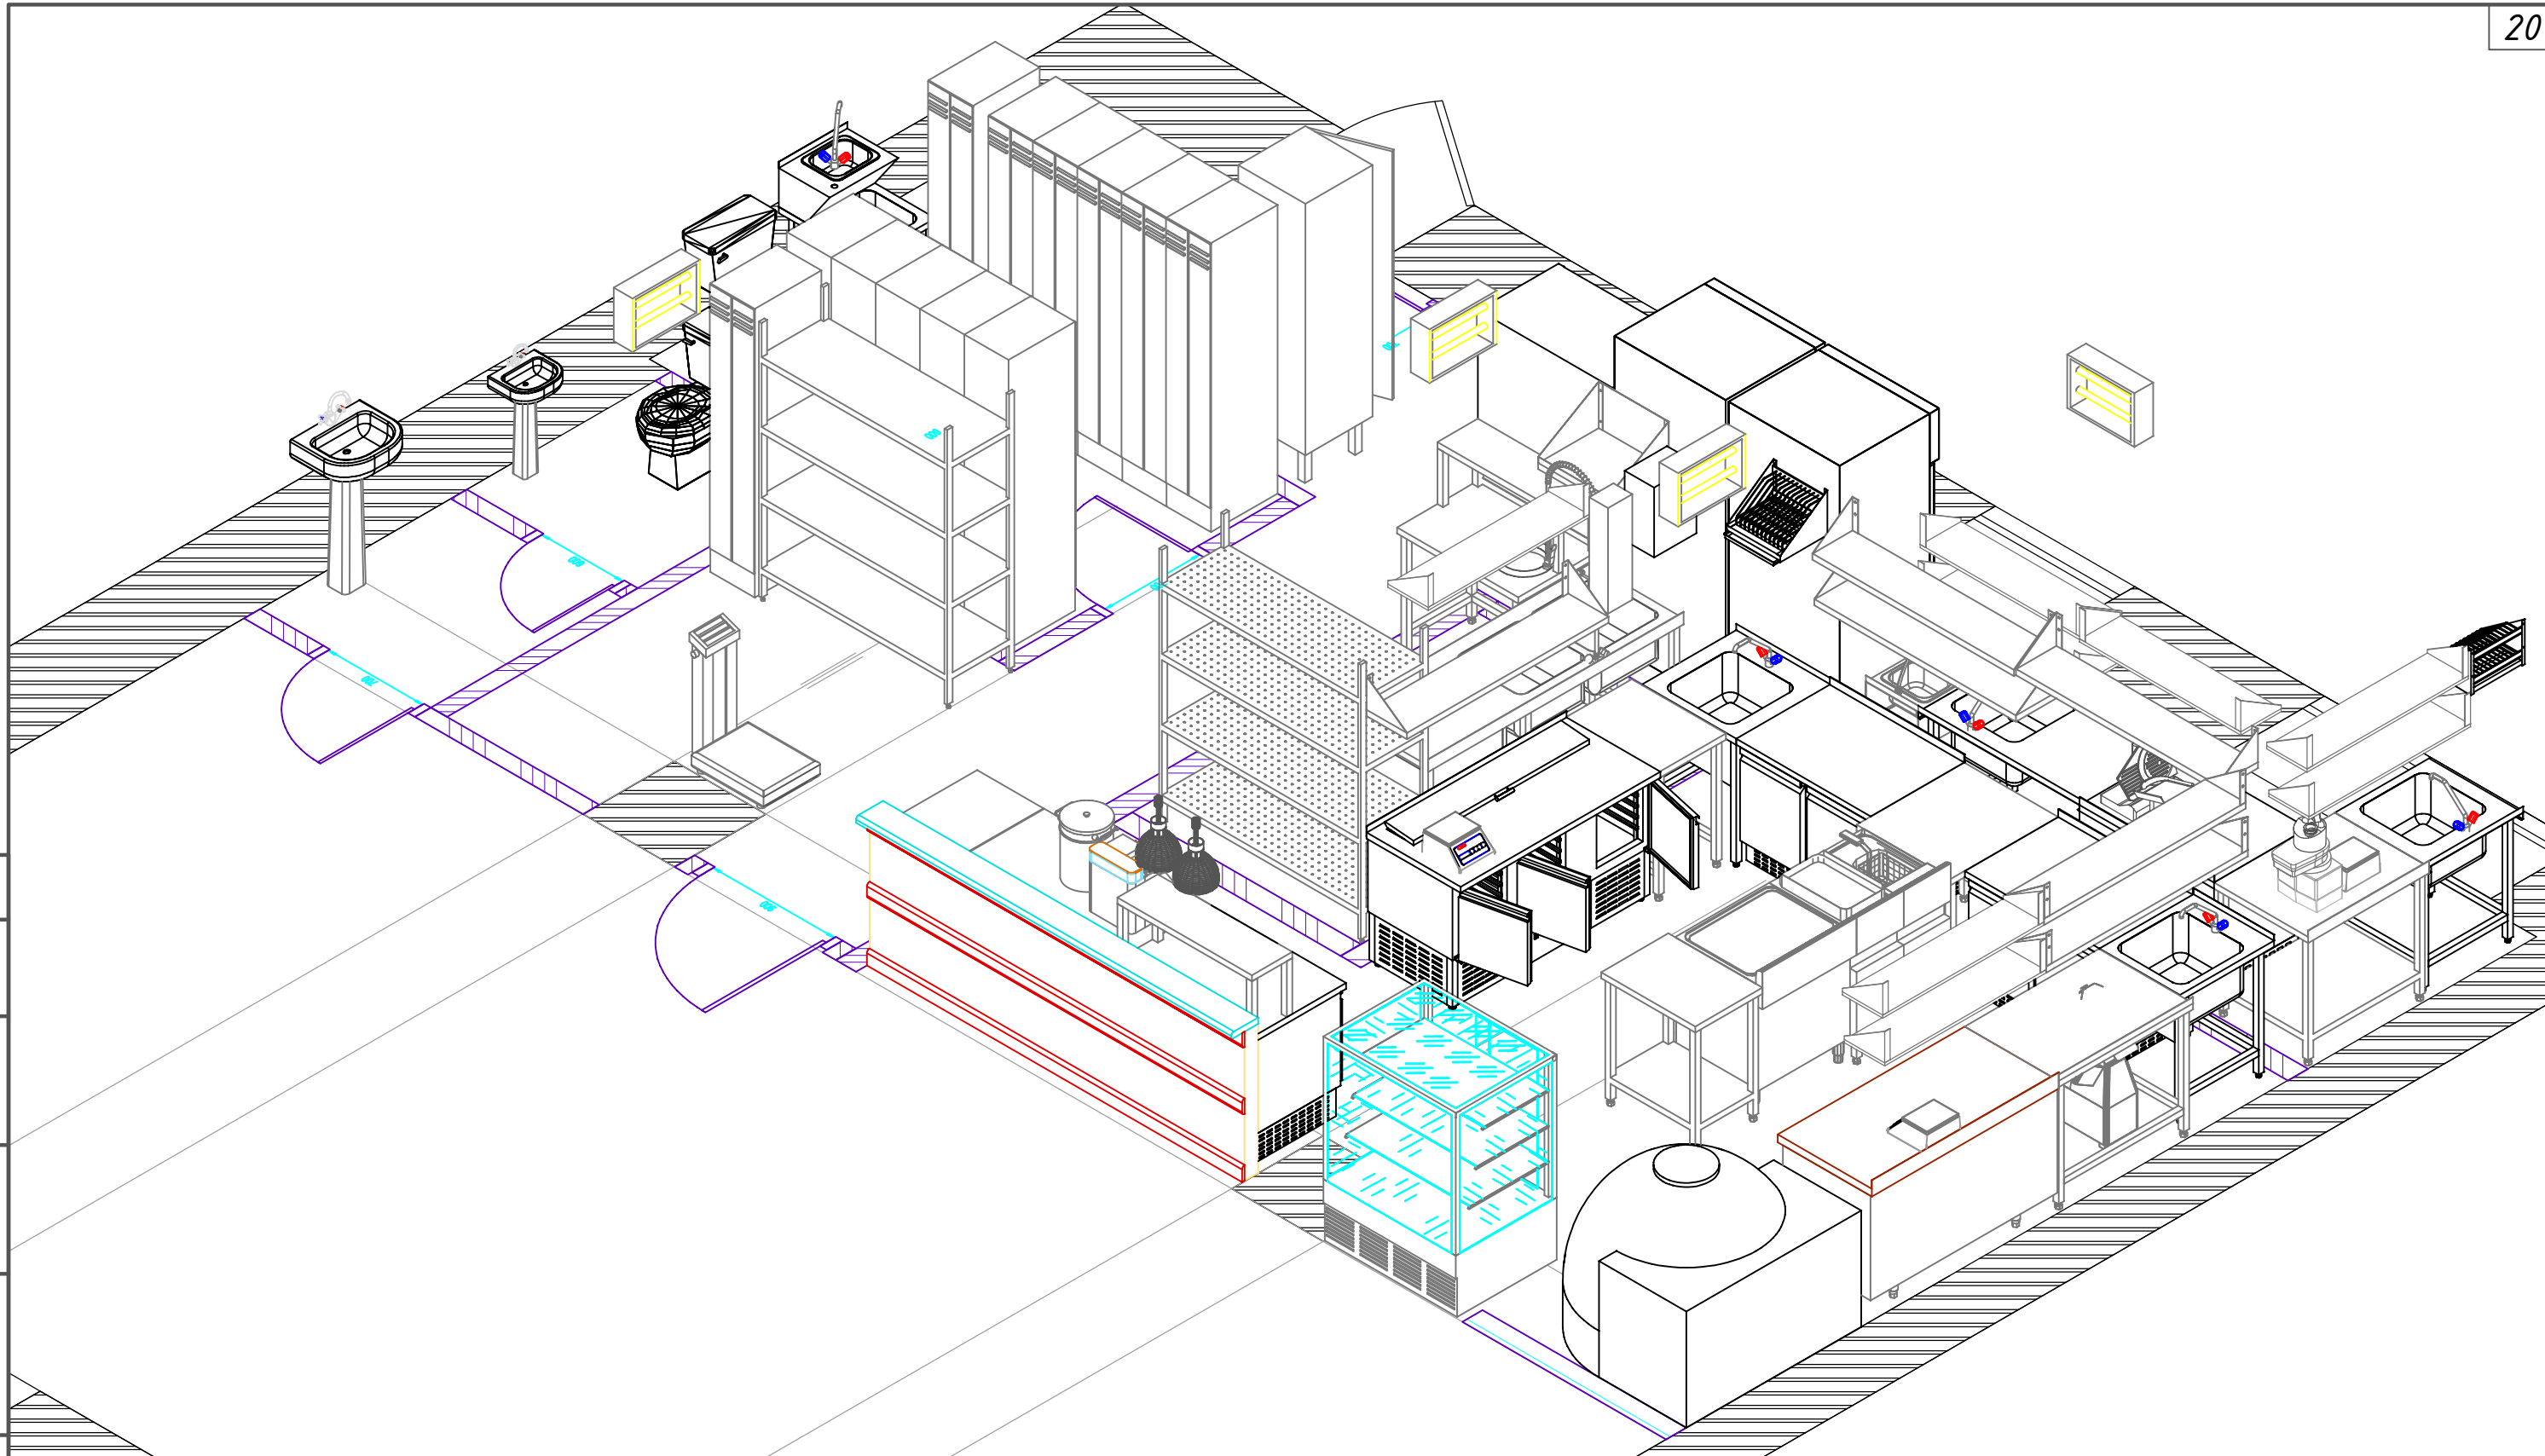

Согласовано		Взам. инв. №	Подп. и дата
Инв. № подл.			

						1048.ТХ			
						Кафе узбекской и европейской кухни на 36 пос. мест по адресу: г. Москва, Павелецкая пл., д.1			
Изм.	Кол.уч.	Лист	док.	Подпись	Дата	Технологические решения. Кафе.	Стадия	Лист	Листов
Разработал		Савочкин			15.12.2021		П	5	6
Проверил		Ложкомоев			15.12.2021	План расстановки технологического оборудования План на отметке +0.000	ООО «Уникальные Технологии»		
Н.контр		Савочкин			15.12.2021				

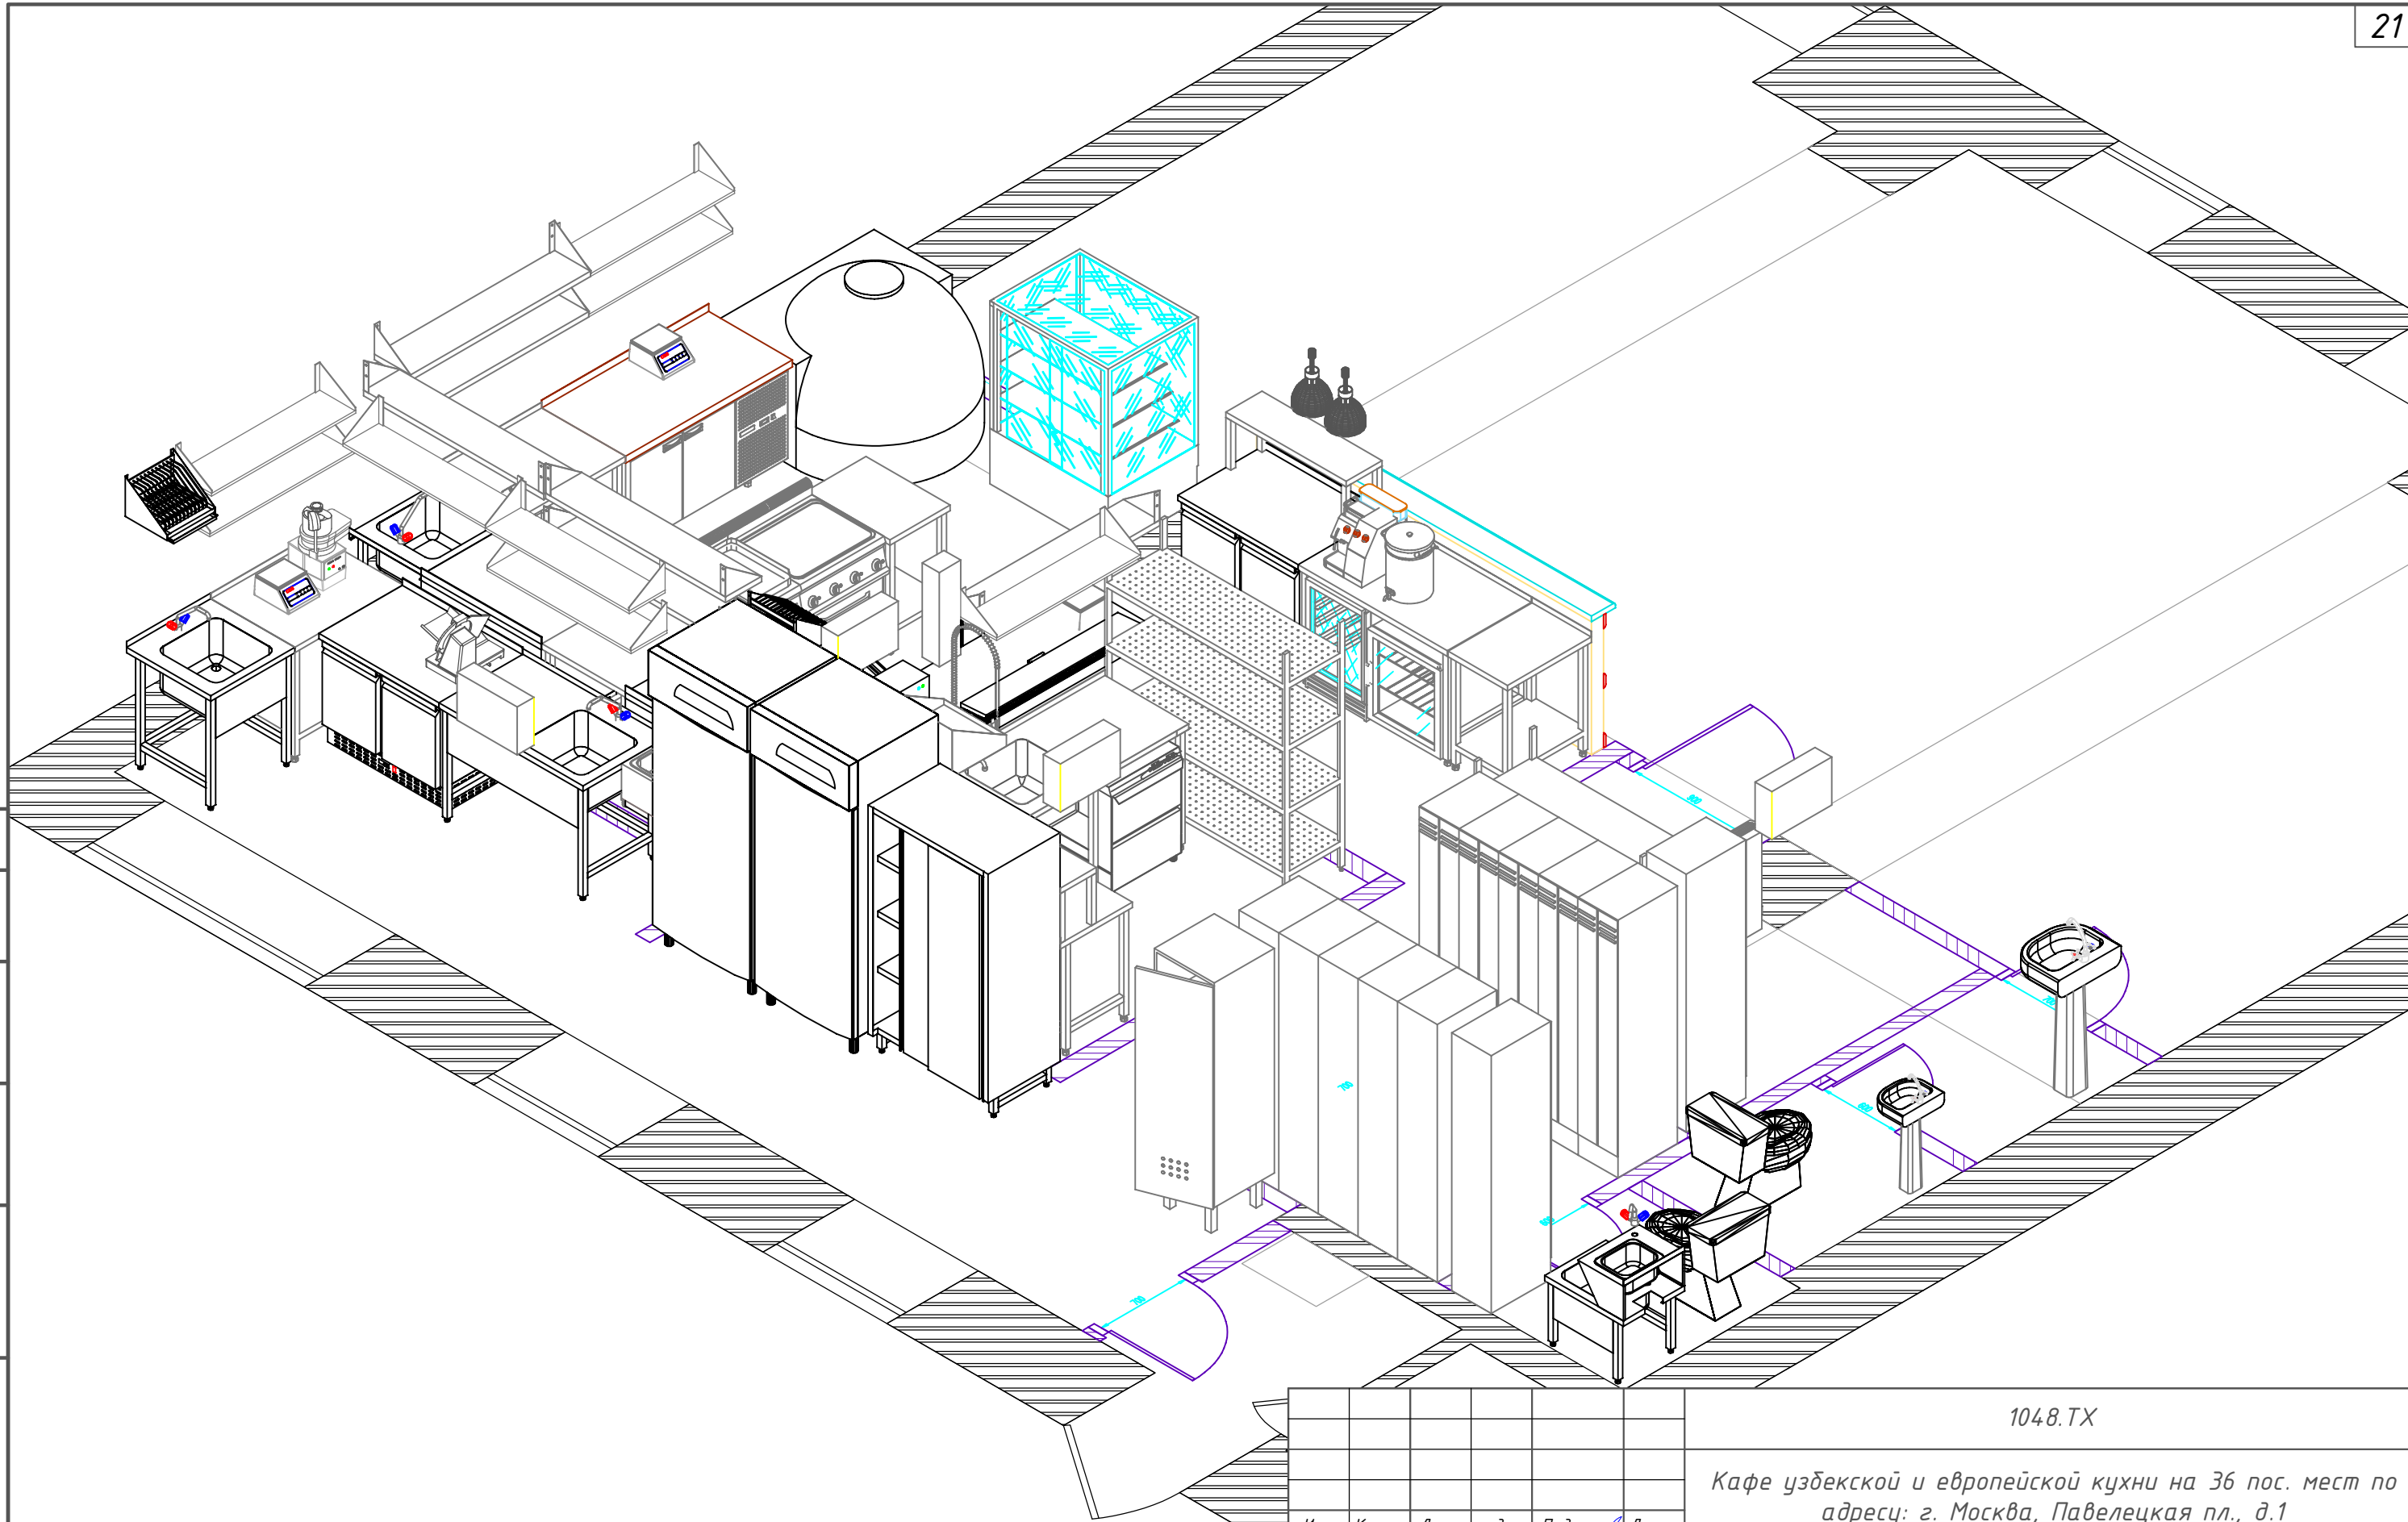

Согласовано		Взам. инв. №		Подп. и дата		Инв. № подл.	

						1048.ТХ		
						Кафе узбекской и европейской кухни на 36 пос. мест по адресу: г. Москва, Павелецкая пл., д.1		
Изм.	Кол.уч.	Лист	док.	Подпись	Дата	Технологические решения. Кафе.	Стадия	Лист
Разработал		Савочкин			15.12.2021		П	6
Проверил		Ложконоев			15.12.2021	План расстановки технологического оборудования План на отметке +0.000	ООО «Уникальные Технологии»	
Н.контр		Савочкин			15.12.2021			

**ВЫПИСКА
ИЗ РЕЕСТРА ЧЛЕНОВ САМОРЕГУЛИРУЕМОЙ ОРГАНИЗАЦИИ**

03.06.2020г.

(дата)

259-В/20

(номер)

**Саморегулируемая организация - Союз «Межрегиональное объединение архитектурно-проектных предприятий малого и среднего предпринимательства-ОПОРА»
СРО «ОПОРА»**

(полное и сокращенное наименование саморегулируемой организации)

**Саморегулируемая организация, основанная на членстве лиц, осуществляющих
подготовку проектной документации**

(вид саморегулируемой организации)

**141100, Московская обл., г. Щёлково, пл. Ленина, д.5, комната 501/1, www.moapp.ru,
moapp@mail.ru**

(адрес места нахождения саморегулируемой организации, адрес официального сайта в информационно-телекоммуникационной сети «Интернет», адрес электронной почты)

СРО-П-147-09032010

(регистрационный номер записи в государственном реестре саморегулируемых организаций)

выдана: Общество с ограниченной ответственностью «Уникальные Технологии»

(фамилия, имя, (в случае если имеется) отчество заявителя – физического лица или полное наименование
заявителя - юридического лица)

Наименование	Сведения
1. Сведения о члене саморегулируемой организации:	
1.1. Полное и (в случае, если имеется) сокращенное наименование юридического лица или фамилия, имя, (в случае, если имеется) отчество индивидуального предпринимателя	Общество с ограниченной ответственностью «Уникальные Технологии» ООО «Уникальные Технологии»
1.2. Идентификационный номер налогоплательщика (ИНН)	7710527771
1.3. Основной государственный регистрационный номер (ОГРН) или основной государственный регистрационный номер индивидуального предпринимателя (ОГРНИП)	1047796064645
1.4. Адрес места нахождения юридического лица	121596, г. Москва, ул. Горбунова, д. 2, строение 204, этаж 3, помещение II, комната 48
1.5. Место фактического осуществления деятельности (только для индивидуального предпринимателя)	
2. Сведения о членстве индивидуального предпринимателя или юридического лица в саморегулируемой организации:	
2.1. Регистрационный номер члена в реестре членов саморегулируемой организации	№ 368
2.2. Дата регистрации юридического лица или индивидуального предпринимателя в реестре членов саморегулируемой организации (число, месяц, год)	10.07.2019г.
2.3. Дата (число, месяц, год) и номер решения о приеме в члены саморегулируемой организации	Протокол № 35-ЗС/19 от 10.07.2019г.
2.4. Дата вступления в силу решения о приеме в члены саморегулируемой организации (число, месяц, год)	10.07.2019г.
2.5. Дата прекращения членства в саморегулируемой организации (число, месяц, год)	
2.6. Основания прекращения членства в саморегулируемой организации	

3. Сведения о наличии у члена саморегулируемой организации права выполнения работ:

3.1. Дата, с которой член саморегулируемой организации имеет право выполнять инженерные изыскания, осуществлять подготовку проектной документации, строительство, реконструкцию, капитальный ремонт, снос объектов капитального строительства по договору подряда на выполнение инженерных изысканий, подготовку проектной документации, по договору строительного подряда, по договору подряда на осуществление сноса (нужное выделить):

в отношении объектов капитального строительства (кроме особо опасных, технически сложных и уникальных объектов, объектов использования атомной энергии)	в отношении особо опасных, технически сложных и уникальных объектов капитального строительства (кроме объектов использования атомной энергии)	в отношении объектов использования атомной энергии
10.07.2019г.	Указывается число, месяц, год возникновения права	Указывается число, месяц, год возникновения права

3.2. Сведения об уровне ответственности члена саморегулируемой организации по обязательствам по договору подряда на выполнение инженерных изысканий, подготовку проектной документации, по договору строительного подряда, по договору подряда на осуществление сноса, и стоимости работ по одному договору, в соответствии с которым указанным членом внесен взнос в компенсационный фонд возмещения вреда (нужное выделить):

а) первый	V	Не превышает 25 миллионов рублей указывается стоимость работ по одному договору в рублях
б) второй		указывается стоимость работ по одному договору в рублях
в) третий		указывается стоимость работ по одному договору в рублях
г) четвертый		указывается стоимость работ по одному договору в рублях
д) пятый*		указывается стоимость работ по одному договору в рублях
е) простой*		в случае если член саморегулируемой организации осуществляет только снос объекта капитального строительства, не связанный со строительством, реконструкцией объекта капитального строительства

*заполняется только для членов саморегулируемых организаций, основанных на членстве лиц, осуществляющих строительство

3.3. Сведения об уровне ответственности члена саморегулируемой организации по обязательствам по договору подряда на выполнение инженерных изысканий, подготовку проектной документации, по договору строительного подряда, по договору подряда на осуществление сноса, заключенным с использованием конкурентных способов заключения договоров, и предельному размеру обязательств по таким договорам, в соответствии с которым указанным членом внесен взнос в компенсационный фонд обеспечения договорных обязательств (нужное выделить):

а) первый	V	Не превышает 25 миллионов рублей указывается предельный размер обязательств по договорам в рублях
б) второй		указывается предельный размер обязательств по договорам в рублях
в) третий		указывается предельный размер обязательств по договорам в рублях
г) четвертый		указывается предельный размер обязательств по договорам в рублях
д) пятый*		указывается предельный размер обязательств по договорам в рублях

*заполняется только для членов саморегулируемых организаций, основанных на членстве лиц, осуществляющих строительство

4. Сведения о приостановлении права выполнять инженерные изыскания, осуществлять подготовку проектной документации, строительство, реконструкцию, капитальный ремонт, снос объектов капитального строительства:

4.1. Дата, с которой приостановлено право выполнения работ (число, месяц, год)	
4.2. Срок, на который приостановлено право выполнения работ*	

*указываются сведения только в отношении действующей меры дисциплинарного воздействия

Директор СРО «ОПОРА»
(должность уполномоченного лица)

М.П.

(подпись)

А.А. Новохатский
(инициалы, фамилия)