


Согласовано

Взам. инв. №
Подп. и дата
Инв. № подл.

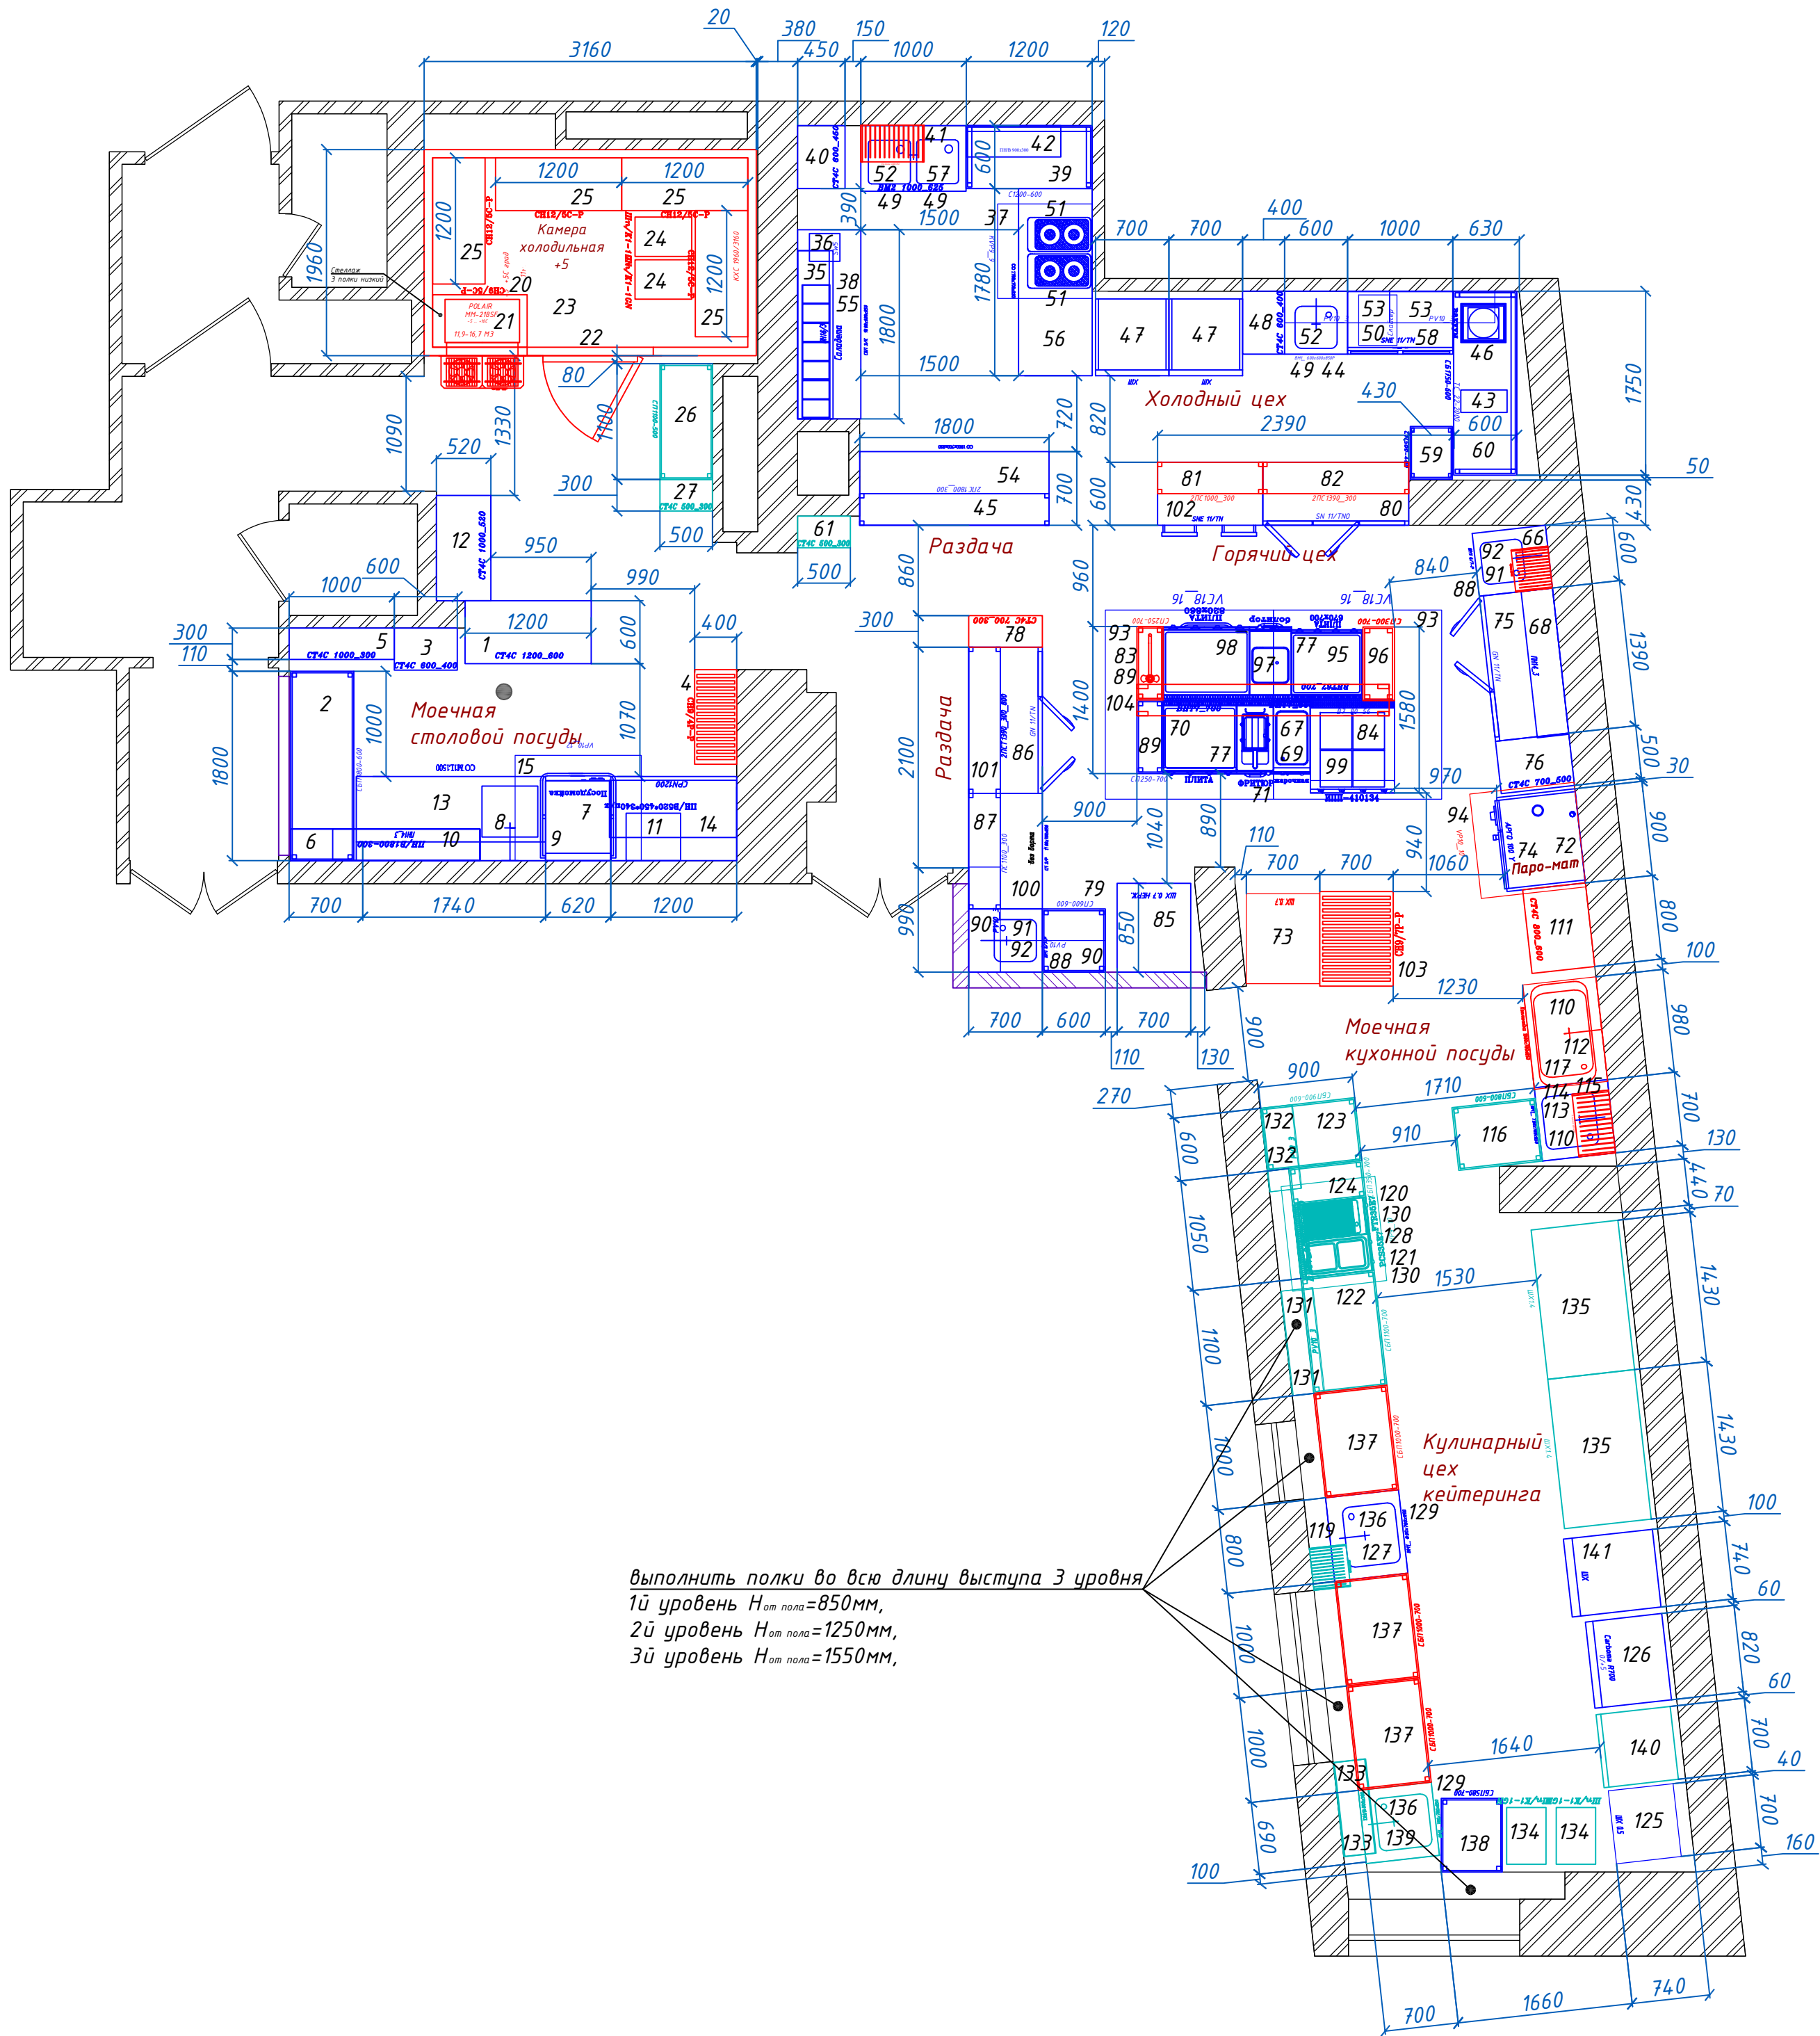

Условные цветовые обозначения
оборудования

- существующее об-е на объекте
- об-е из кулинарного цеха
- новое об-е

выполнить полки во всю длину выступа 3 уровня
1й уровень $H_{от\ пола}=850\text{мм}$,
2й уровень $H_{от\ пола}=1250\text{мм}$,
3й уровень $H_{от\ пола}=1550\text{мм}$,


Масштаб 1:50

						1049.TX			
						Перепланировка произв. зоны ресторана по адресу: г.Москва, Ботанический пер., д.5			
Изм.	Кол.уч.	Лист	док.	Подпись	Дата	Технологическая часть проекта. Технология предприятия питания.	Стадия	Лист	Листов
Рук.пр-та.	Секацкий				31.01.2022		Р		5
Технолог	Савочкин				31.01.2022				
						План расстановки технологического оборудования План на отметке +0.000			
Заказчик									

Согласовано

З – подвод электроэнергии
Ф – фазность тока
Р – однофазная розетка с заземлением
ШР – штепсельная розетка с рабочим нулем и заземлением
h – высота подводов от чистого пола в мм
L – длина свободного провода в мм
380В / 220В – напряжение в сети
* – условное значение предполагаемого оборудования, перед подключением обязательно смотреть паспорт производителя

- Прокладка электросетей должна осуществляться в плоскости стен и пола, согласно требованиям ПУЭ по трёх или пятипроводной схеме, в зависимости от подключаемого технологического оборудования
- В случае подключения оборудования путём ввода кабеля напрямую, без установки разъёма, необходим выход МЯГКОГО (МНОГОЖИЛЬНОГО) кабеля, длиной 2500мм, согласно заданным высотам
- Установленные силовые разъёмы необходимо укомплектовать ответной частью.

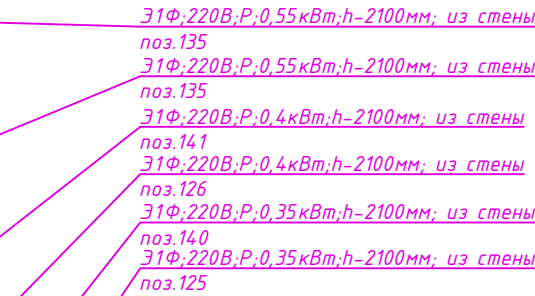


Формат	A2
--------	----

Согласовано


Инв. № подл. Подп. и дата Взам. инв. №

Примечания

- В местах крепления зонтов необходимо обеспечить достаточную несущую способность поверхностей. Подготовить подвесы в точках крепления /шпилька М8 или цепь/ на высоте 2100 мм от пола.
- Отверстия в зонах под крепеж сверлятся по месту
- Вытяжной зонт крепиться на высоте 2000 мм от пола /по нижнему срезу зонта/
- Отверстия в вытяжных зонах для врезки фланцев выполняются по месту /при подключении/
- В помещении предназначенном под установку холодильных камер с моноблоками или сплит-системами необходимо обеспечить приточно-вытяжную вентиляцию (температура окружающей среды от +5 до +25 градусов Цельсия, влажность воздуха не выше 80%)
- Отопительные приборы, в помещениях предназначенных под установку холодильных камер, следует размещать на расстоянии не менее 1500 мм от стен камер

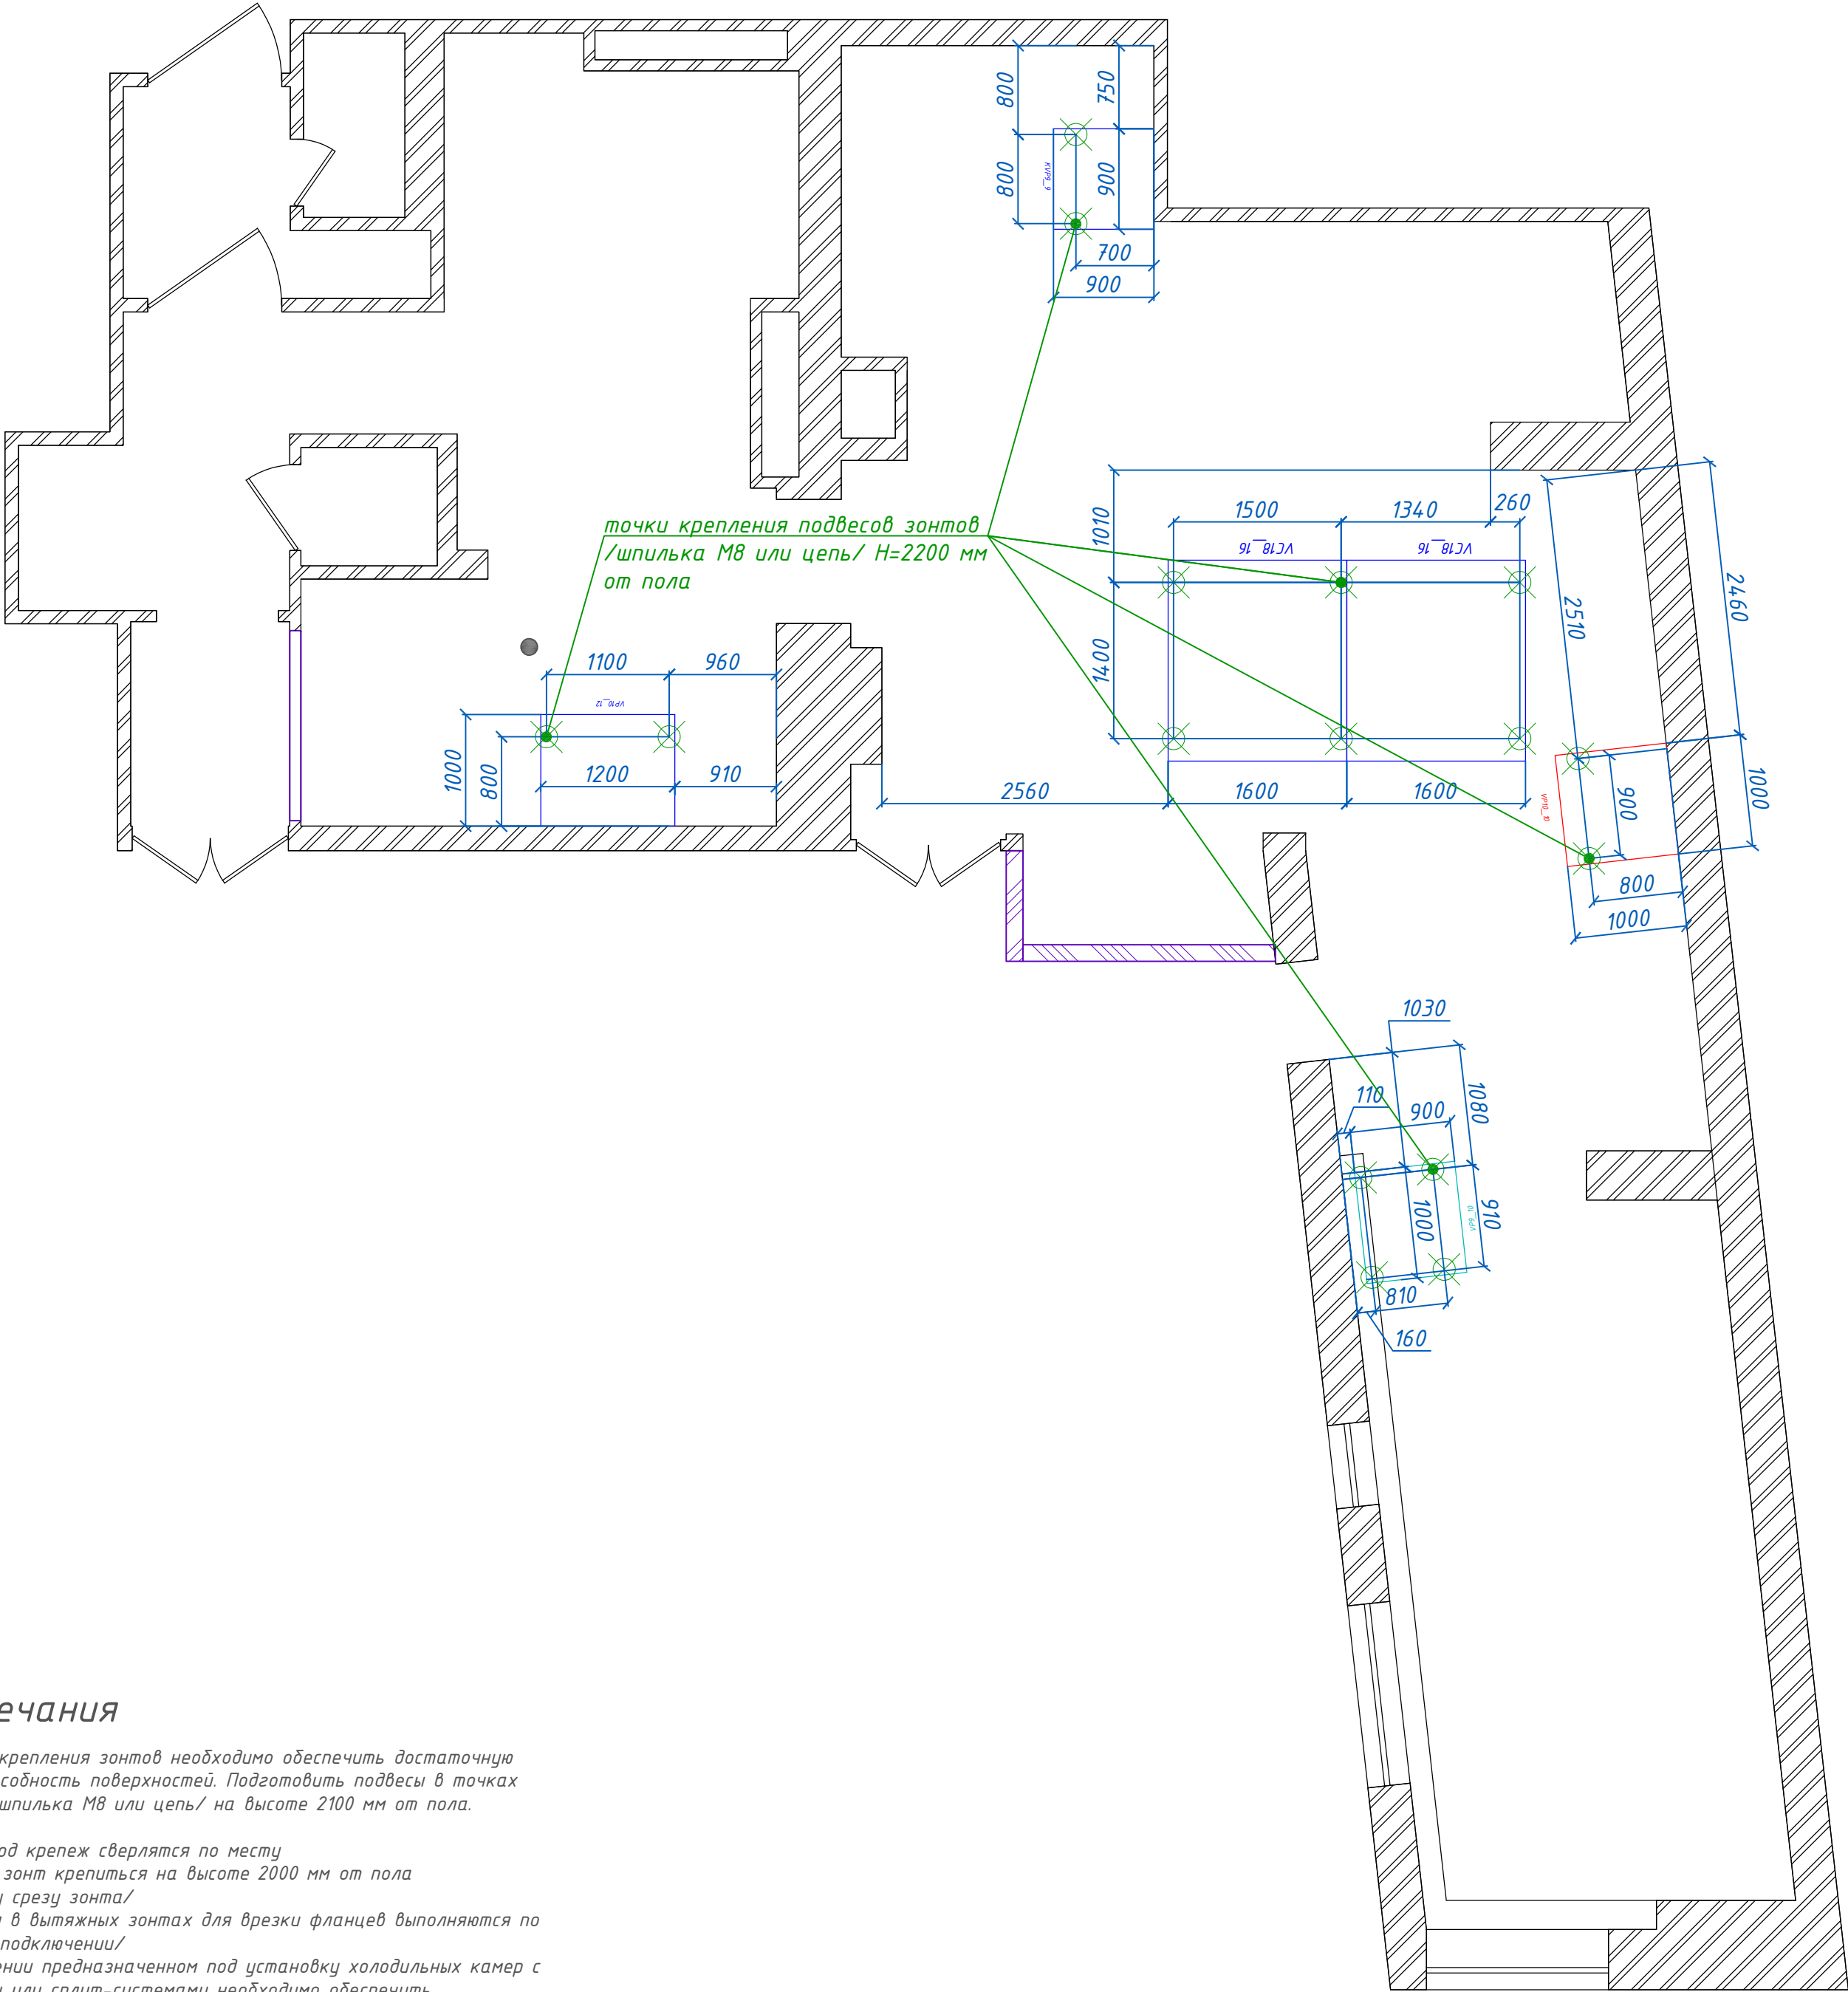

						1049.TX			
						Перепланировка произв. зоны ресторана по адресу: г.Москва, Ботанический пер., д.5			
Изм.	Кол.уч.	Лист	док.	Подпись	Дата	Технологическая часть проекта. Технология предприятия питания.	Стадия	Лист	Листов
Рук.пр-та.		Секацкий			31.01.2022		Р		5
Технолог		Савочкин			31.01.2022	План расположения вентиляционных зонтов План на отметке +0,000			
Заказчик									

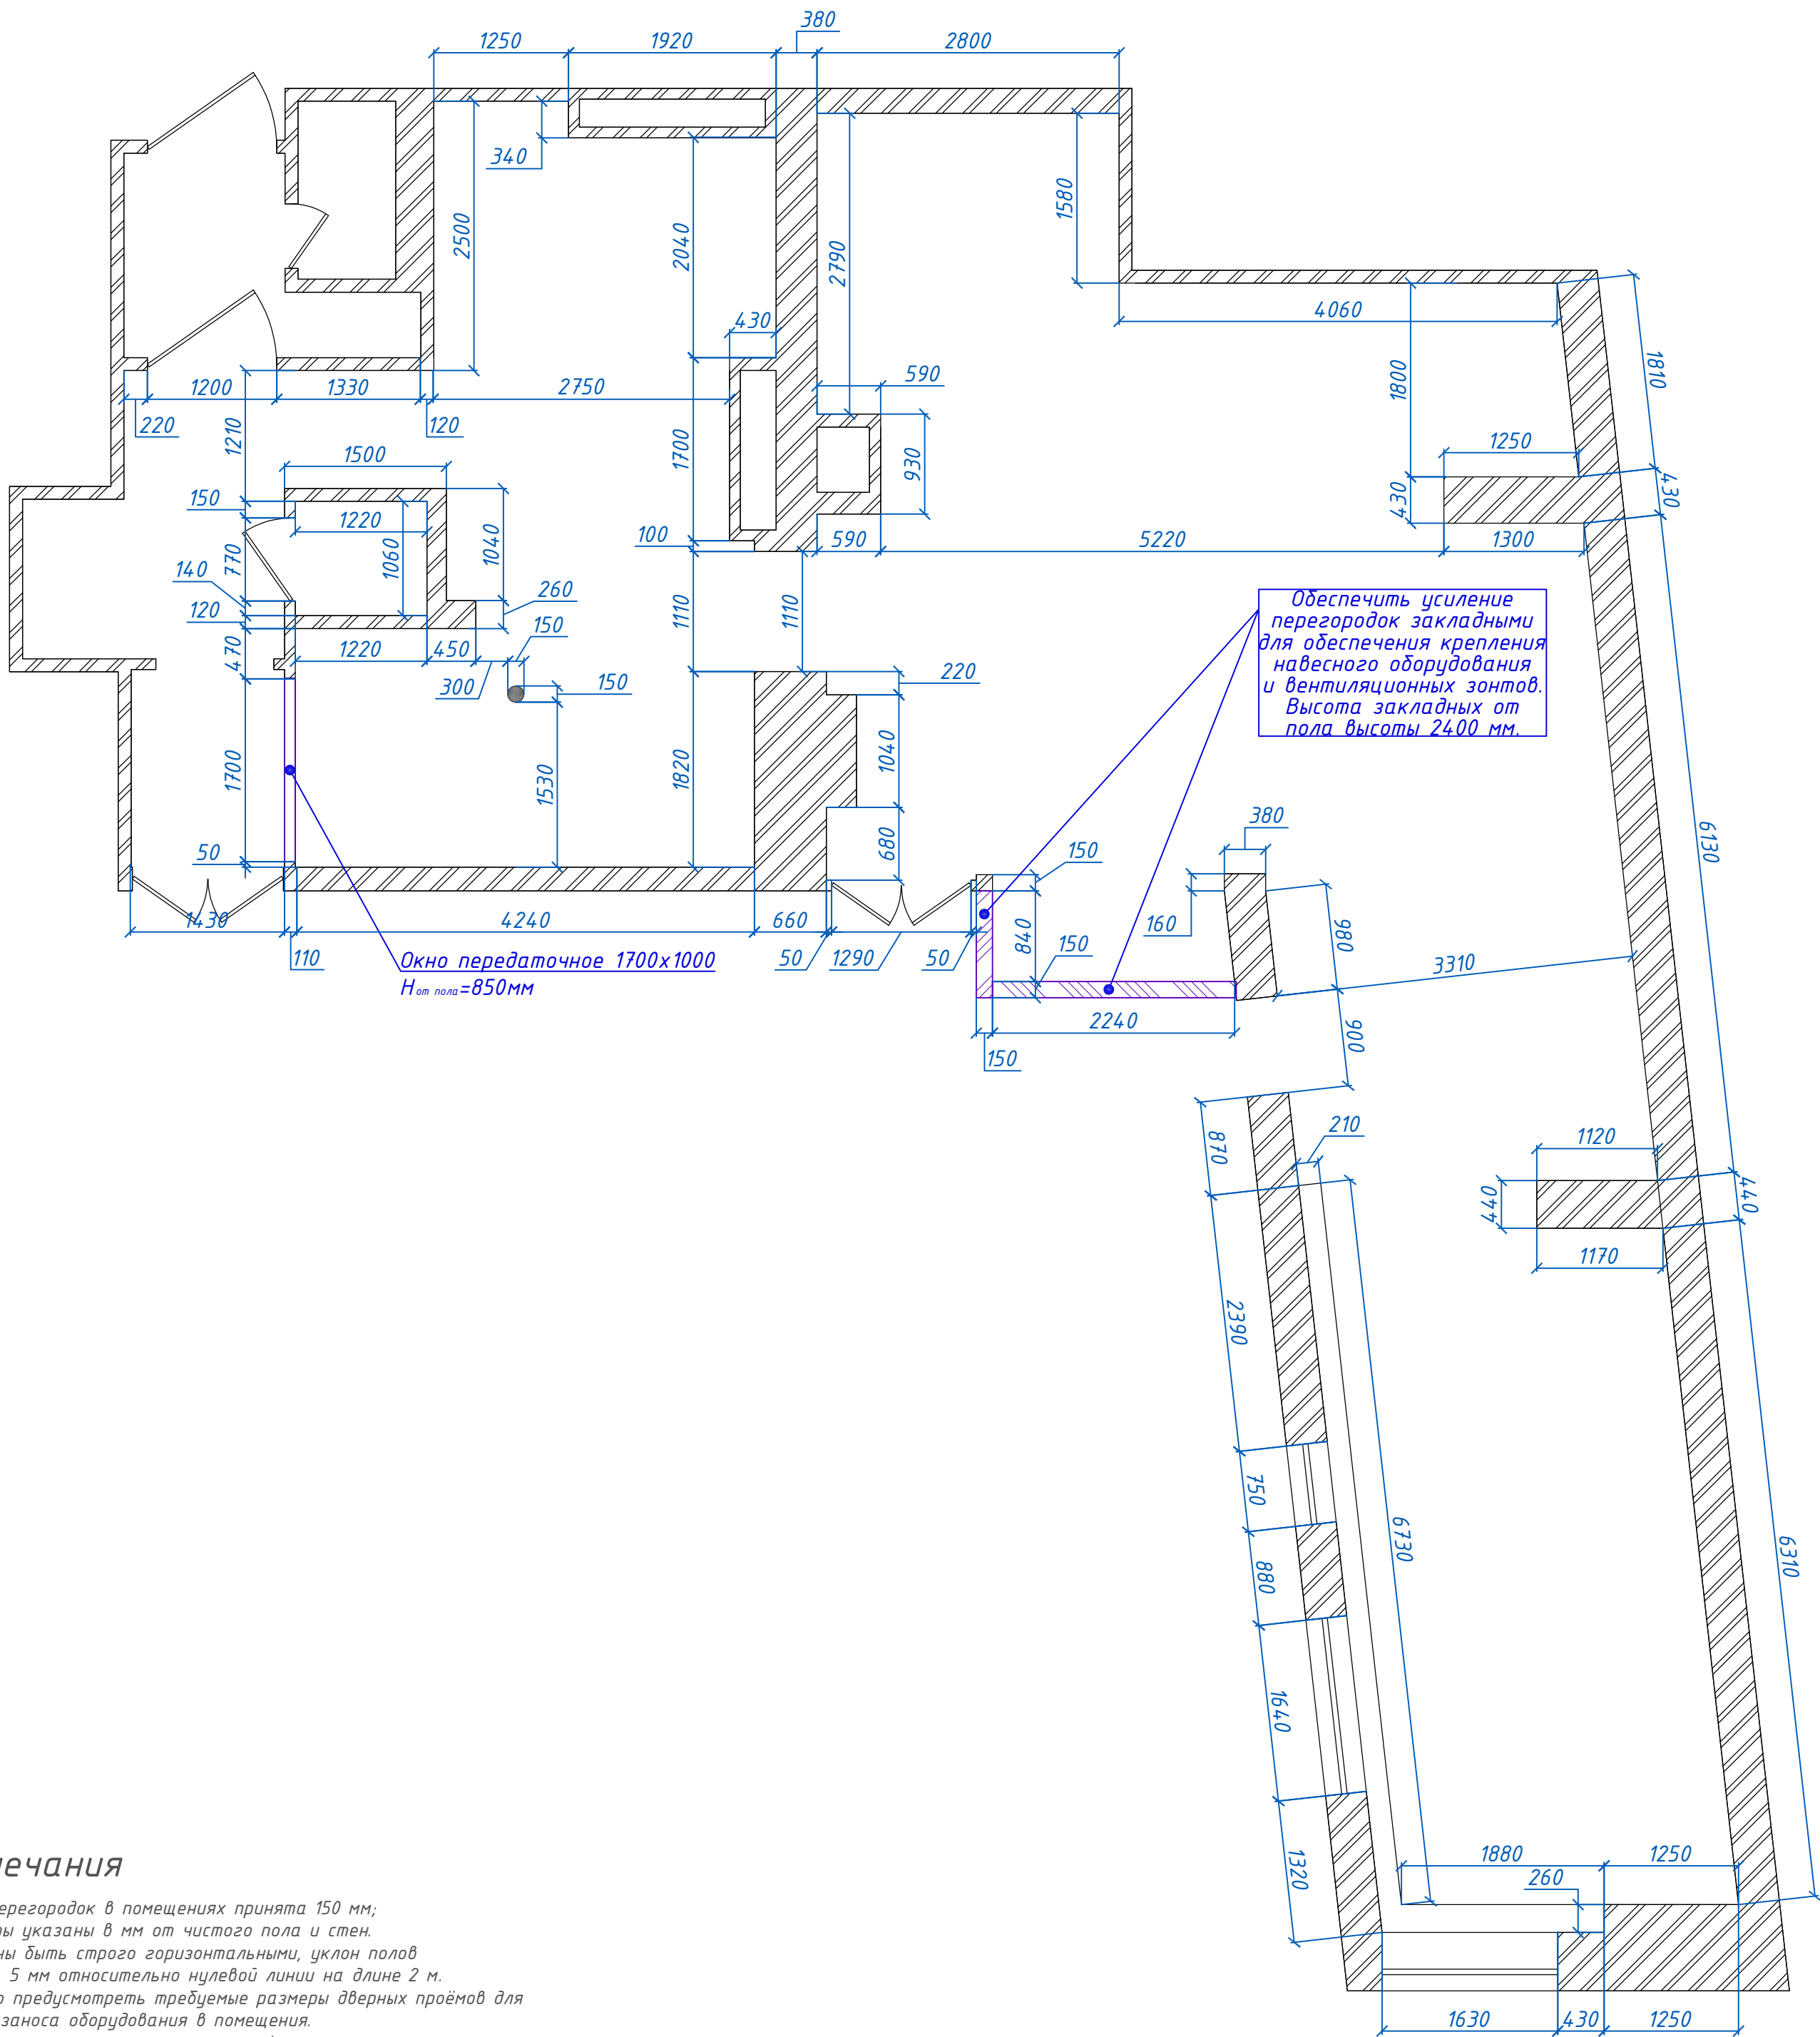

Примечания

- Толщина перегородок в помещениях принята 150 мм;
- Все размеры указаны в мм от чистого пола и стен.
- полы должны быть строго горизонтальными, уклон полов не более +/- 5 мм относительно нулевой линии на длине 2 м.
- Необходимо предусмотреть требуемые размеры дверных проёмов для обеспечения заноса оборудования в помещения.
- Для установки навесного оборудования (полок, панелей, пристенных и центральных вентиляционных зонтов) требуется предусмотреть закладные элементы, обеспечивающие надёжное крепление вышеуказанного оборудования.

						1049.TX			
						Перепланировка произв. зоны ресторана по адресу: г.Москва, Ботанический пер., д.5			
Изм.	Кол.уч.	Лист	док.	Подпись	Дата	Технологическая часть проекта. Технология предприятия питания.	Стадия	Лист	Листов
Рук.пр-та.	Секацкий				31.01.2022		Р		5
Технолог	Савочкин				31.01.2022				
						План расположения перегородок			
Заказчик						План на отметке +0.000			