


Согласовано

Инв. № подл. Подп. и дата Взам. инв. №

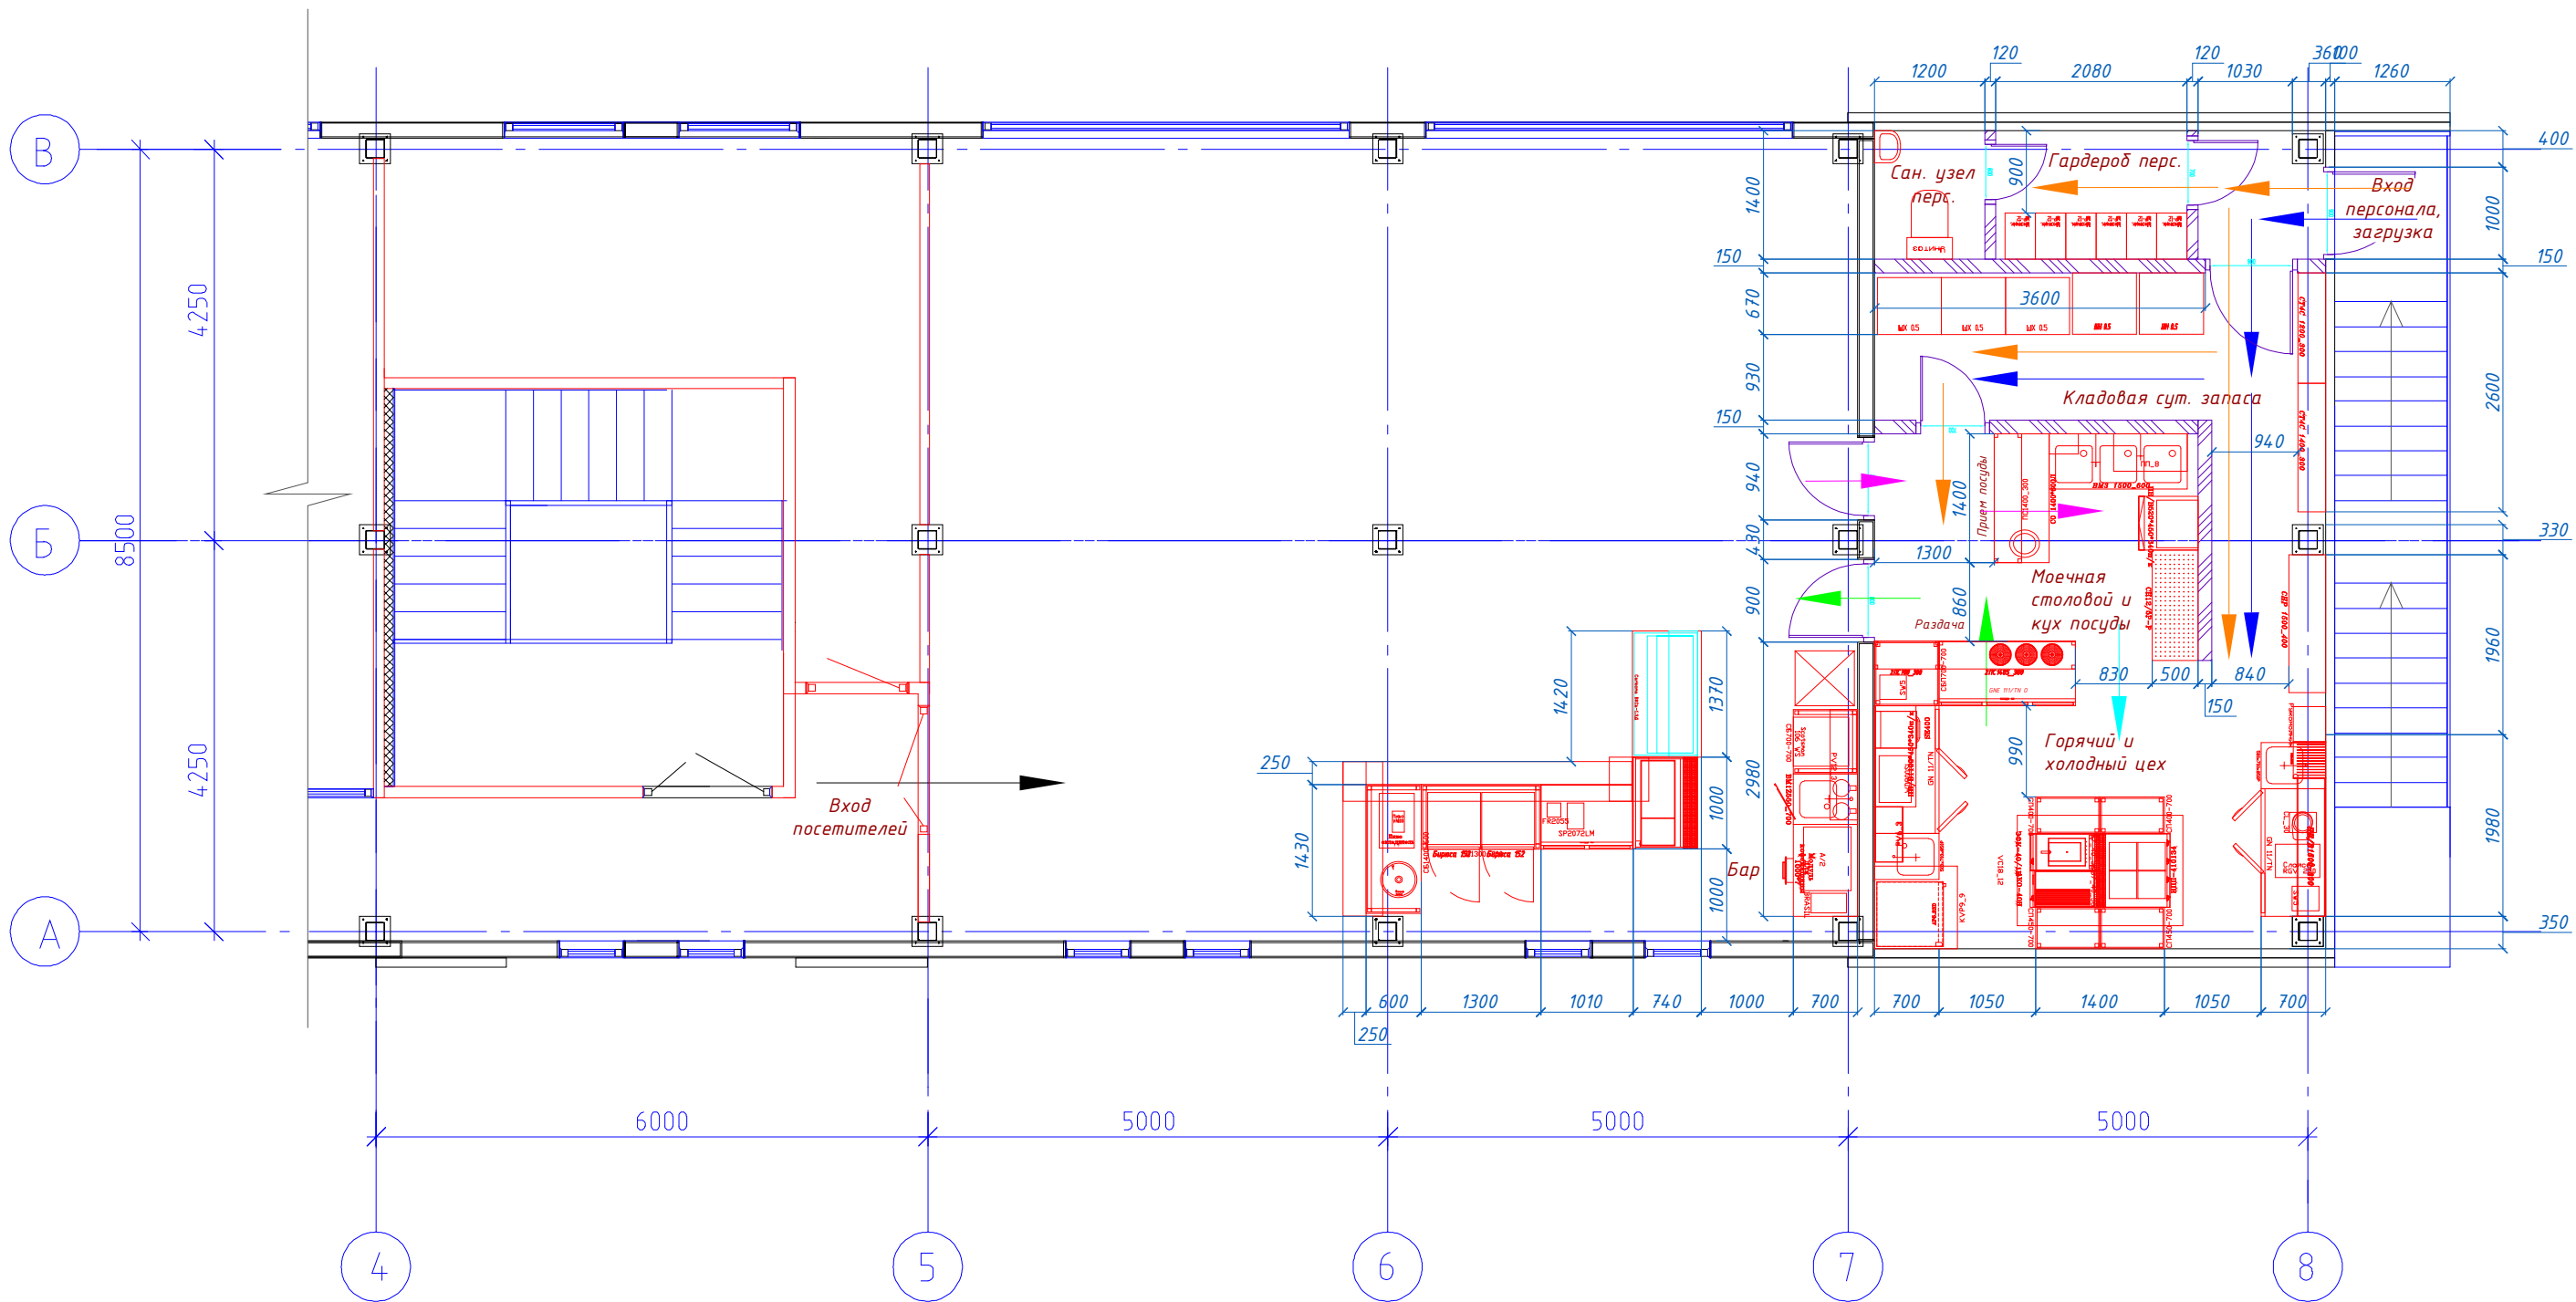

Масштаб 1:75

Схема движения потоков

	Сотрудники
	Полуфабрикаты
	Готовые блюда
	Грязная посуда
	Чистая посуда
	Посетители


						1052.ТХ			
						Московская обл.,			
Изм.	Кол.уч.	Лист	док.	Подпись	Дата	Технологическая часть проекта. Технологиф Кафе при Автомойке.	Стадия	Лист	Листов
Рук.пр-та.				Секацкий	16.12.2021		П		5
Технолог				Савочкин	16.12.2021	План расстановки технологического оборудования План на отметке +0.000			

Согласовано

Взам. инв. №

Подп. и дата

Инв. № подл.

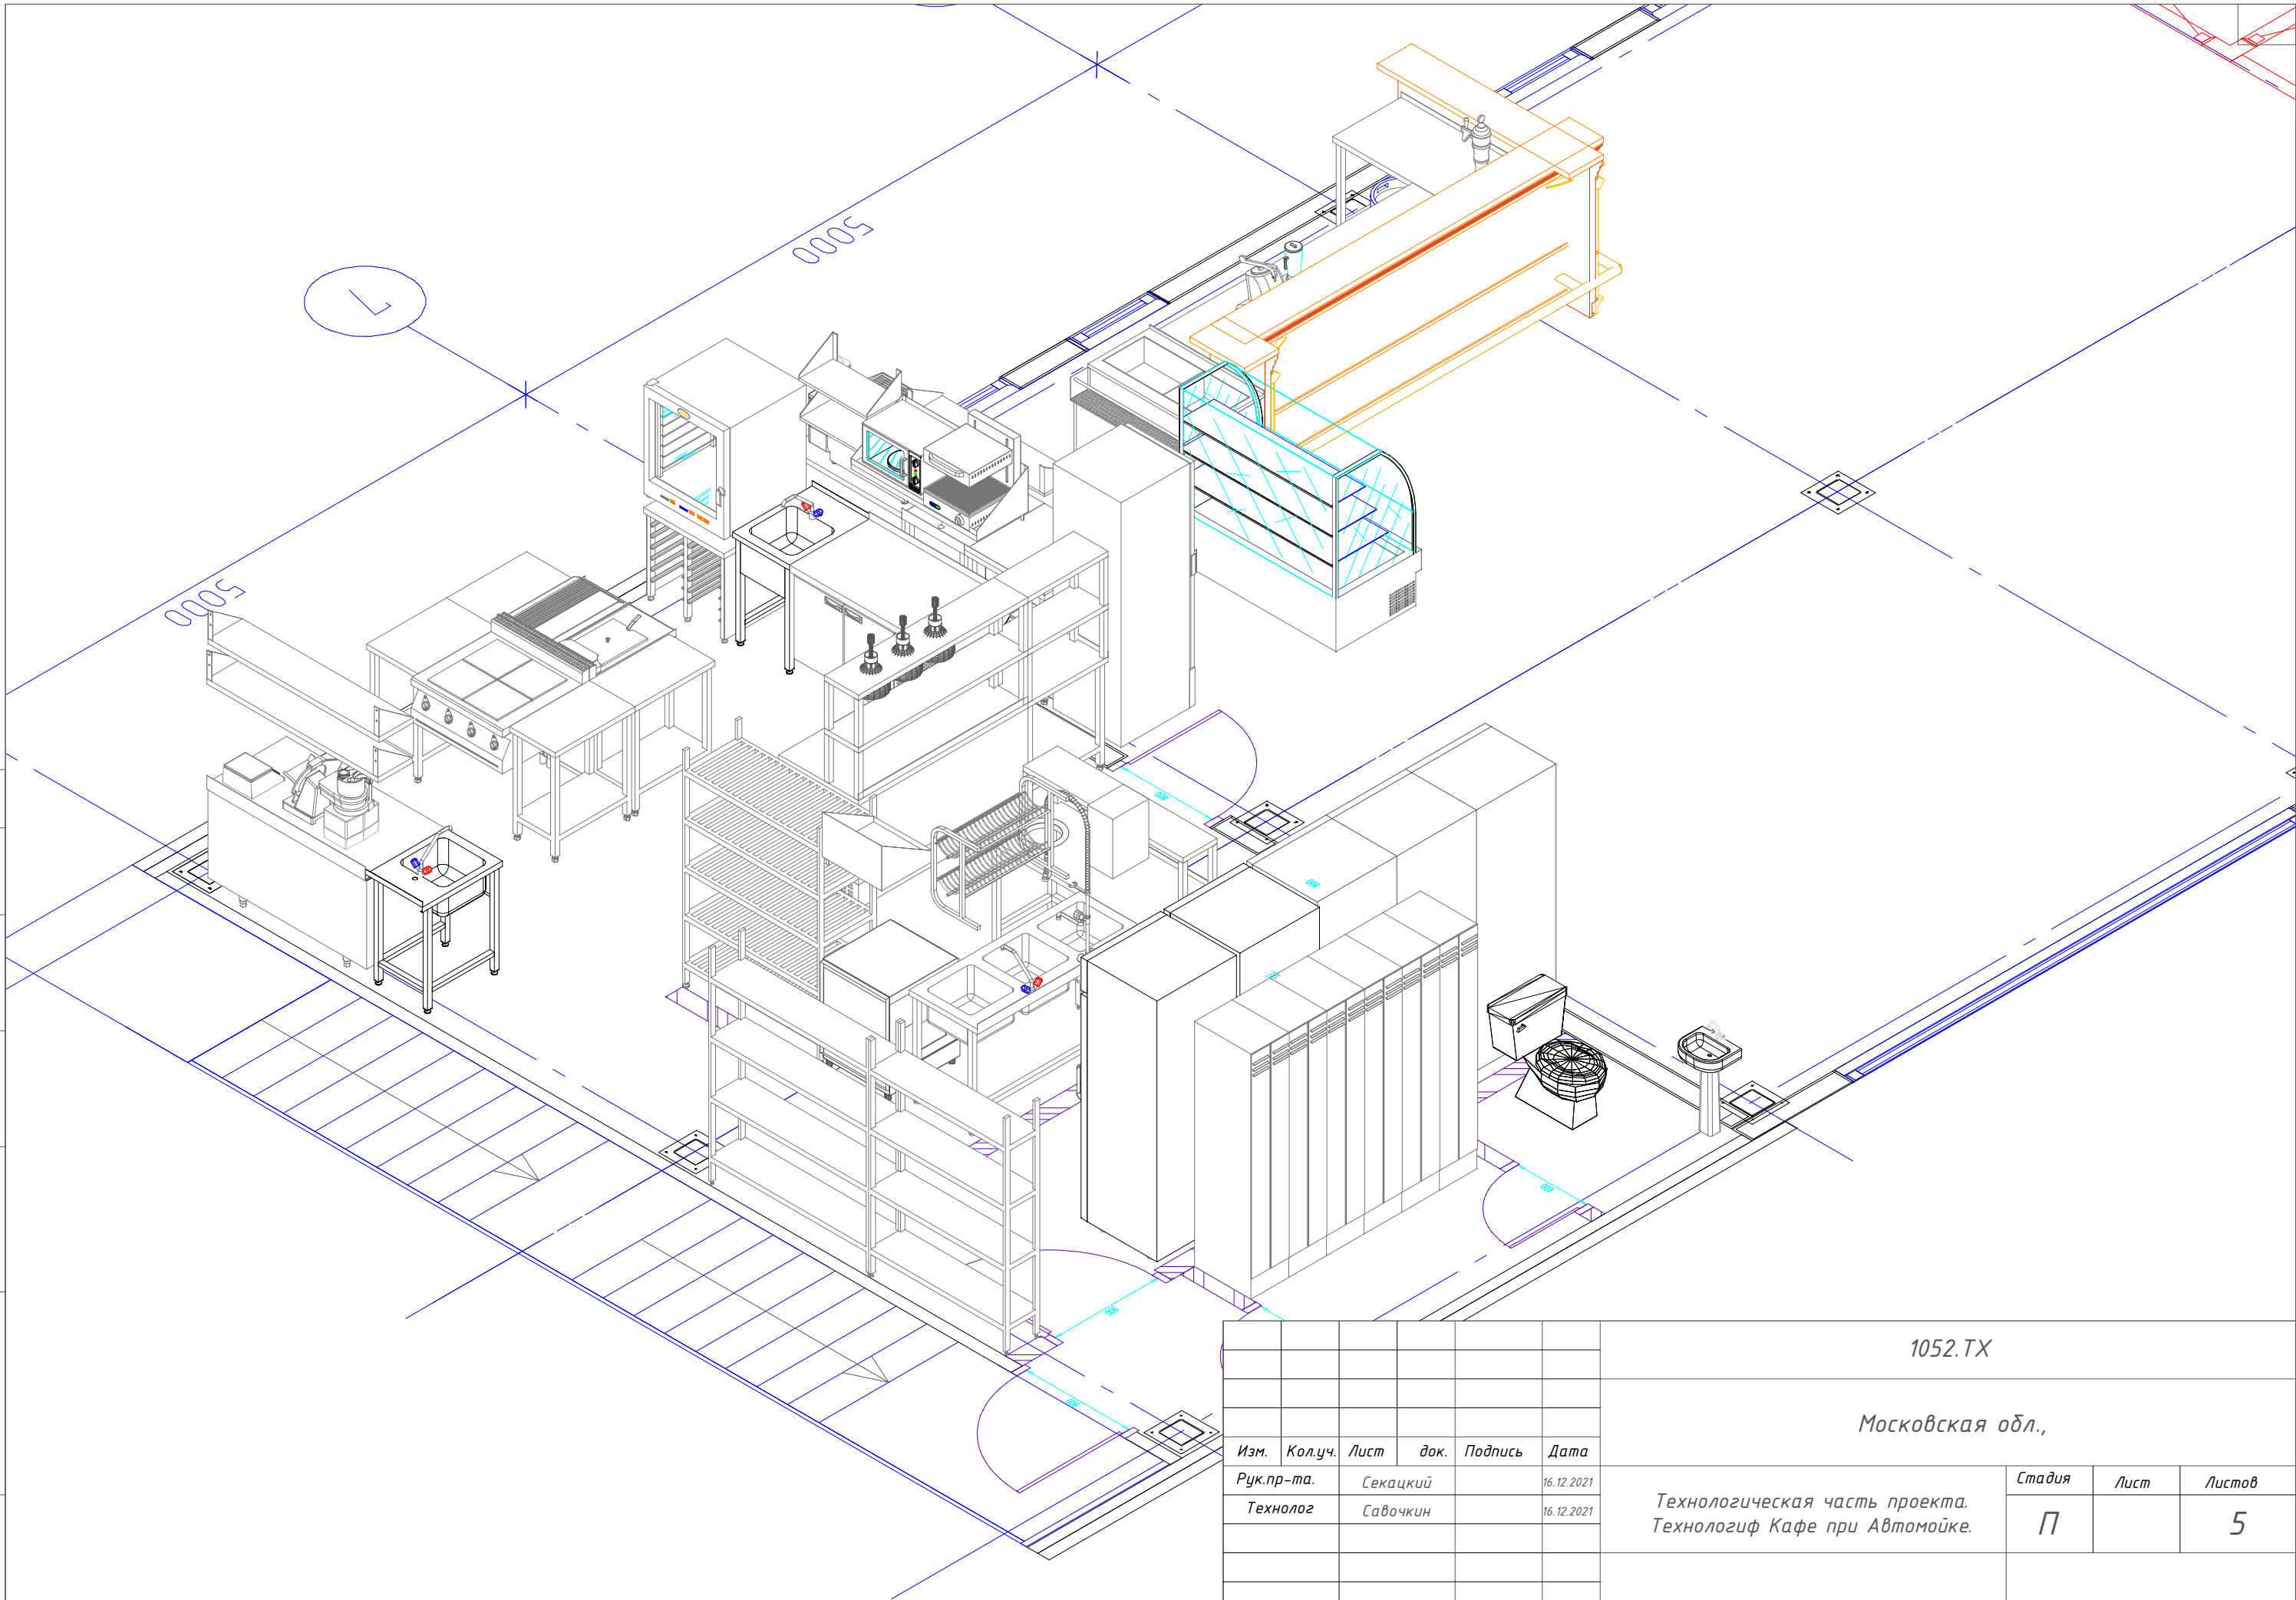

Изм.	Кол.уч.	Лист	док.	Подпись	Дата
Рук.пр-та.	Секацкий				16.12.2021
Технолог	Савочкин				16.12.2021


1052.ТХ			
Московская обл.,			
Технологическая часть проекта. Технологиф Кафе при Автомойке.	Стадия	Лист	Листов
	П		5
План на отметке +0.000			

Согласовано

Взам. инв. №

Подп. и дата

Инв. № подл.

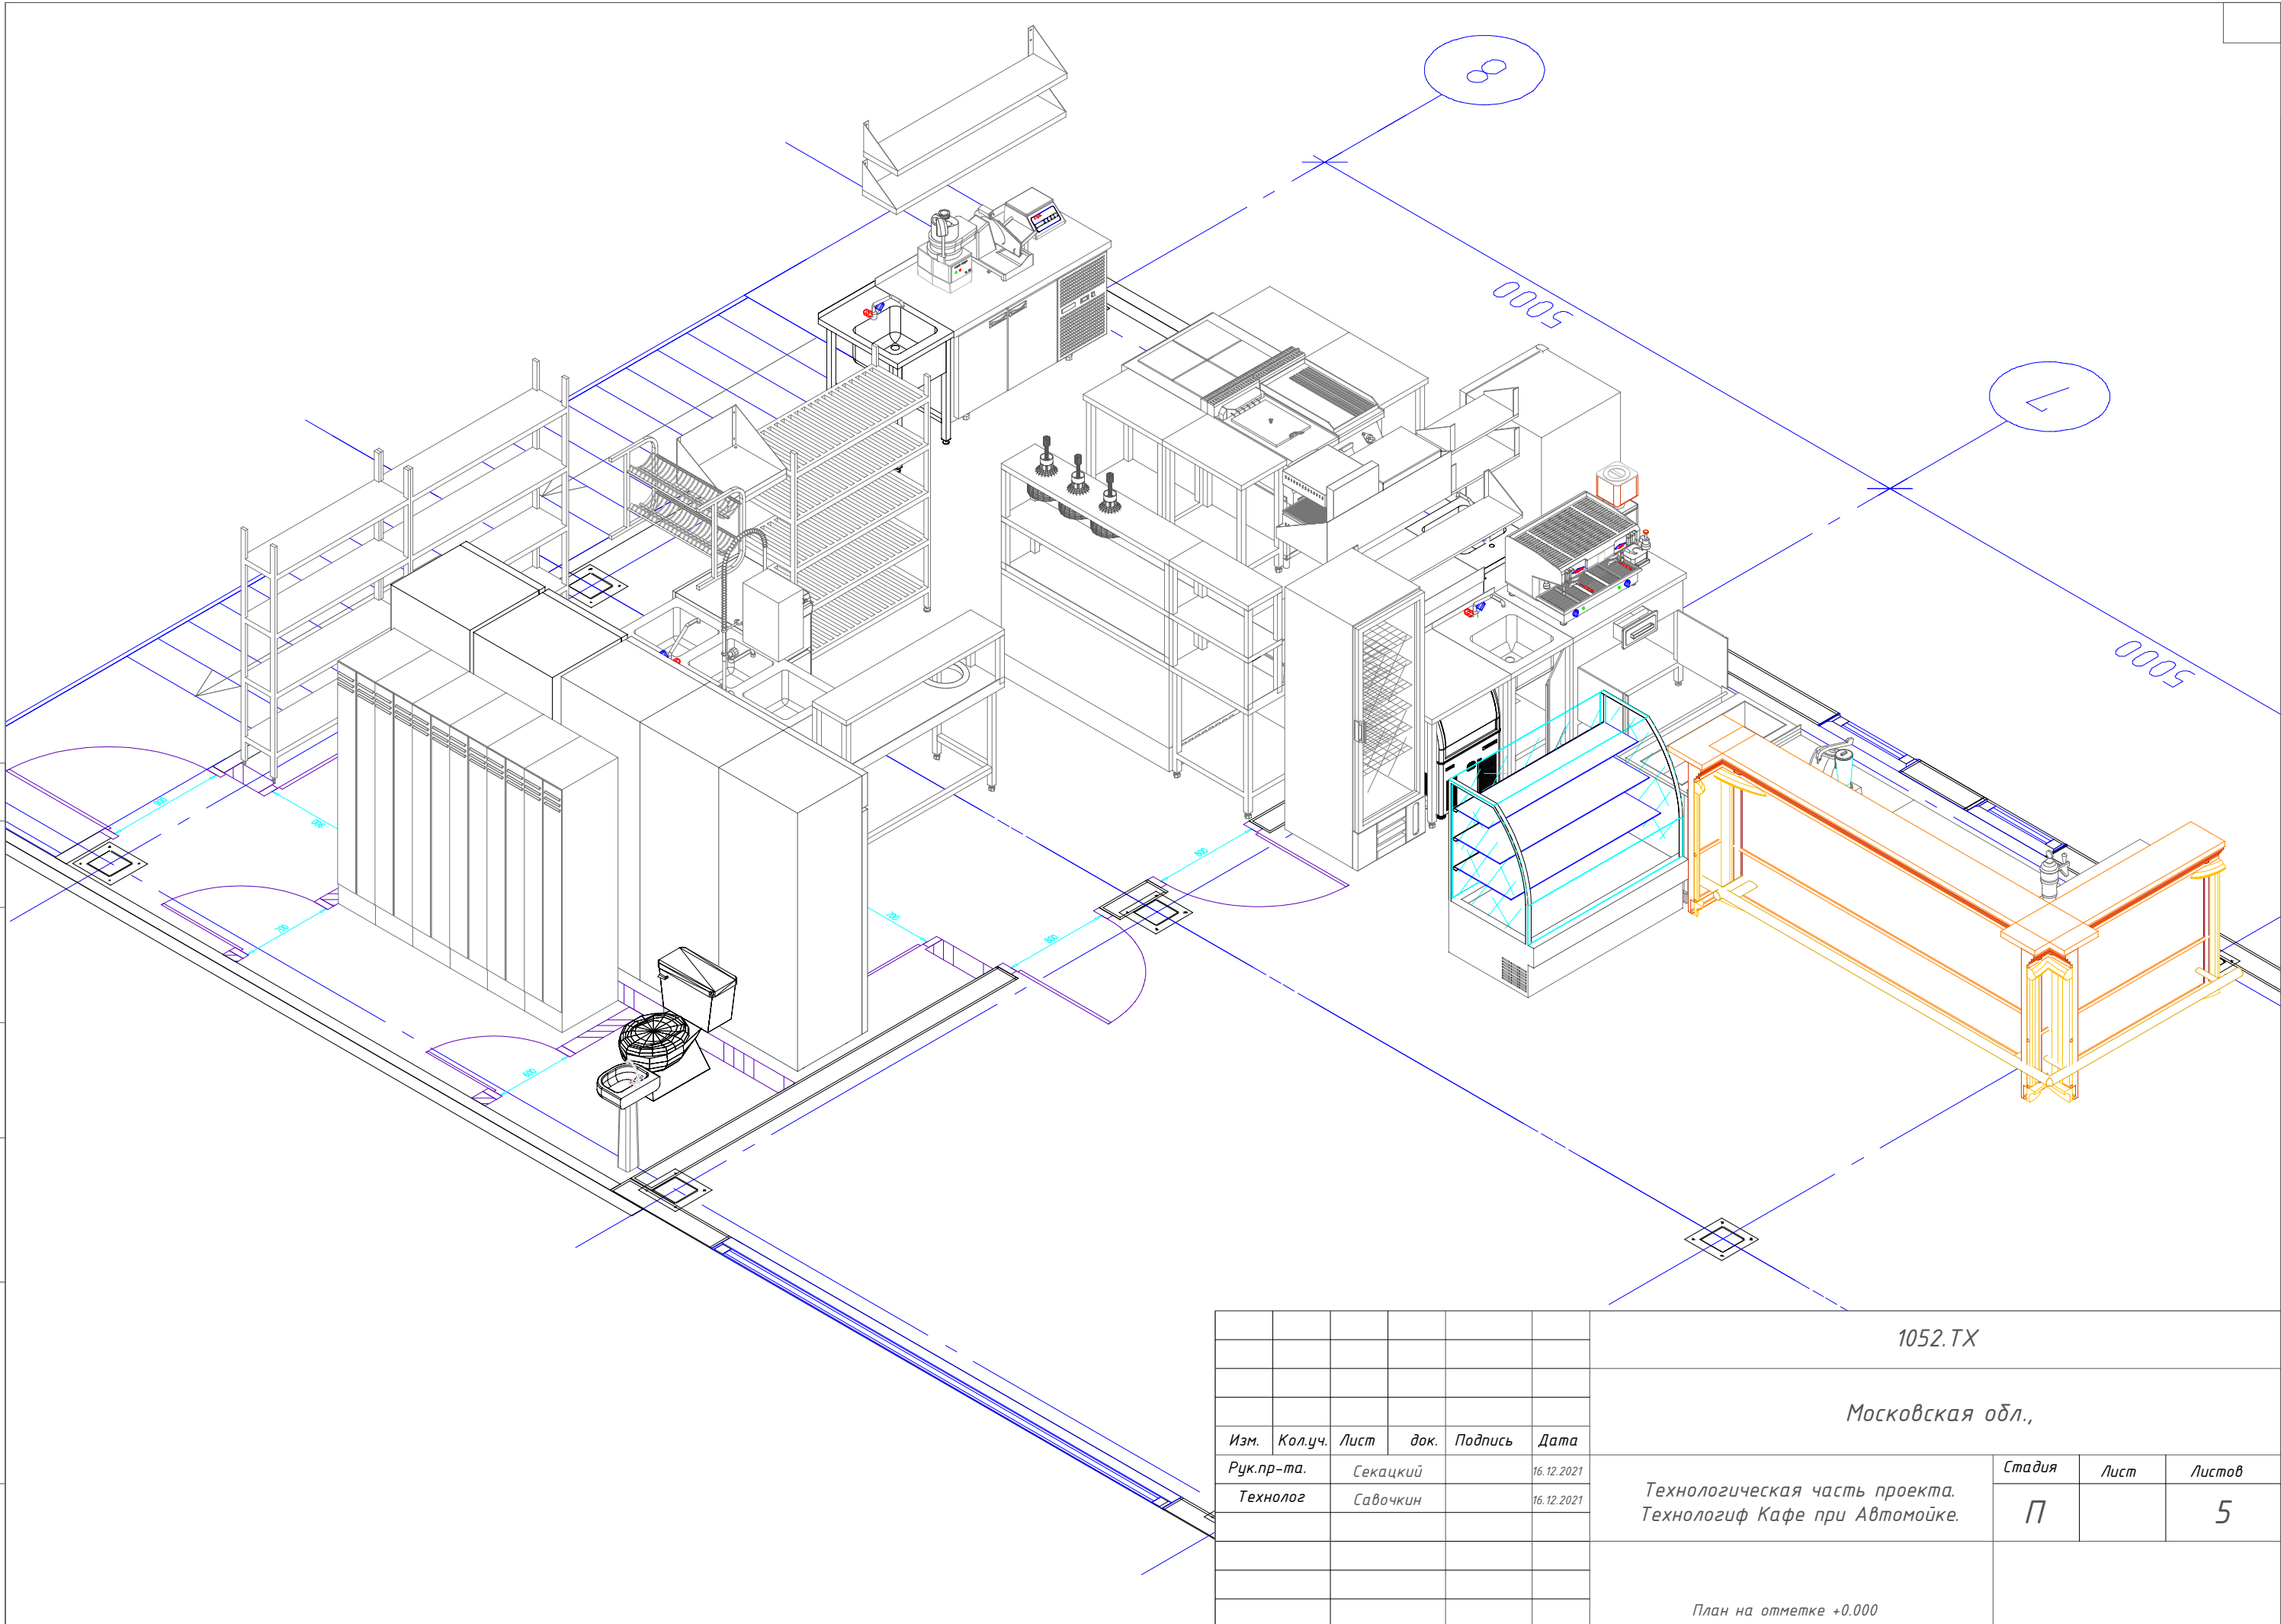

Изм.	Кол.уч.	Лист	док.	Подпись	Дата
Рук.пр-та.	Секацкий				16.12.2021
Технолог	Савочкин				16.12.2021


1052.ТХ			
Московская обл.,			
Технологическая часть проекта. Технологиф Кафе при Автомойке.	Стадия	Лист	Листов
	П		5
План на отметке +0.000			

Согласовано

Взам. инв. №

Подп. и дата

Инв. № подл.

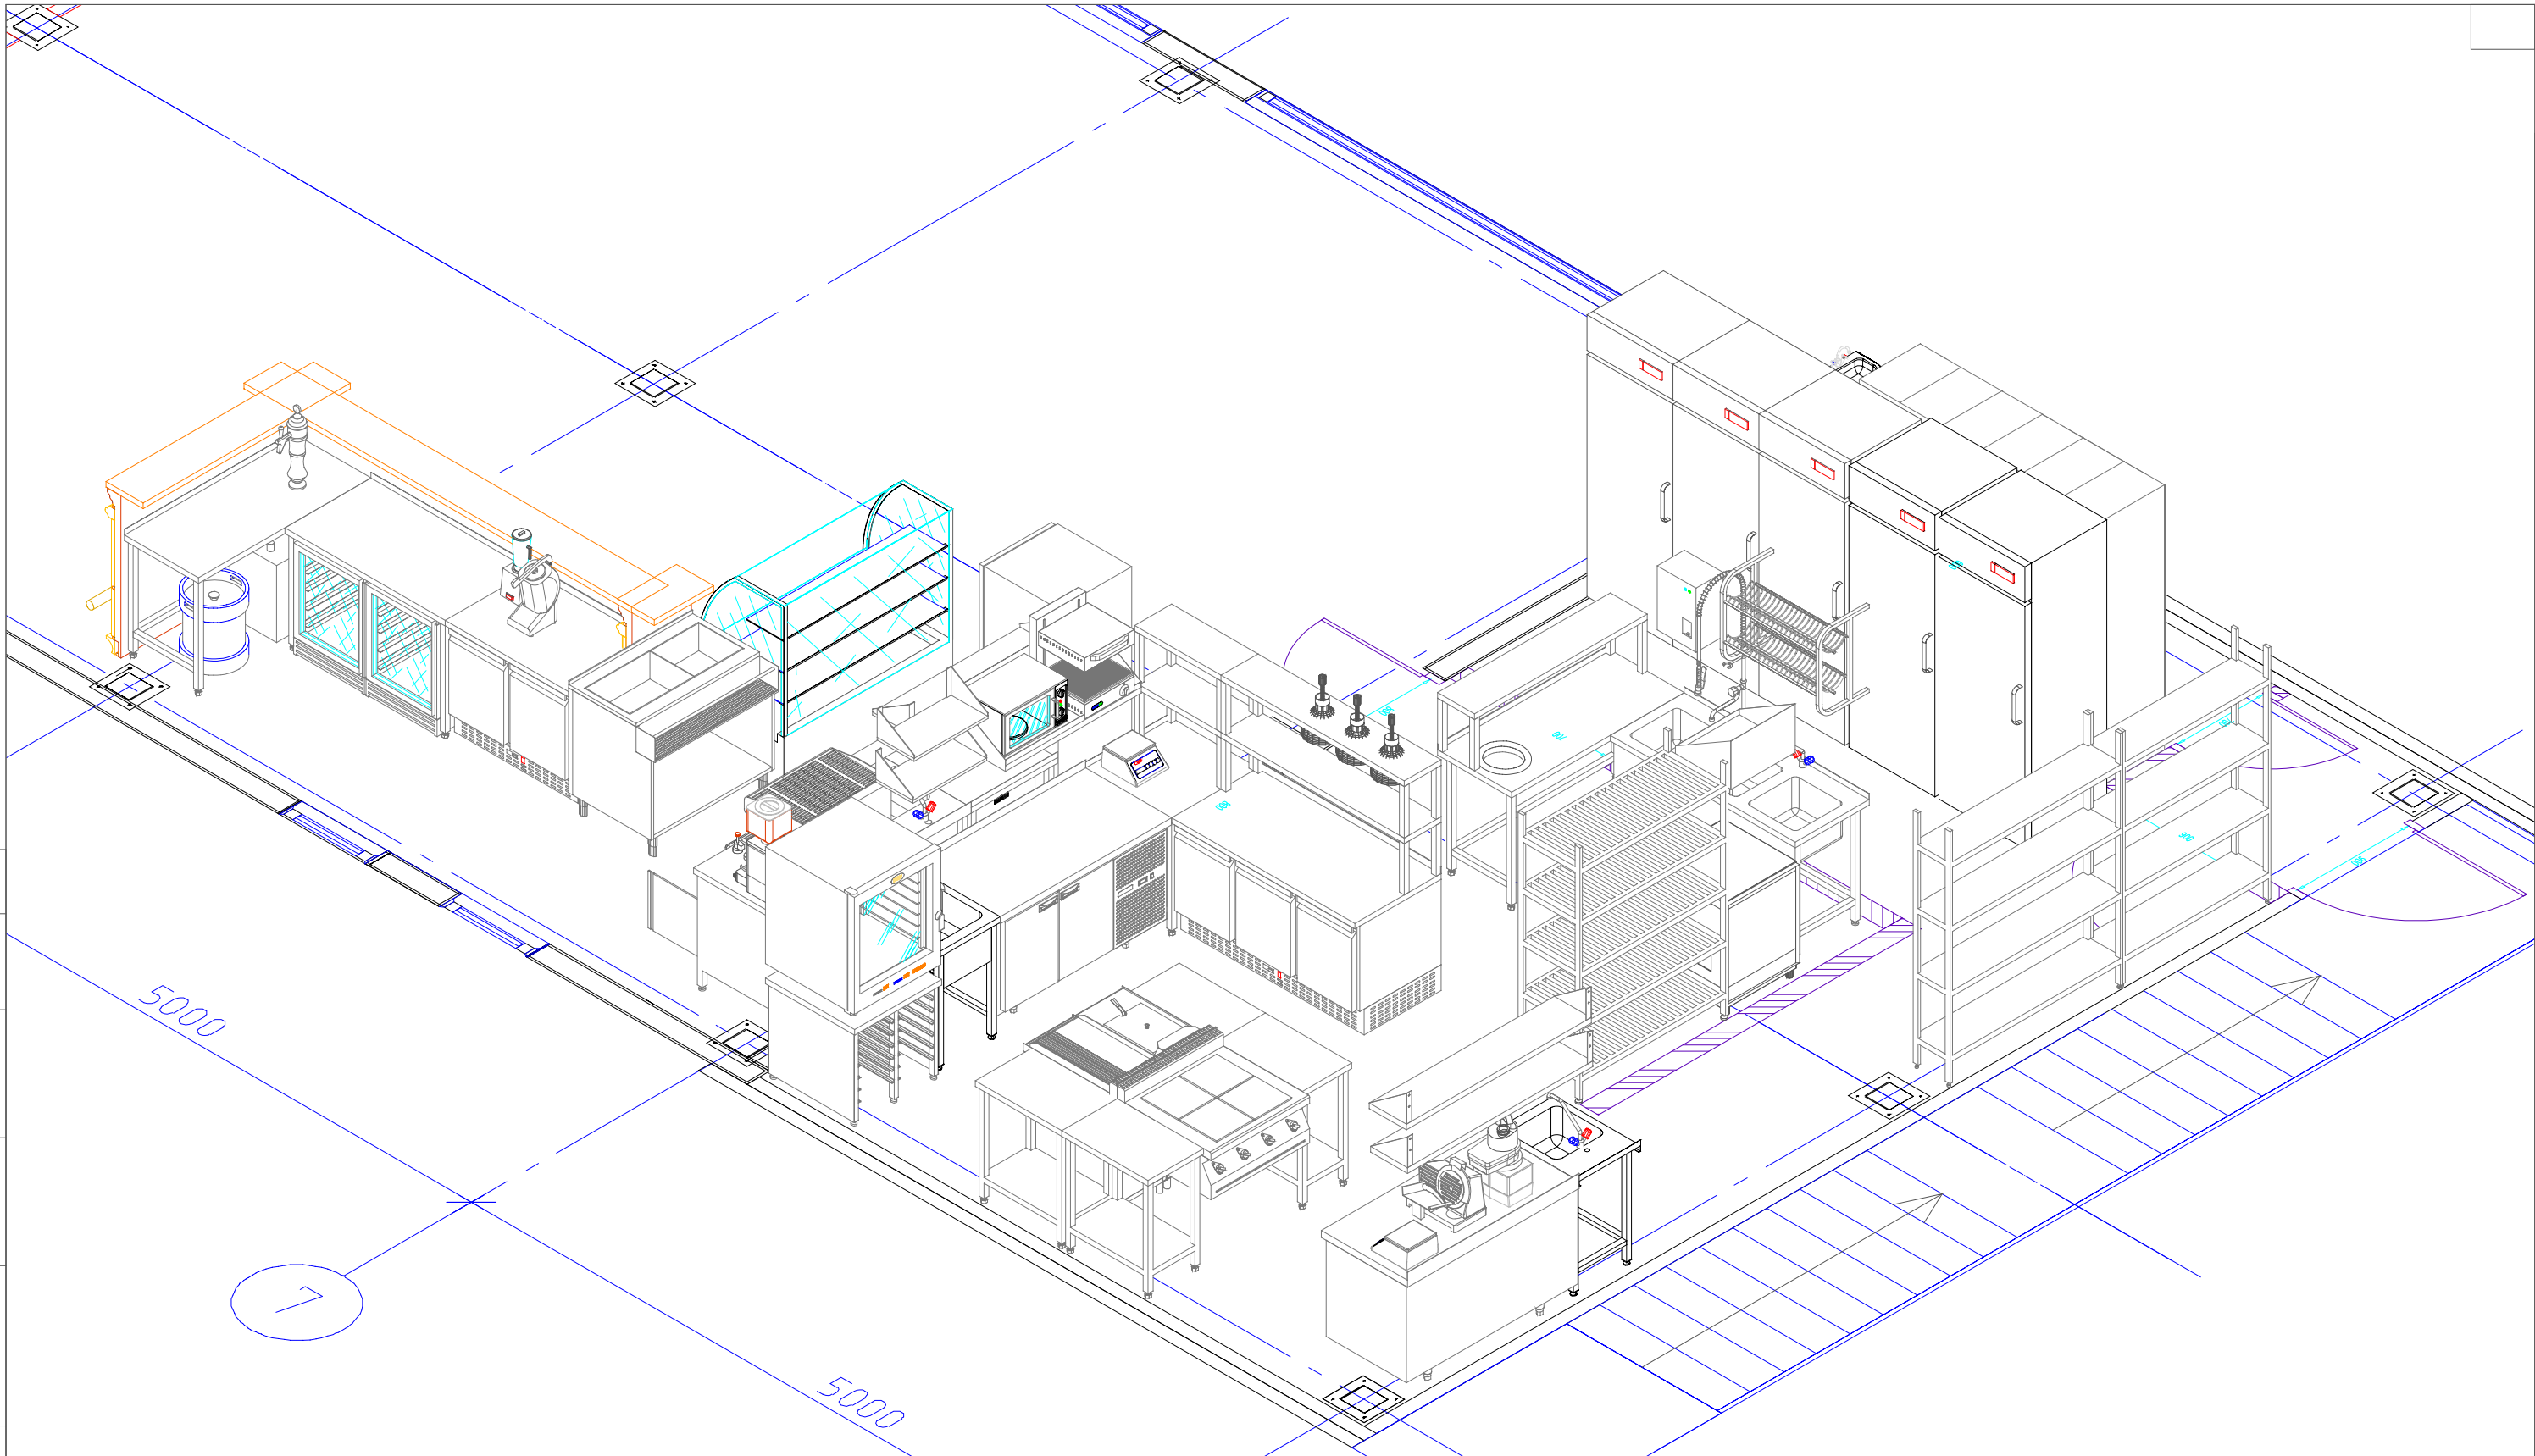

						1052.ТХ		
						Московская обл.,		
Изм.	Кол.уч.	Лист	док.	Подпись	Дата	Технологическая часть проекта. Технологиф Кафе при Автомойке.	Стадия	Лист
Рук.пр-та.		Секацкий			16.12.2021		П	5
Технолог		Савочкин			16.12.2021			
						План на отметке +0.000		