


Согласовано

Инд. № подл. Подп. и дата Взам. инд. №

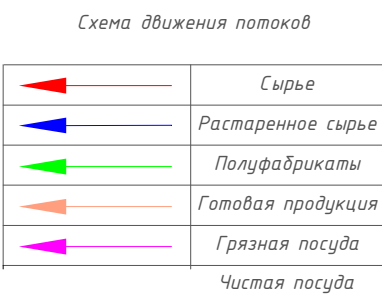


Масштаб 1:75

						1181.TX			
						Владимирская область, городской округ Покров, посёлок Введенский			
Изм.	Кол.уч.	Лист	док.	Подпись	Дата	Технологические решения. Технология пекарни с Кафе.	Стадия	Лист	Листов
Разраб.	Савочкин				13.09.2025		Р		5
Проверил	Савочкин				13.09.2025	План расстановки технологического оборудования План на отметке +0.000			
Заказчик									

Согласовано


Изм. № подл. Подп. и дата Взам. инв. №

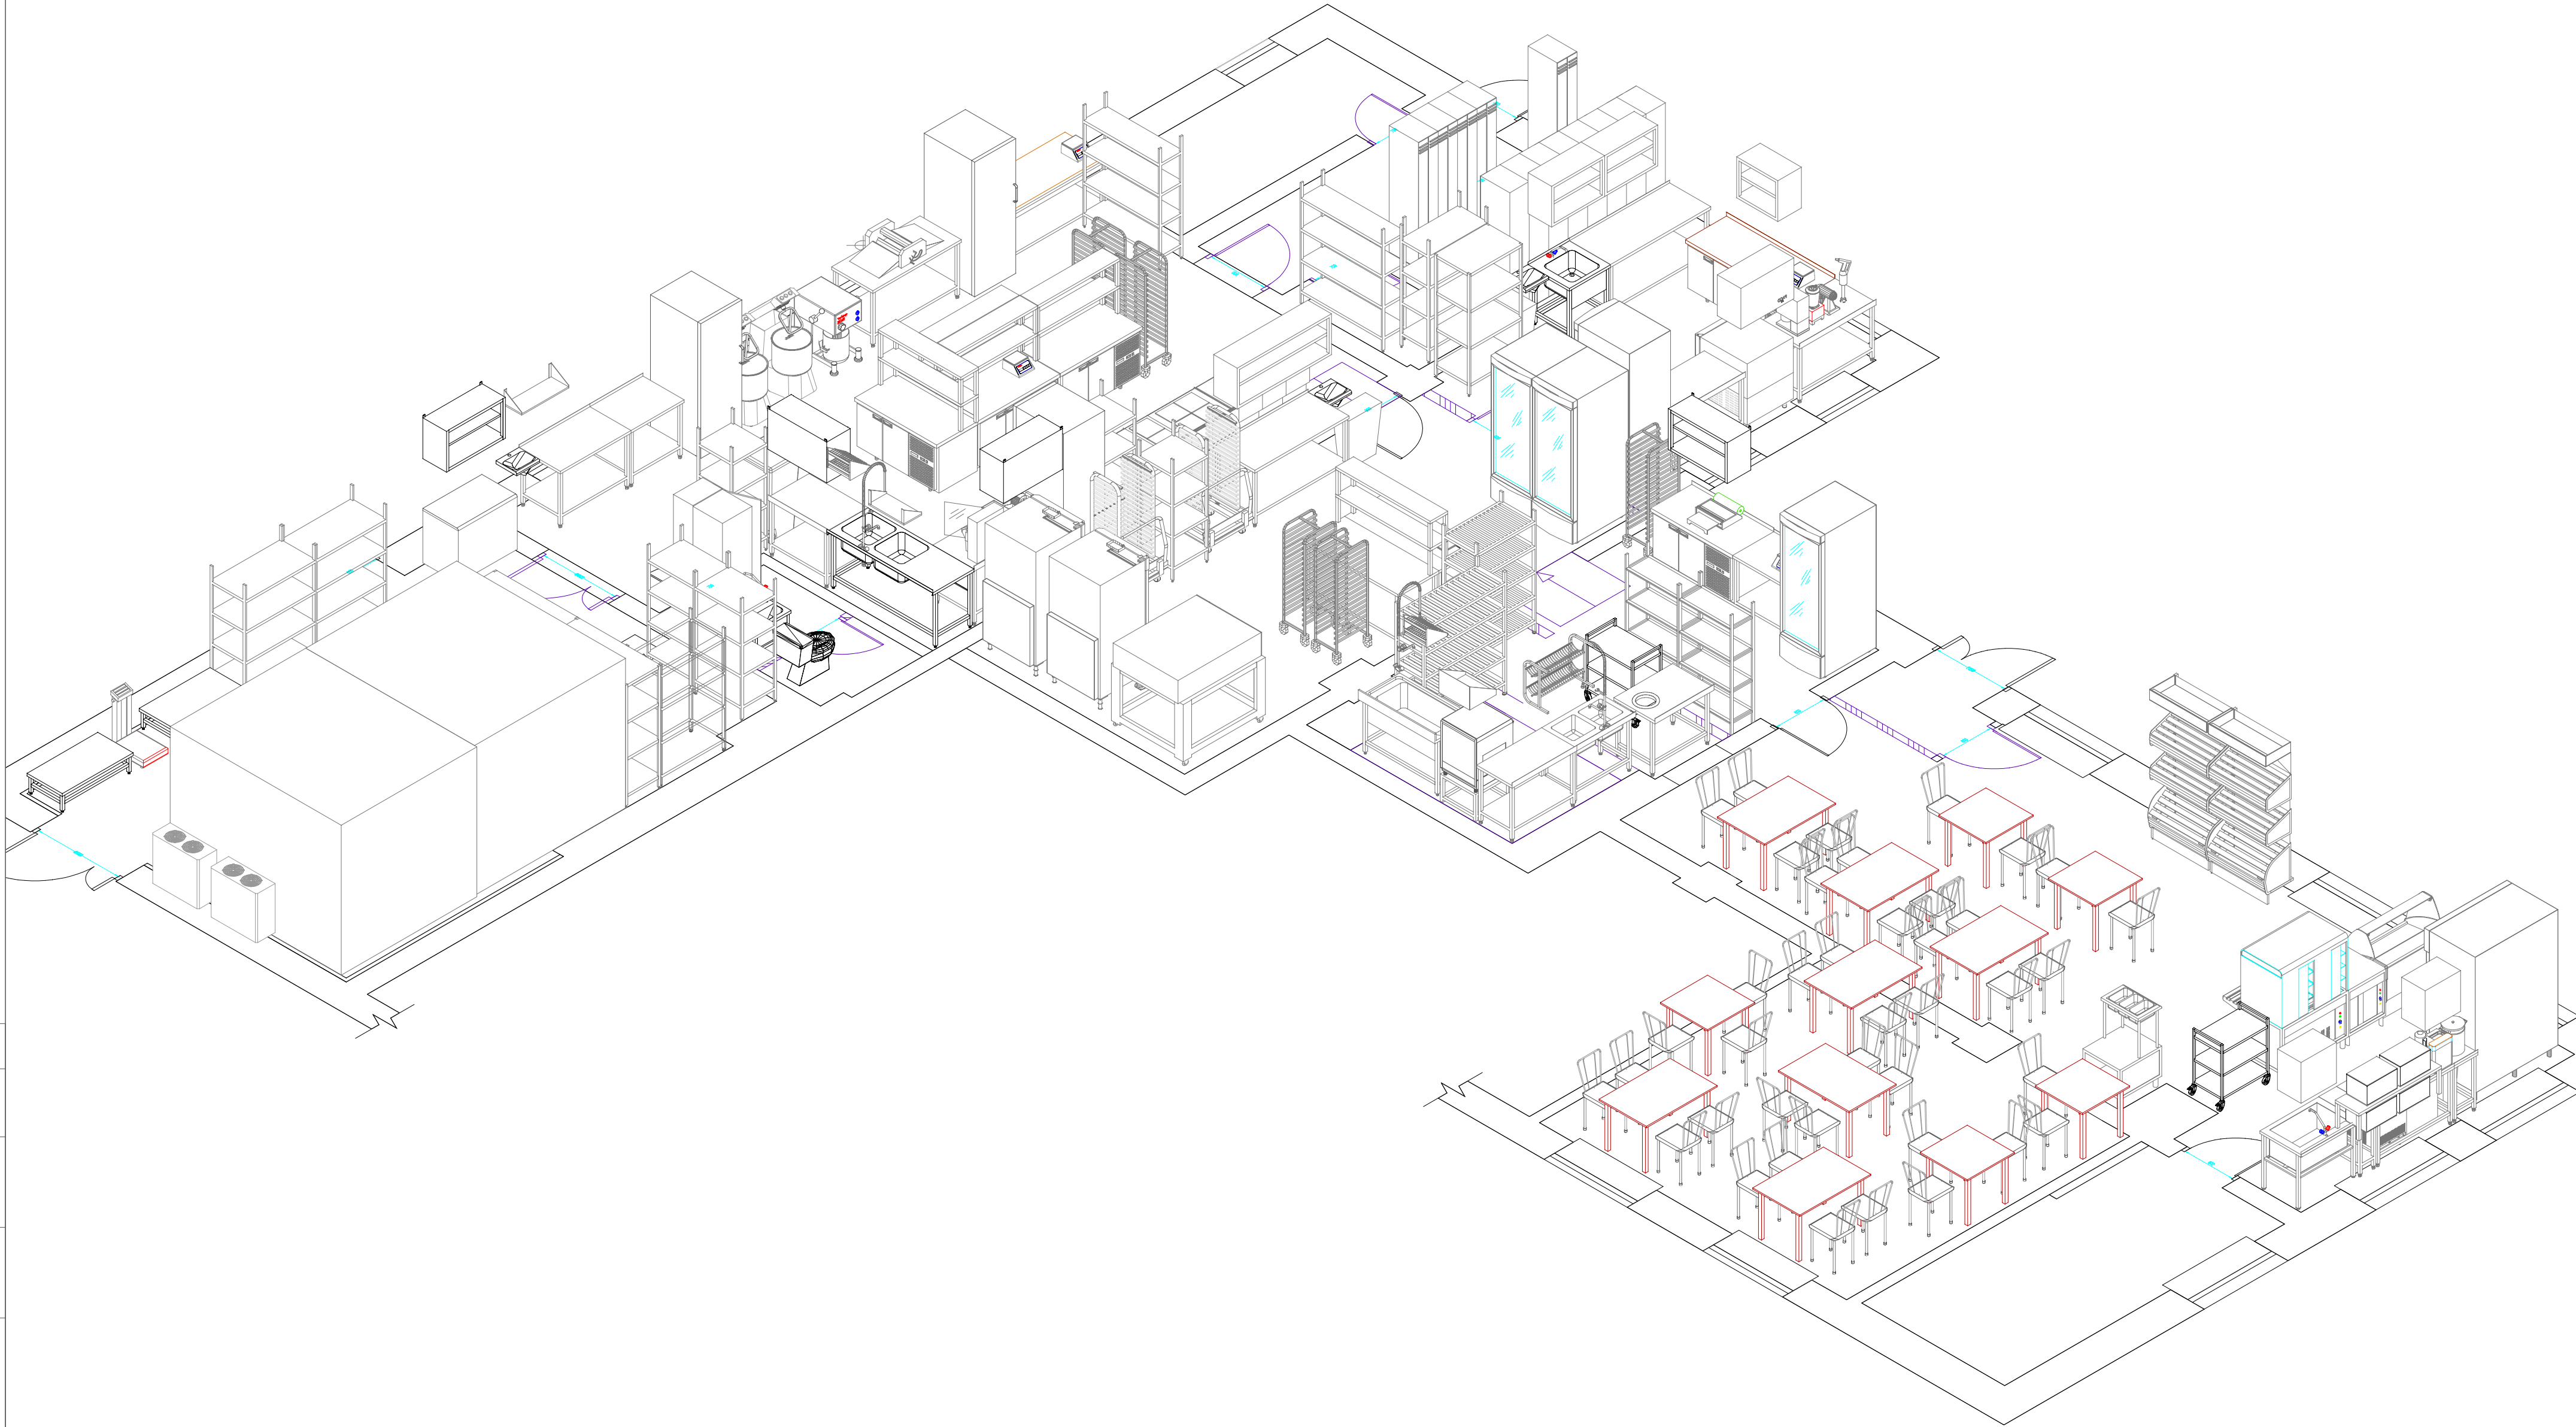

						1181.TX			
						Владимирская область, городской округ Покров, посёлок Введенский			
Изм.	Кол.уч.	Лист	док.	Подпись	Дата	Технологические решения. Технология пекарни с Кафе.	Стадия	Лист	Листов
Разраб.		Савочкин			13.09.2025		Р		5
Проверил		Савочкин			13.09.2025				
Заказчик						План на отметке +0.000			

Согласовано


Инв. № подл. Подп. и дата. Взам. инв. №

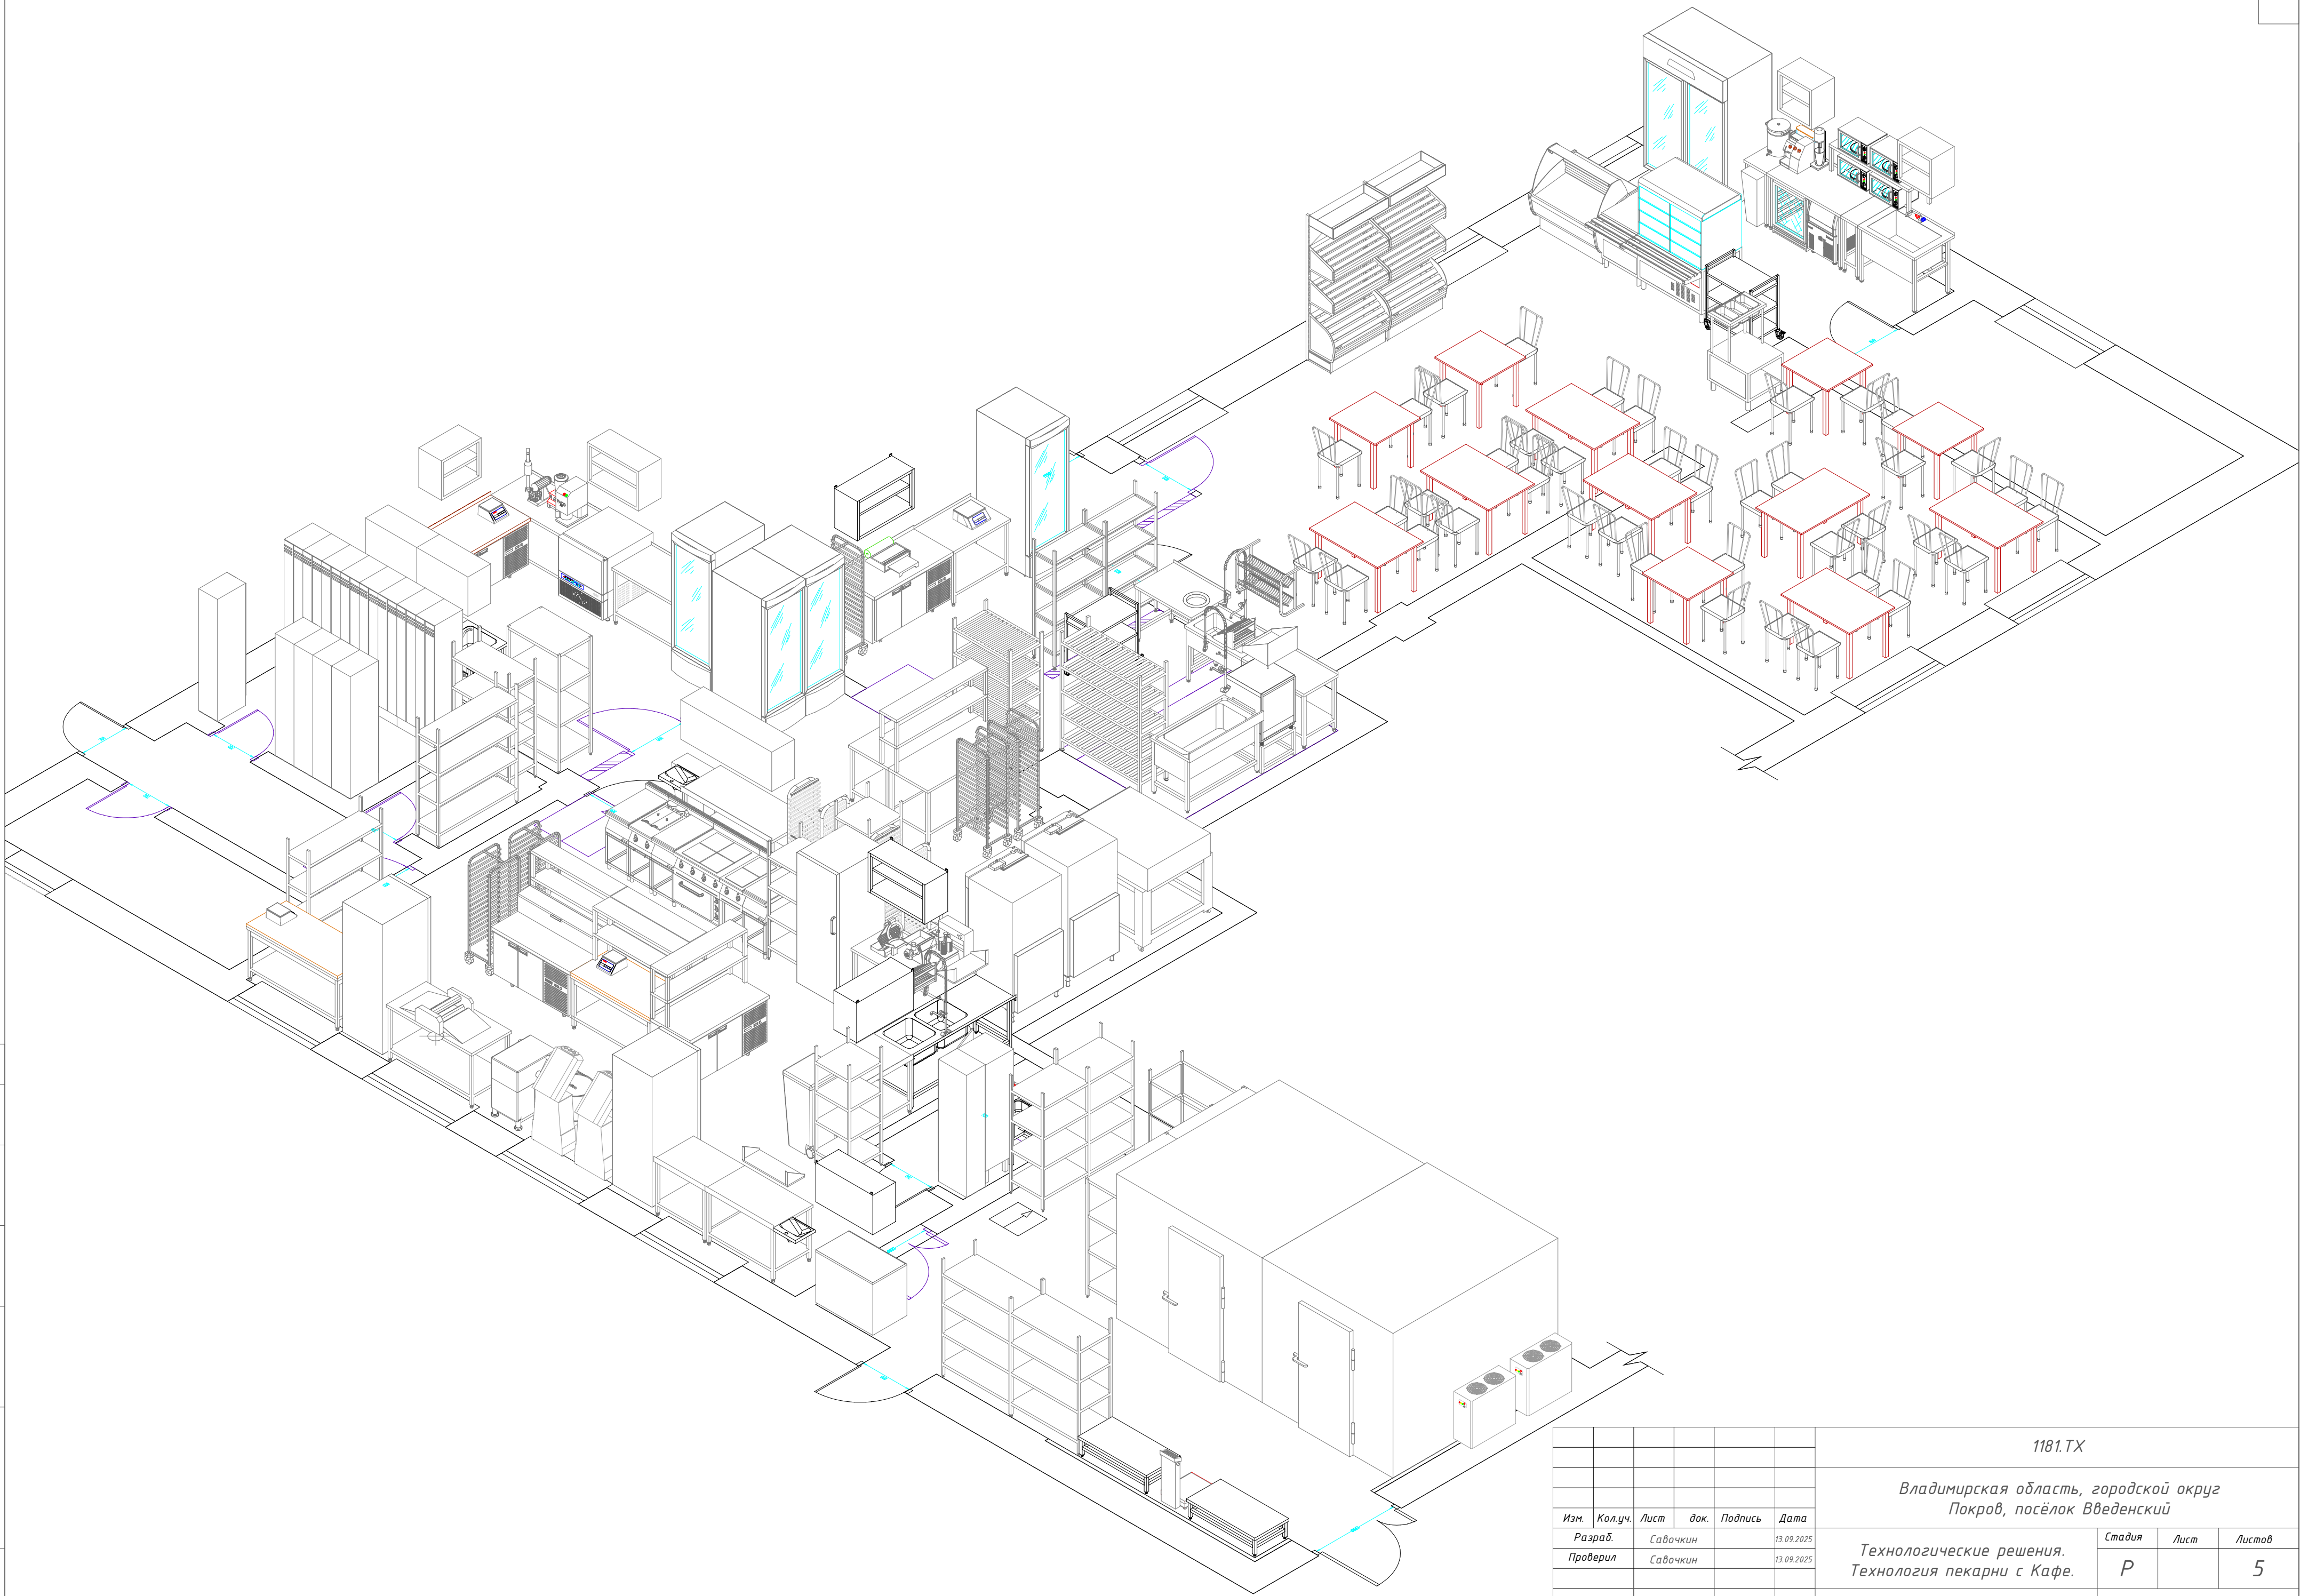

						1181.TX			
						Владимирская область, городской округ Покров, посёлок Введенский			
Изм.	Колуч.	Лист	док.	Подпись	Дата	Технологические решения. Технология пекарни с Кафе.	Стадия	Лист	Листов
Разраб.		Савочкин		13.09.2025			Р		5
Проверил		Савочкин		13.09.2025					
Заказчик						План на отметке +0.000			

Согласовано

Инв. № подл. Подп. и дата Взам. инв. №

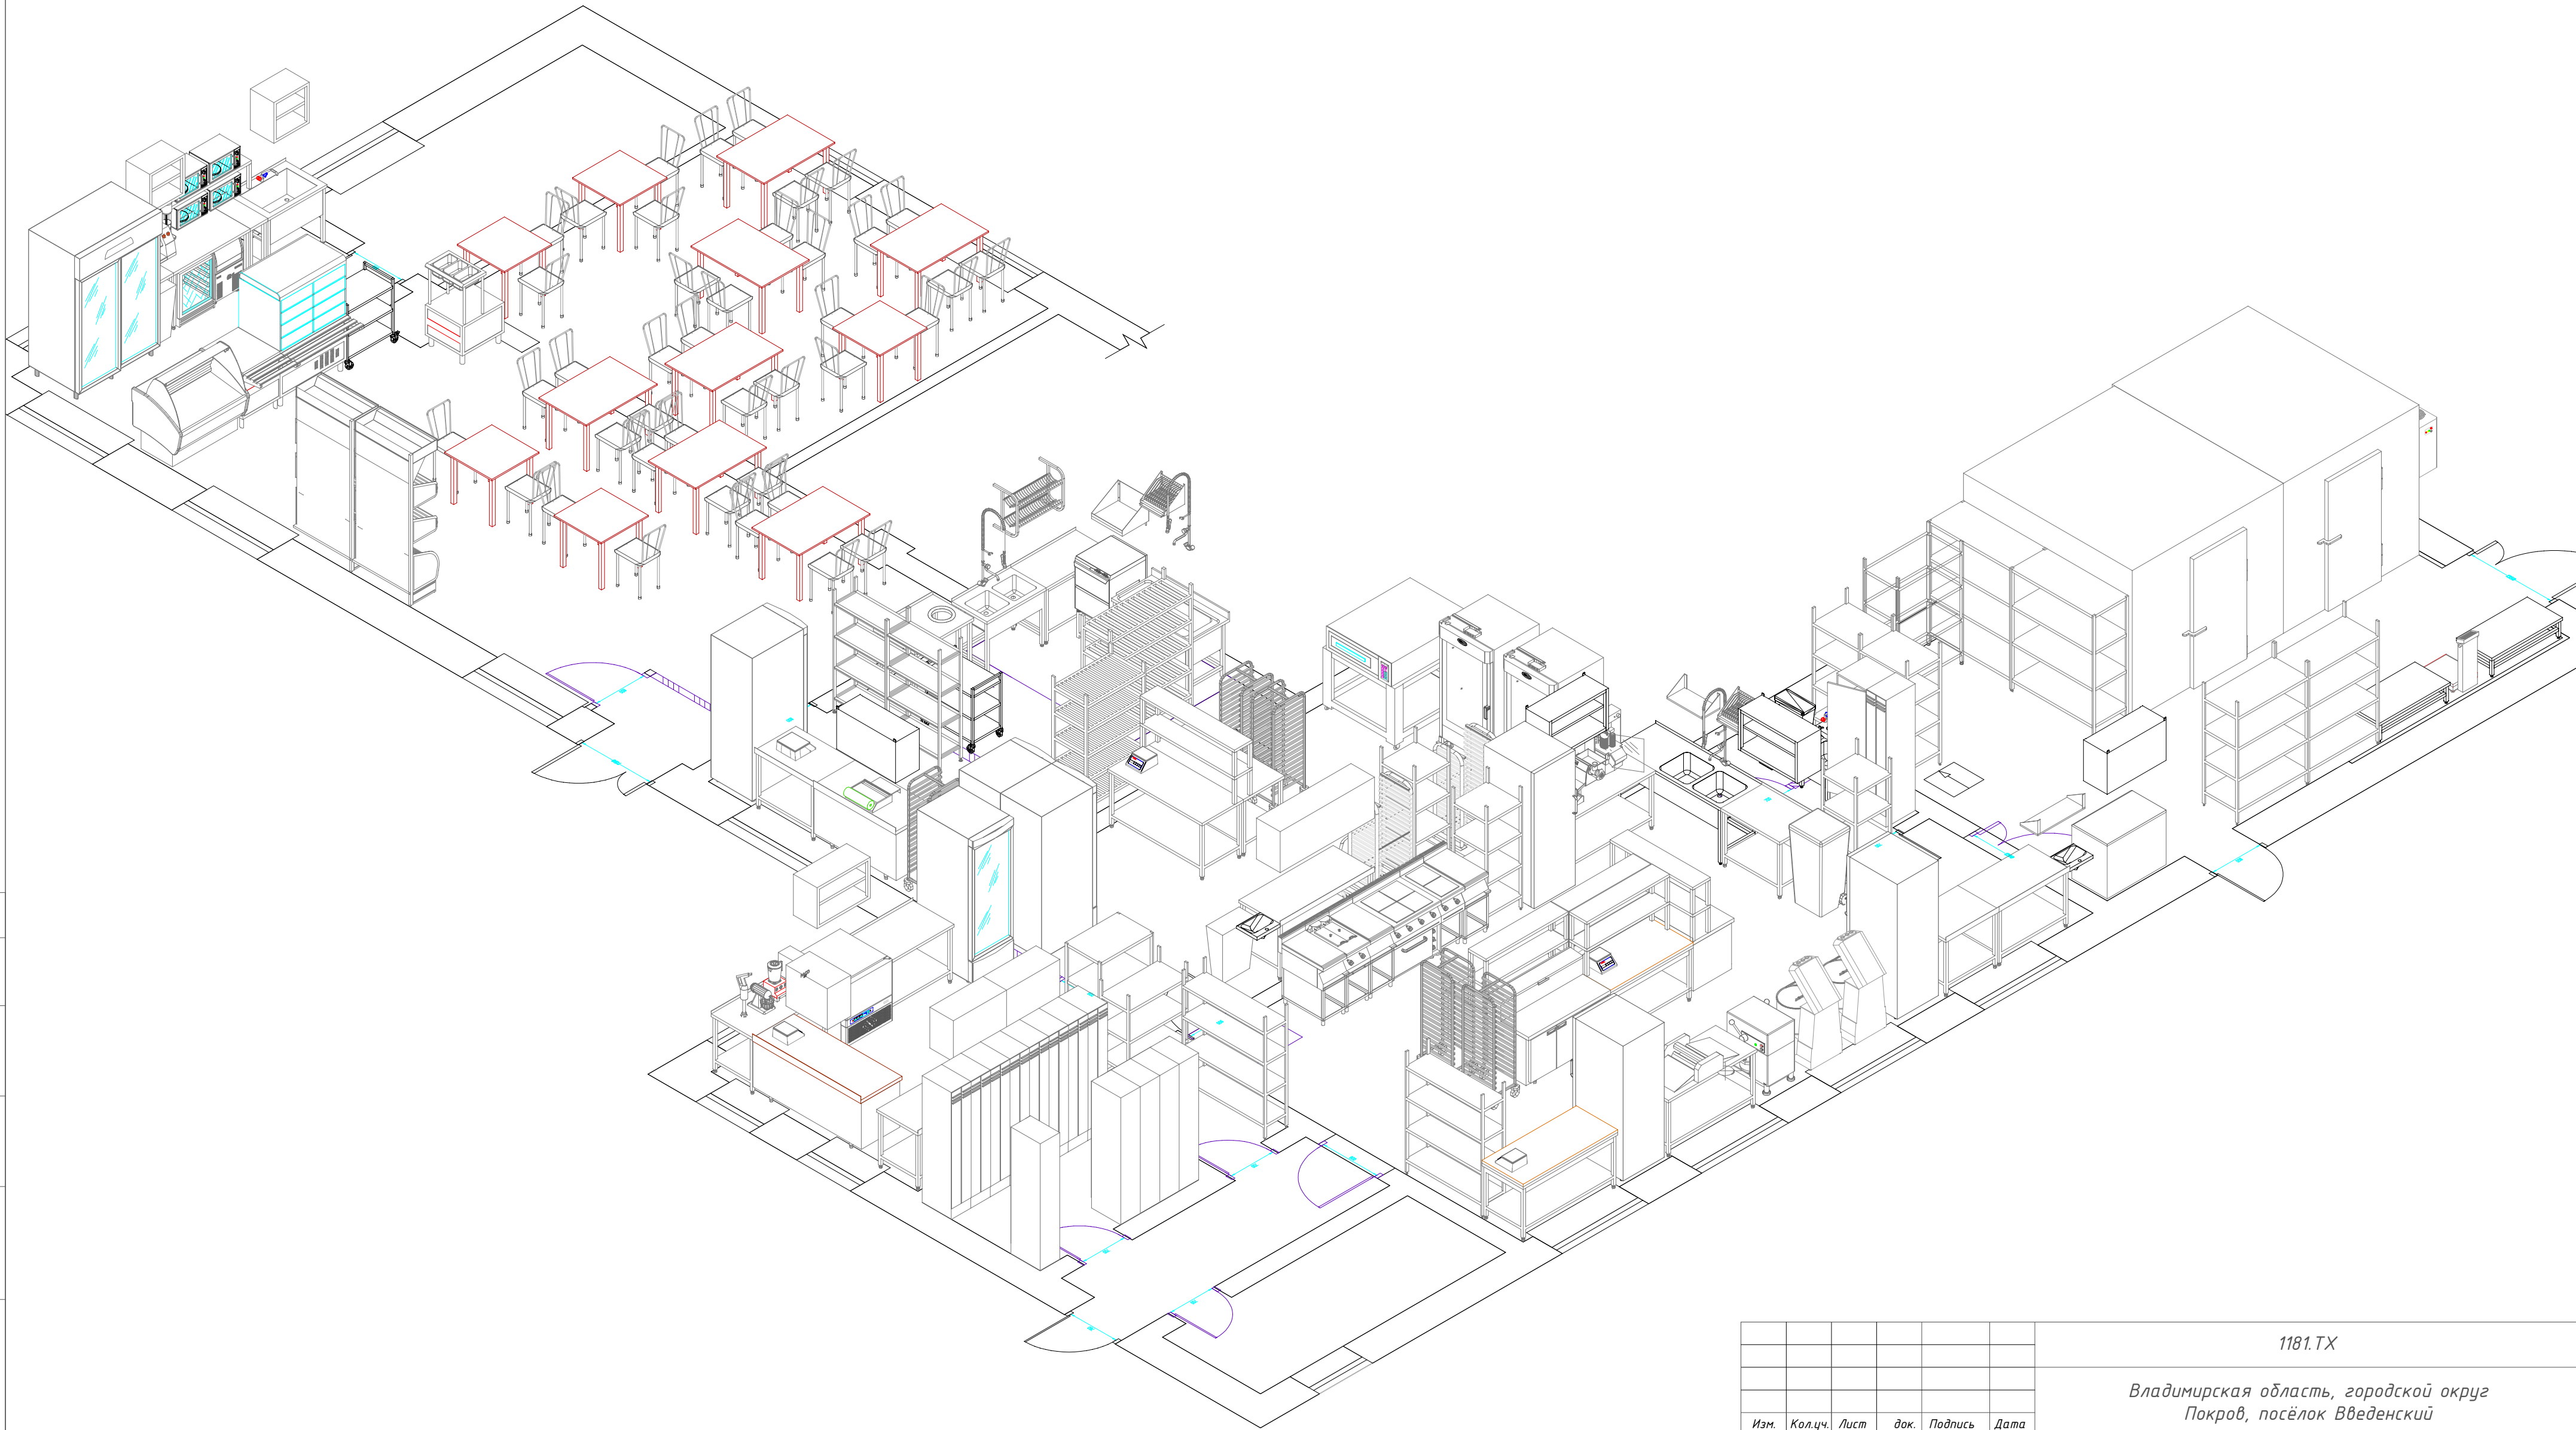

						1181.TX			
						Владимирская область, городской округ Покров, посёлок Введенский			
Изм.	Кол.уч.	Лист	док.	Подпись	Дата	Технологические решения. Технология пекарни с Кафе.	Стадия	Лист	Листов
Разраб.		Савочкин			13.09.2025		Р		5
Проверил		Савочкин			13.09.2025				
Заказчик						План на отметке +0.000			