

Схема движения потоков

	Сырье
	Полуфабрикаты
	Готовые блюда
	Грязная посуда
	Чистая посуда

М/1

М

Л/1

Л

К

И


Ж

Е/1

Е

Согласовано

Инд. № подл.	Подп. и дата	Взам. инд. №

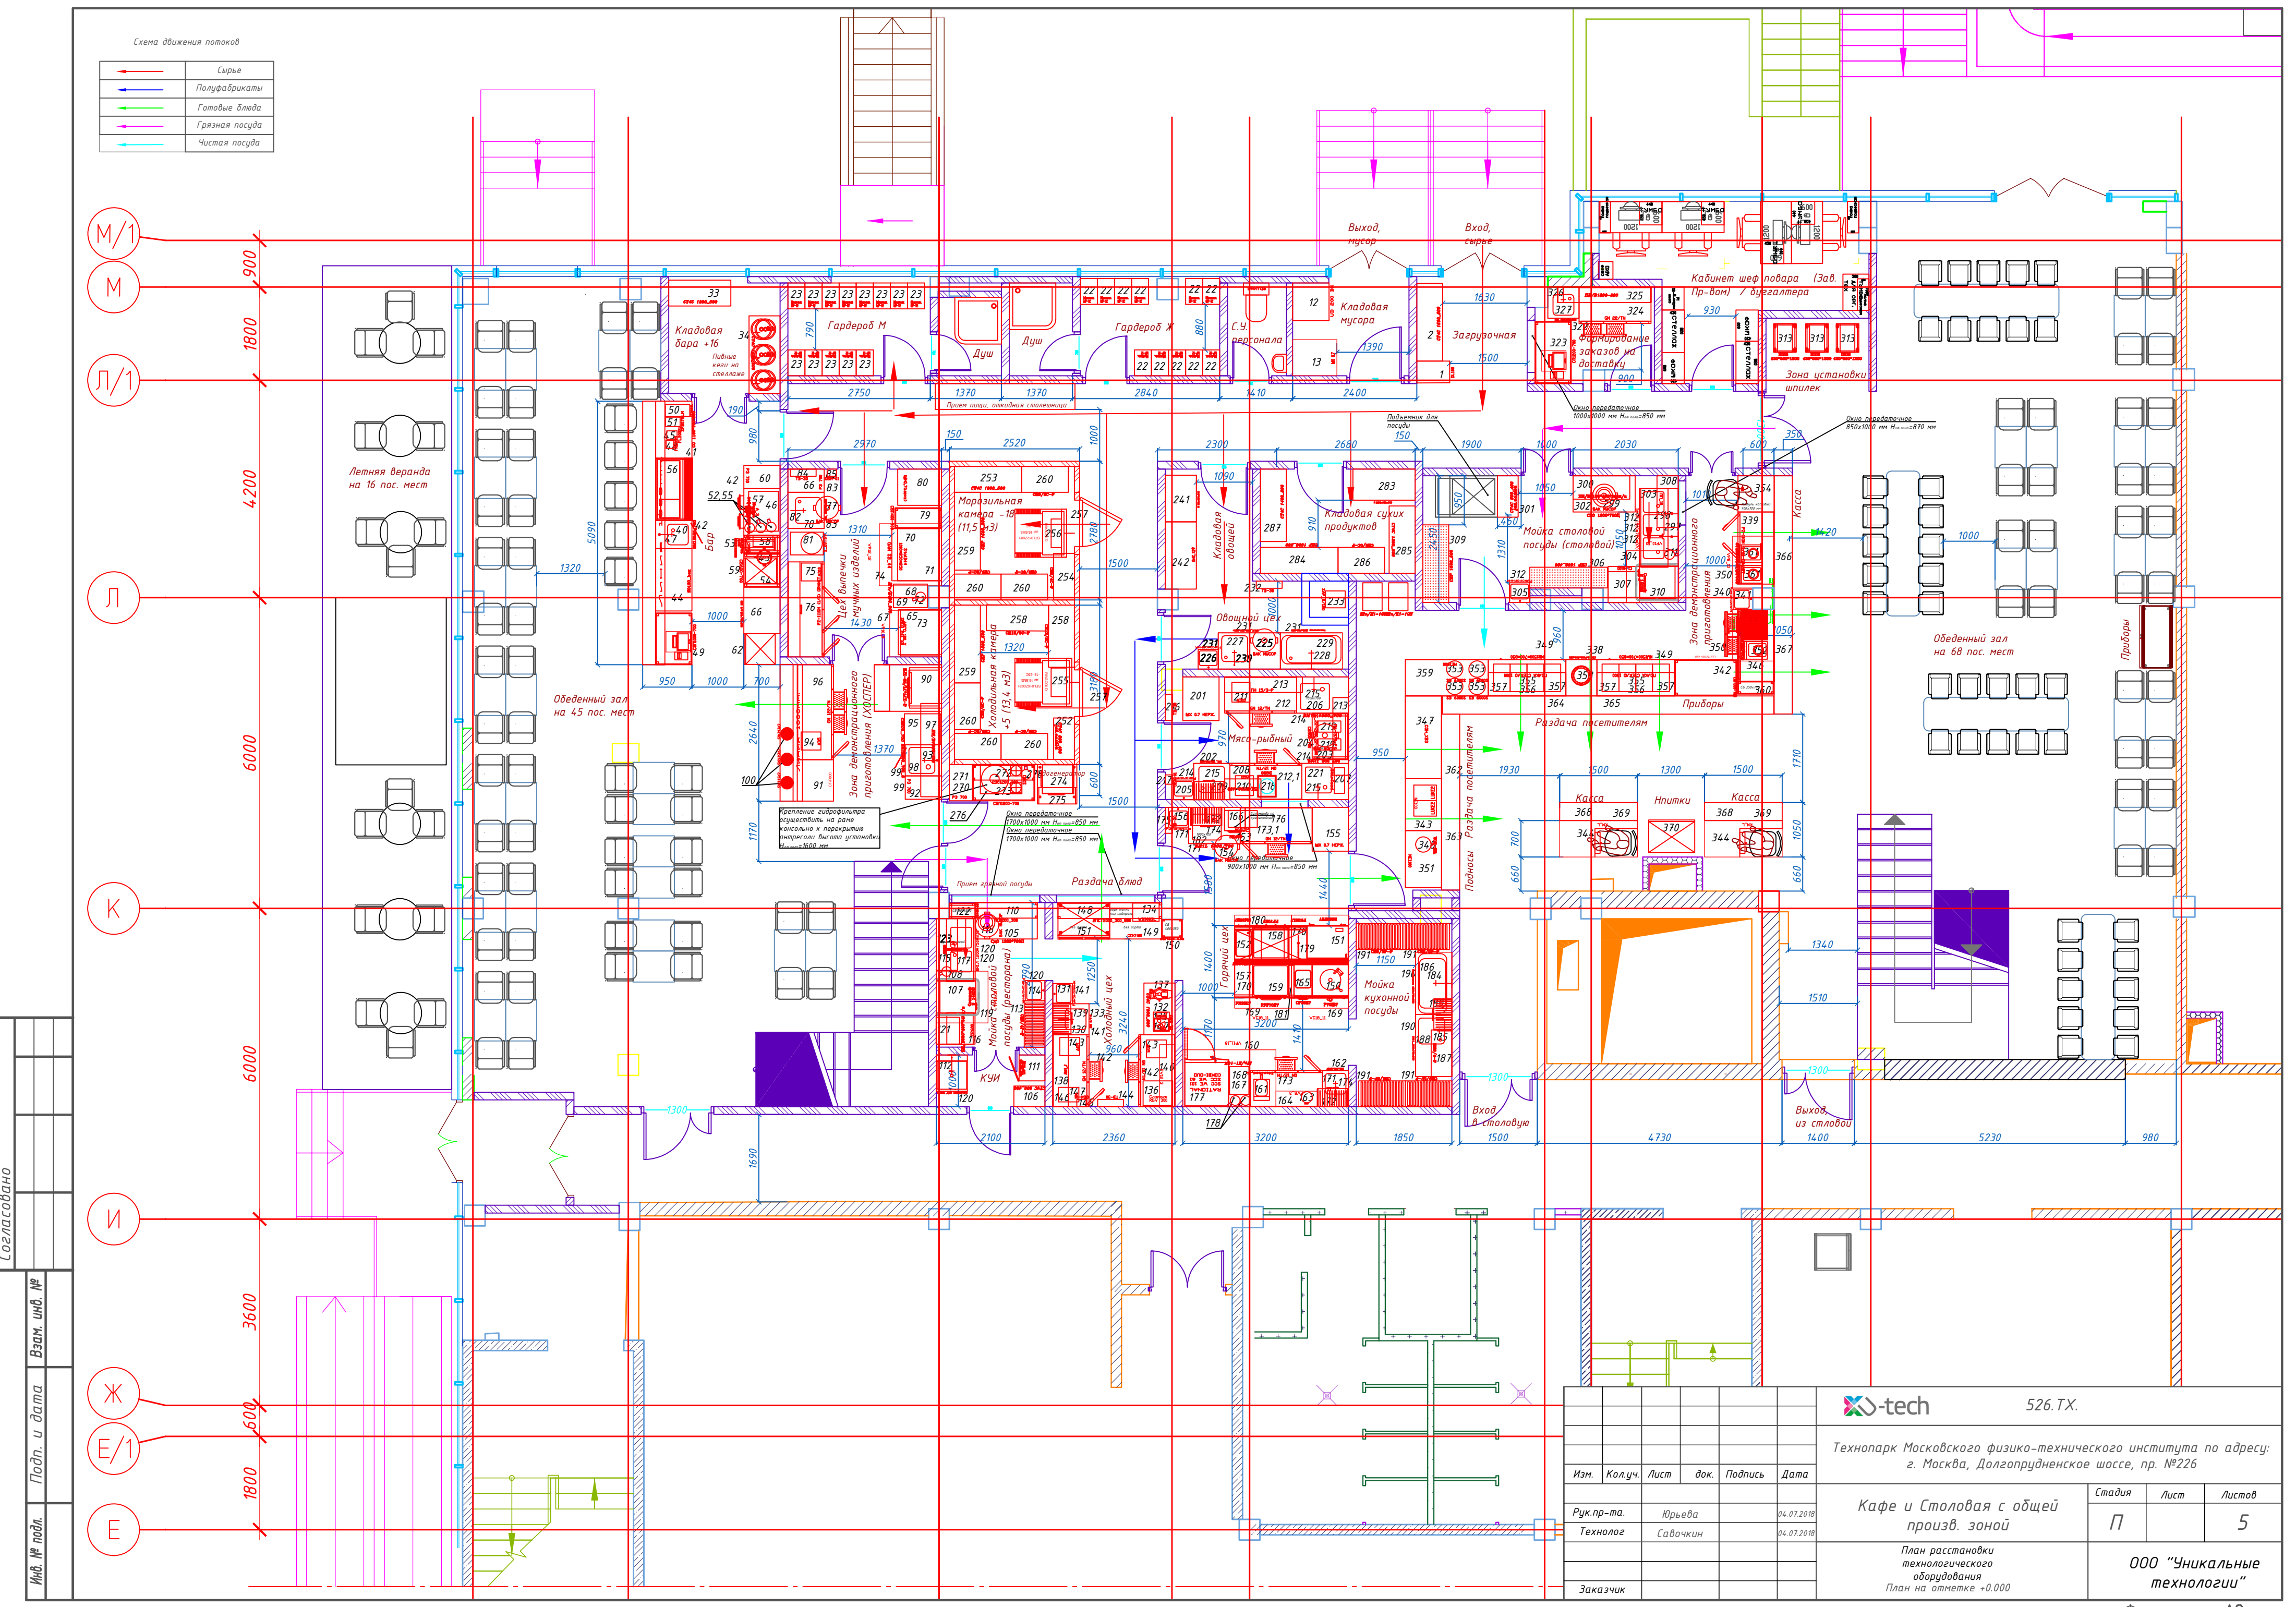

					526.ТХ.		
Технопарк Московского физико-технического института по адресу: г. Москва, Долгопрудненское шоссе, пр. №226					Кафе и Столовая с общей произв. зоной		
Изм.	Колуч.	Лист	док.	Подпись	Дата	Стадия	Лист
Рук.пр-та.	Юрьева	04.07.2018				П	5
Технолог	Савочкин	04.07.2018				000 "Уникальные технологии"	
Заказчик						Формат А2	


Согласовано

Инд. № подл. Подп. и дата Взам. инд. №

Схема движения потоков

	Сырье
	Полуфабрикаты
	Готовые блюда
	Грязная посуда
	Чистая посуда

Вход для персонала,
погрузка/разгрузка

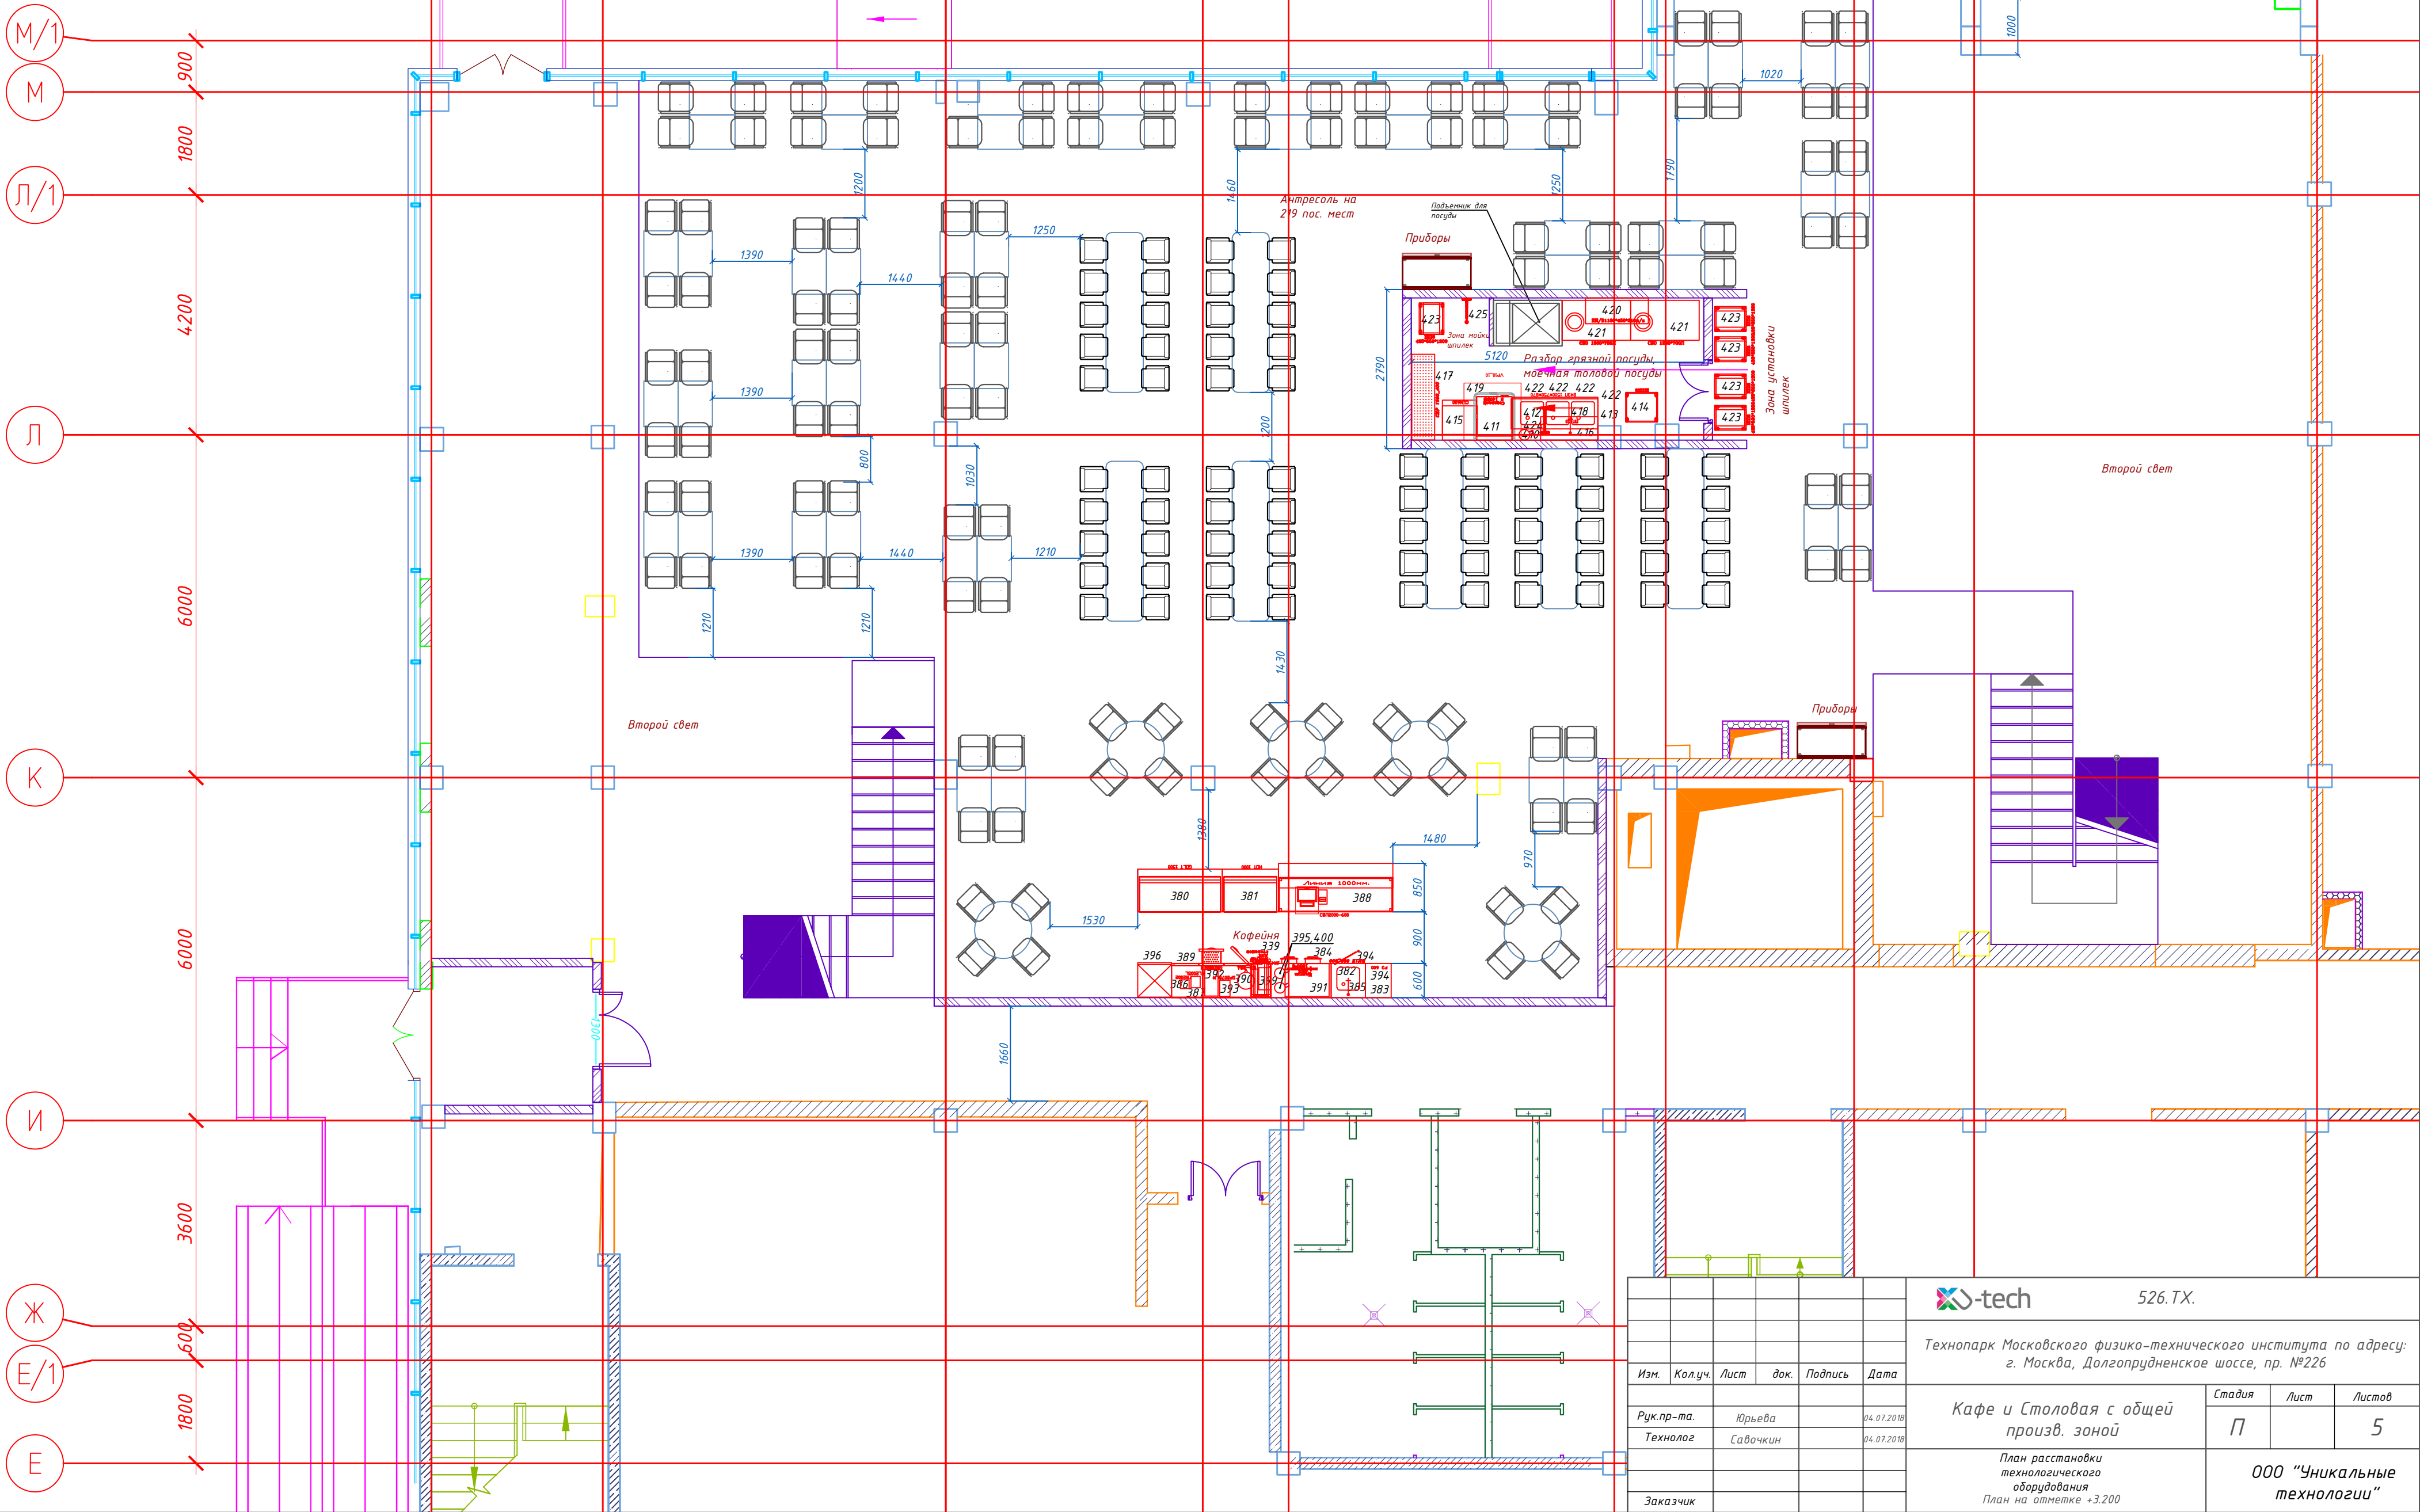

tech

526.ТХ.

Технопарк Московского физико-технического института по адресу:
г. Москва, Долгопрудненское шоссе, пр. №226

Кафе и Столовая с общей
произв. зоной

План расстановки
технологического
оборудования
План на отметке +3.200

Стадия	Лист	Листов
П		5

ООО "Уникальные
технологии"

Формат А2

Вход для персонала,
погрузка/разгрузка

Условные обозначения

Э – подвод электроэнергии
Ф – фазность тока
Р – однофазная розетка с заземлением
ШР – штепсельная розетка с рабочим нулем и заземлением
h – высота подводов от чистого пола в мм
L – длина свободного провода в мм
380В / 220В – напряжение в сети
* – условное значение предполагаемого оборудования, перед подключением обязательно смотреть паспорт производителя

Примечания

- Прокладка электросетей должна осуществляться в плоскости стен и пола, согласно требованиям ПУЭ по трёх или пятипроводной схеме, в зависимости от подключаемого технологического оборудования
- В случае подключения оборудования путём ввода кабеля напрямую, без установки разъёма, необходим выход МЯГКОГО (МНОГОЖИЛЬНОГО) кабеля, длиной 2500мм, согласно заданным высотам
- Установленные силовые разъёмы необходимо укомплектовать ответной частью.
- Установленная суммарная потребляемая мощность по технологическому оборудованию составит согласно спецификации оборудования 241,625кВт/час.

tech

526.TX.

Технопарк Московского физико-технического института по адресу:
г. Москва, Долгопрудненское шоссе, пр. №226

Кафе и Столовая с общей
произв. зоной

План расположения
электропроводов
План на отметке +3.200


Стадия	Лист	Листов
П		5

ООО "Уникальные
технологии"

Формат А2

Согласовано

Инд. № подл.	Подп. и дата	Взам. инд. №

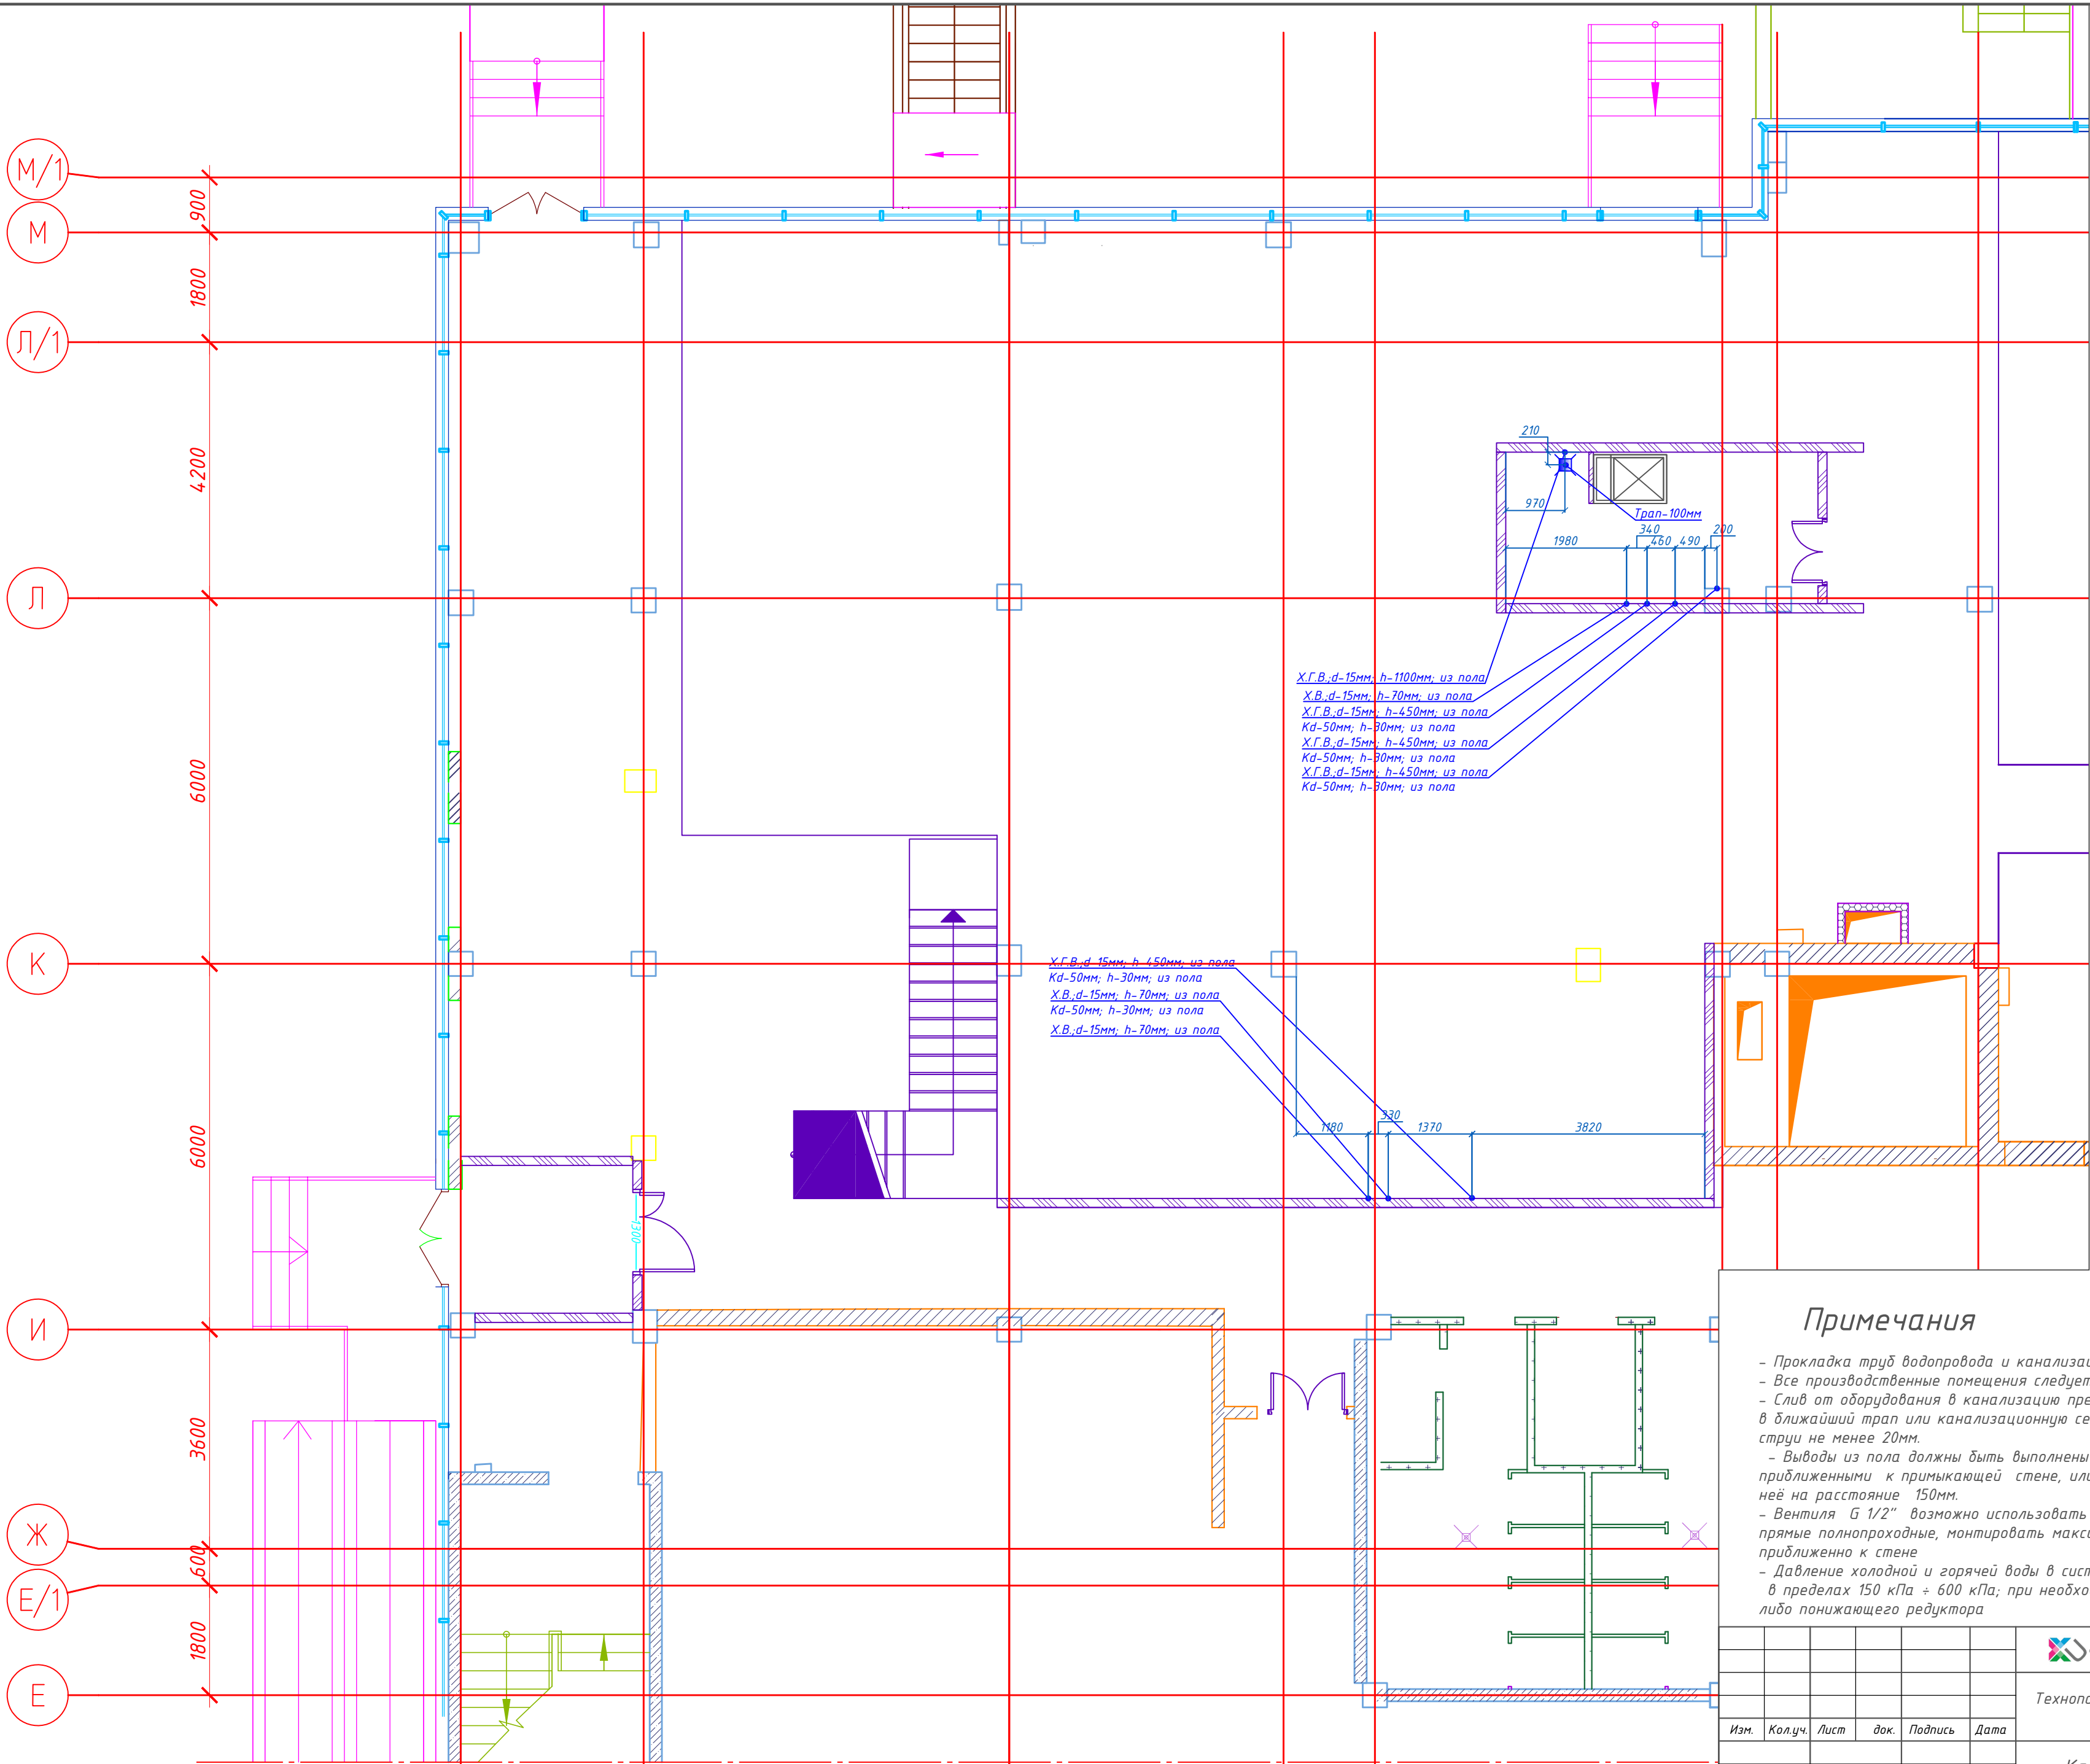

Х.Г.В. d-15мм, h-1100мм, из пола
Х.В. d-15мм, h-70мм, из пола
Х.Г.В. d-15мм, h-450мм, из пола
Кд-50мм, h-30мм, из пола
Х.Г.В. d-15мм, h-450мм, из пола
Кд-50мм, h-30мм, из пола
Х.Г.В. d-15мм, h-450мм, из пола
Кд-50мм, h-30мм, из пола

Х.Г.В. d-15мм, h-450мм, из пола
Кд-50мм, h-30мм, из пола
Х.В. d-15мм, h-70мм, из пола
Кд-50мм, h-30мм, из пола
Х.В. d-15мм, h-70мм, из пола


Условные обозначения

Х.В. – подвод холодной воды
Х.Г.В. – подвод холодной и горячей воды
d – диаметр трубопровода
K – отвод в канализацию
h – высота подводов от чистого пола в мм
Трап d=100мм
Габариты трапа должны быть 500x230мм. Центр ливневки определяется привязкой указанной на плане

Примечания

- Прокладка труб водопровода и канализации должна осуществляться в плоскости стен и пола
- Все производственные помещения следует оборудовать сливными трапами.
- Слив от оборудования в канализацию предусмотреть в ближайший трап или канализационную сеть с разрывом струи не менее 20мм.
- Выходы из пола должны быть выполнены максимально приближенными к примыкающей стене, или отнесены от нее на расстояние 150мм.
- Вентили G 1/2" возможно использовать угловые или прямые полнопроходные, монтировать максимально приближенно к стене
- Давление холодной и горячей воды в системе водоснабжения в пределах 150 кПа ÷ 600 кПа; при необходимости с установкой насоса, повышающего давление либо понижающего редуктора

						526.ТХ.			
						Технопарк Московского физико-технического института по адресу: г. Москва, Долгопрудненское шоссе, пр. №226			
Изм.	Колуч.	Лист	док.	Подпись	Дата	Кафе и Столовая с общей произв. зоной	Стация	Лист	Листов
Рук.пр-та.		Юрьева			04.07.2018		П		5
Технолог		Савочкин			04.07.2018				
Заказчик									
						План расположения выводов воды и канализации План на отметке +3.200			
						ООО "Уникальные технологии"			
						Формат А2			

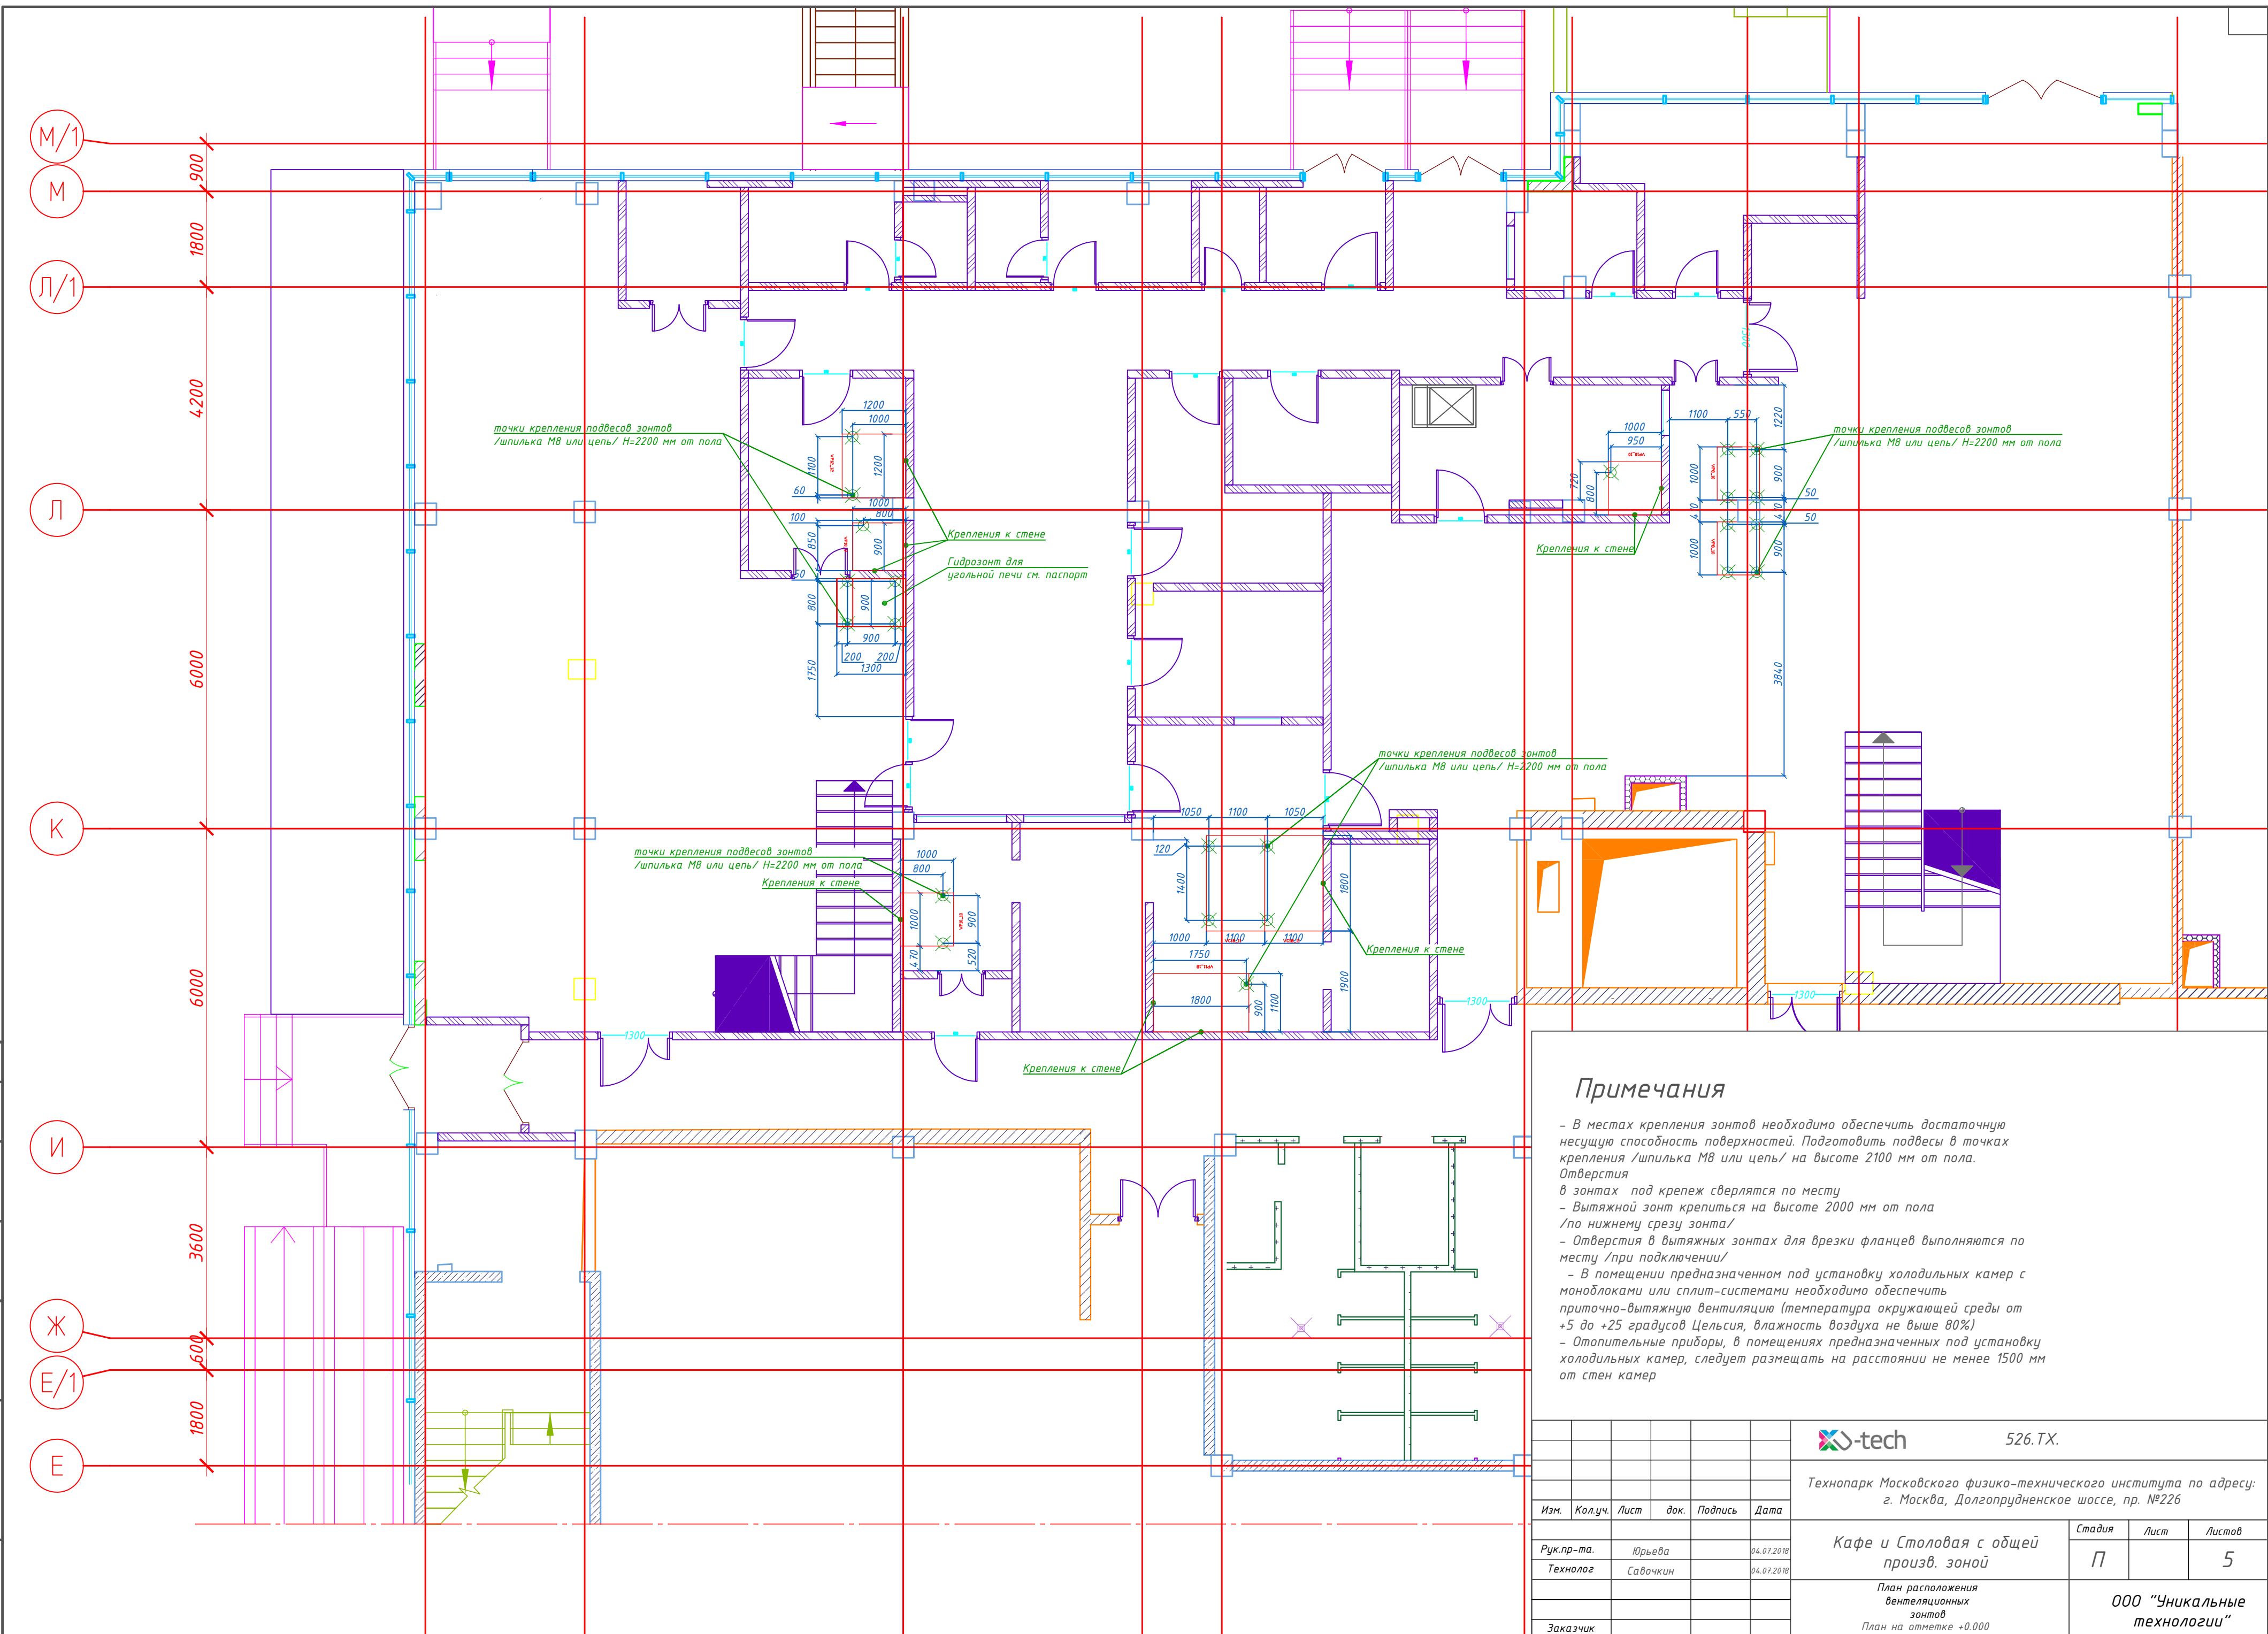[illegible]


Примечания

- В местах крепления зонтов необходимо обеспечить достаточную несущую способность поверхности. Подготовить подвесы в точках крепления /шпилька М8 или цепь/ на высоте 2100 мм от пола. Отверстия
 - в зонтах под крепеж сверлятся по месту
 - Выхажной зонт крепиться на высоте 2000 мм от пола /по нижней срезу зонта/
 - Отверстия в выхажных зонтах для врезки фланцев выполняются по месту /при подключении/
 - В помещениях предназначенном под установку холодильных камер с моноблоками или сплит-системами необходимо обеспечить приточно-вытяжную вентиляцию (температура окружающей среды от +5 до +25 градусов Цельсия, влажность воздуха не выше 80%)
 - Отопительные приборы, в помещениях предназначенных под установку холодильных камер, следует размещать на расстоянии не менее 1500 мм от стен камер

						 526.TX.
						Технопарк Московского физико-технического института по адресу: г. Москва, Долгопрудненское шоссе, пр. №226
Изм.	Колуч.	Лист	док.	Подпись	Дата	
Рук.пр-та.		Юрьева			04.07.2018	Кафе и Столовая с общей произв. зоной
Технолог		Савочкин			04.07.2018	
Заказчик						План расположения вентиляционных зонтов План на отметке +0.000
						Стадия
						Лист
						Листов
						П
						5
						000 "Уникальные технологии"

Согласовано

Инд. № подл.	Подп. и дата	Взам. инд. №

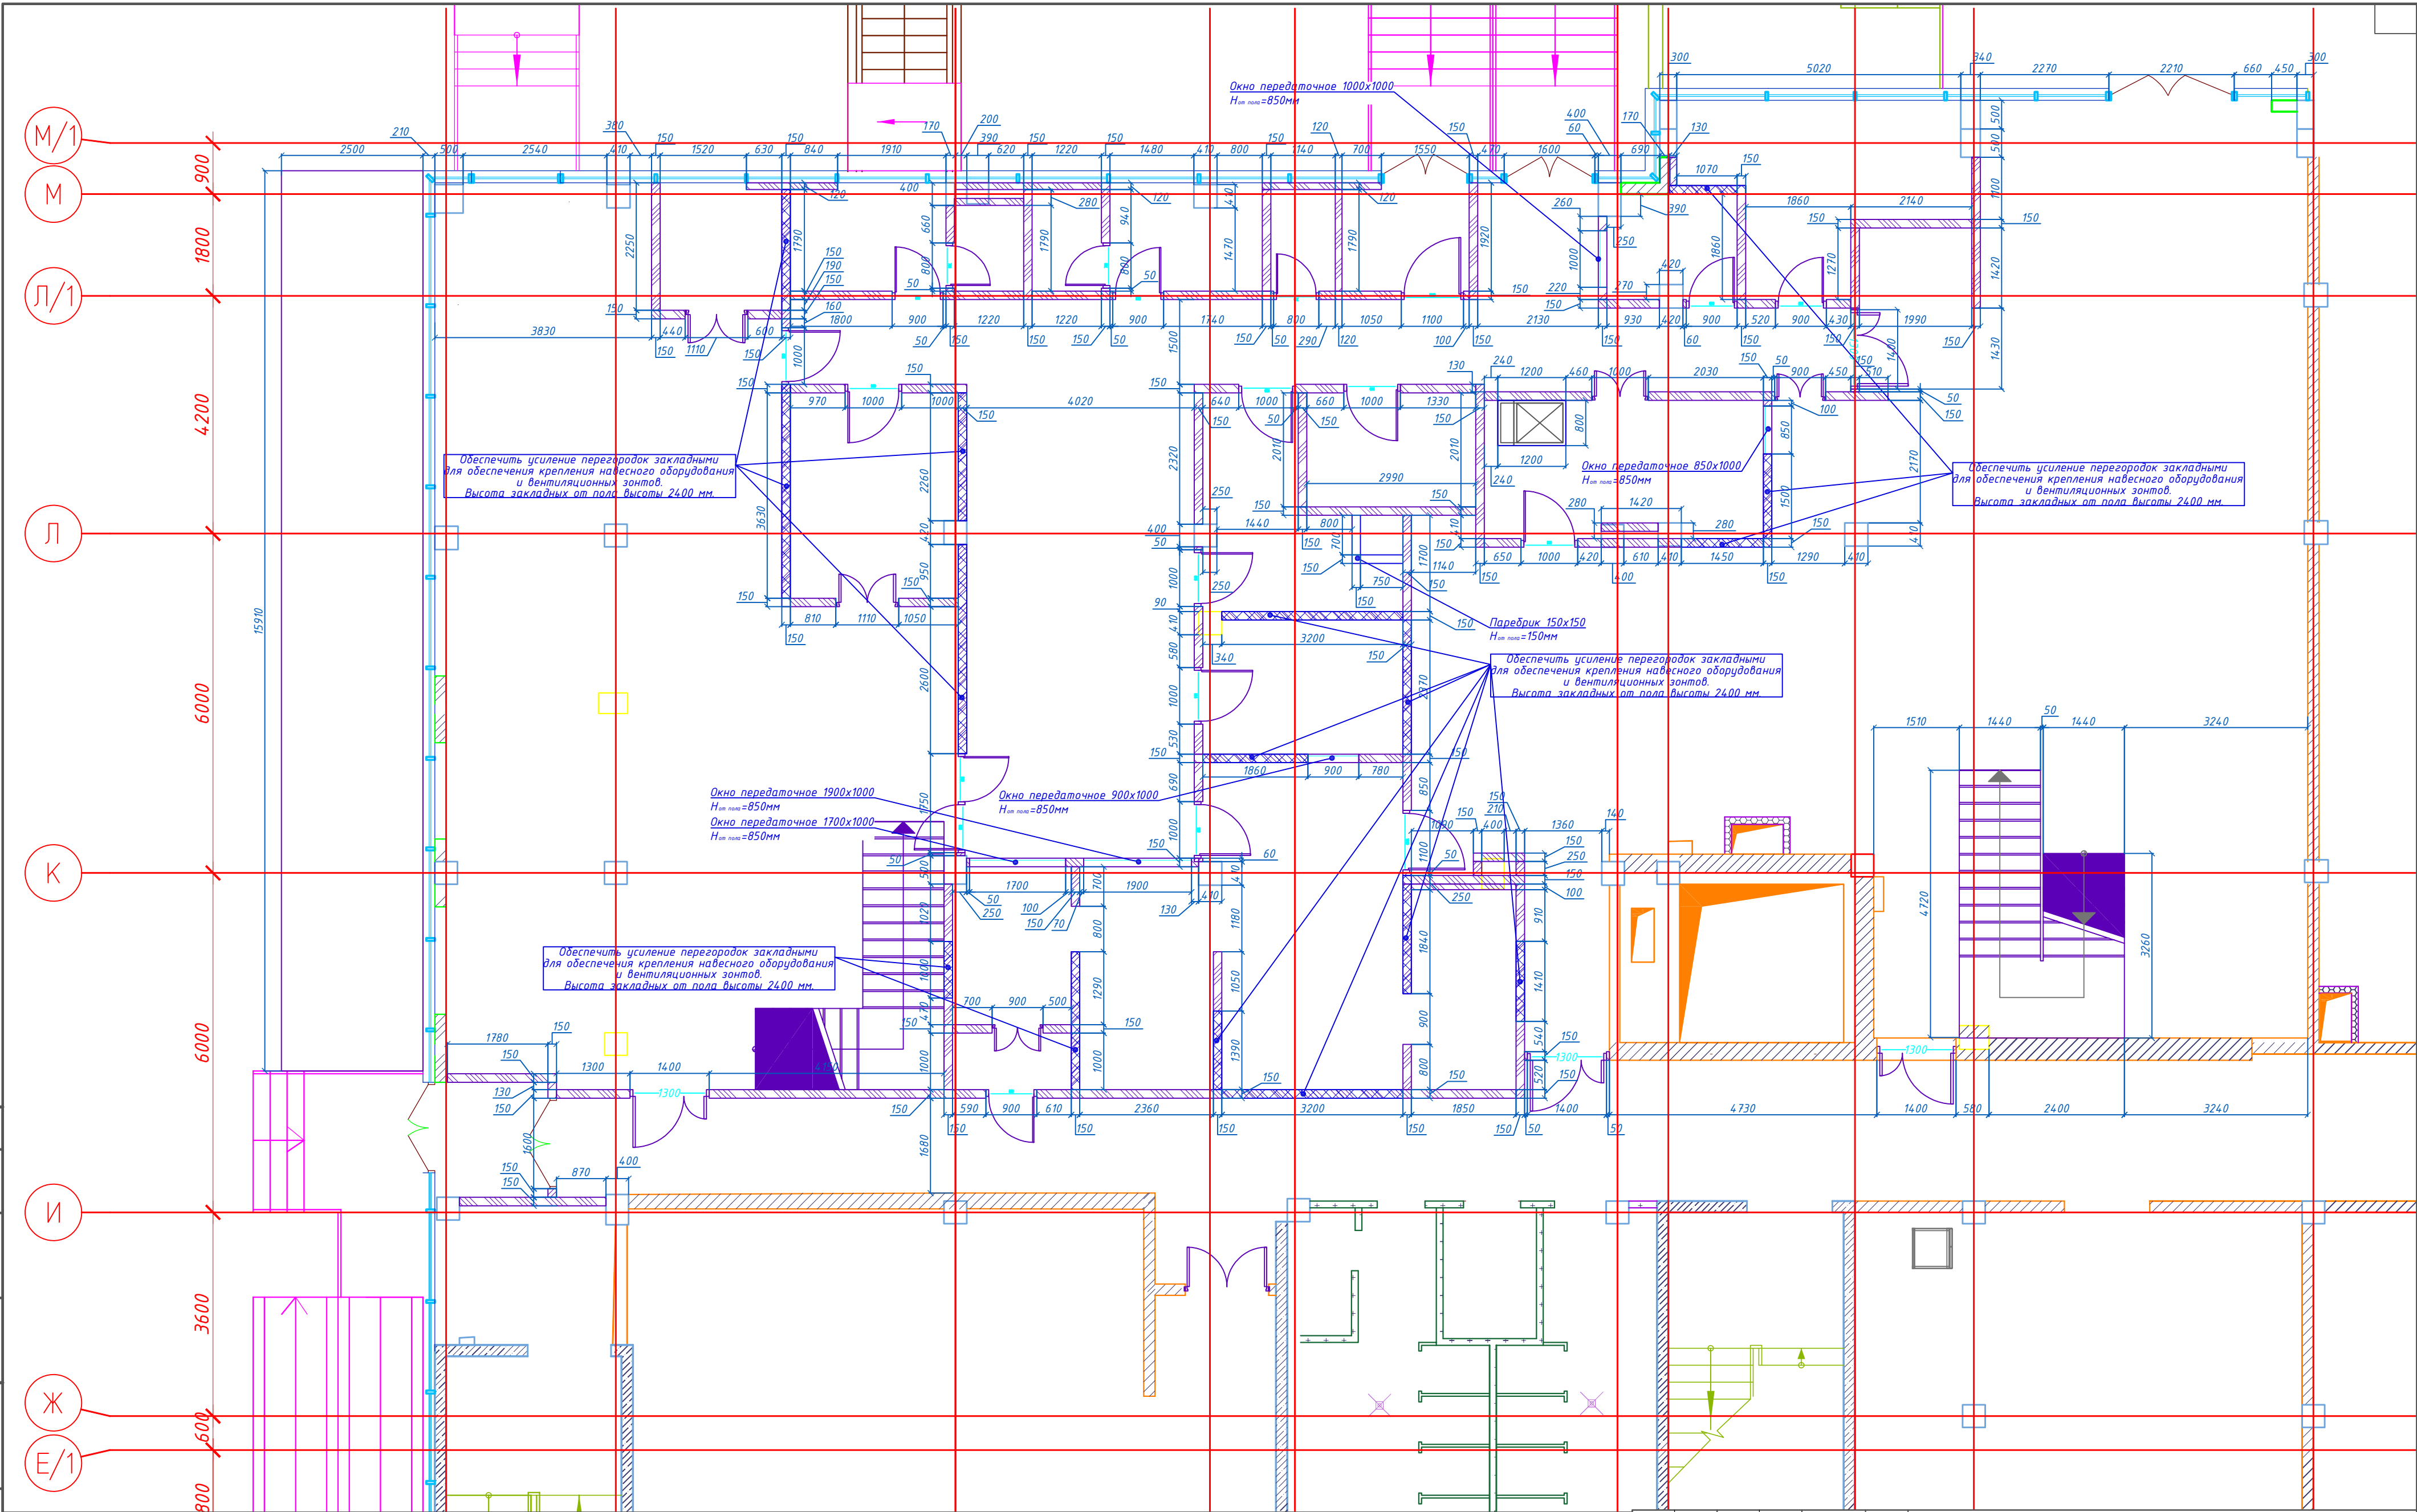


Примечания

- Толщина перегородок в помещениях принята 150 мм;
- Все размеры указаны в мм от чистого пола и стен.
- полы должны быть строго горизонтальными, уклон полов не более +/- 5 мм относительно нулевой линии на длине 2 м.
- Необходимо предусмотреть требуемые размеры дверных проёмов для обеспечения заноса оборудования в помещения.
- Для установки навесного оборудования (полок, панелей, пристенных и центральных вентиляционных зонтов) требуется предусмотреть закладные элементы, обеспечивающие надёжное крепление вышеуказанного оборудования.

						526.ТХ.			
						Технопарк Московского физико-технического института по адресу: г. Москва, Долгопрудненское шоссе, пр. №226			
Изм.	Колуч.	Лист	док.	Подпись	Дата	Кафе и Столовая с общей произв. зоной	Стадия	Лист	Листов
Рук.пр-та.	Юрьева	04.07.2018					П		5
Технолог	Савочкин	04.07.2018							
Заказчик									
						План расположения перегородок План на отметке +0.000			
						ООО "Уникальные технологии"			
						Формат А2			

*Вход для персонала,
погрузка/разгрузка*

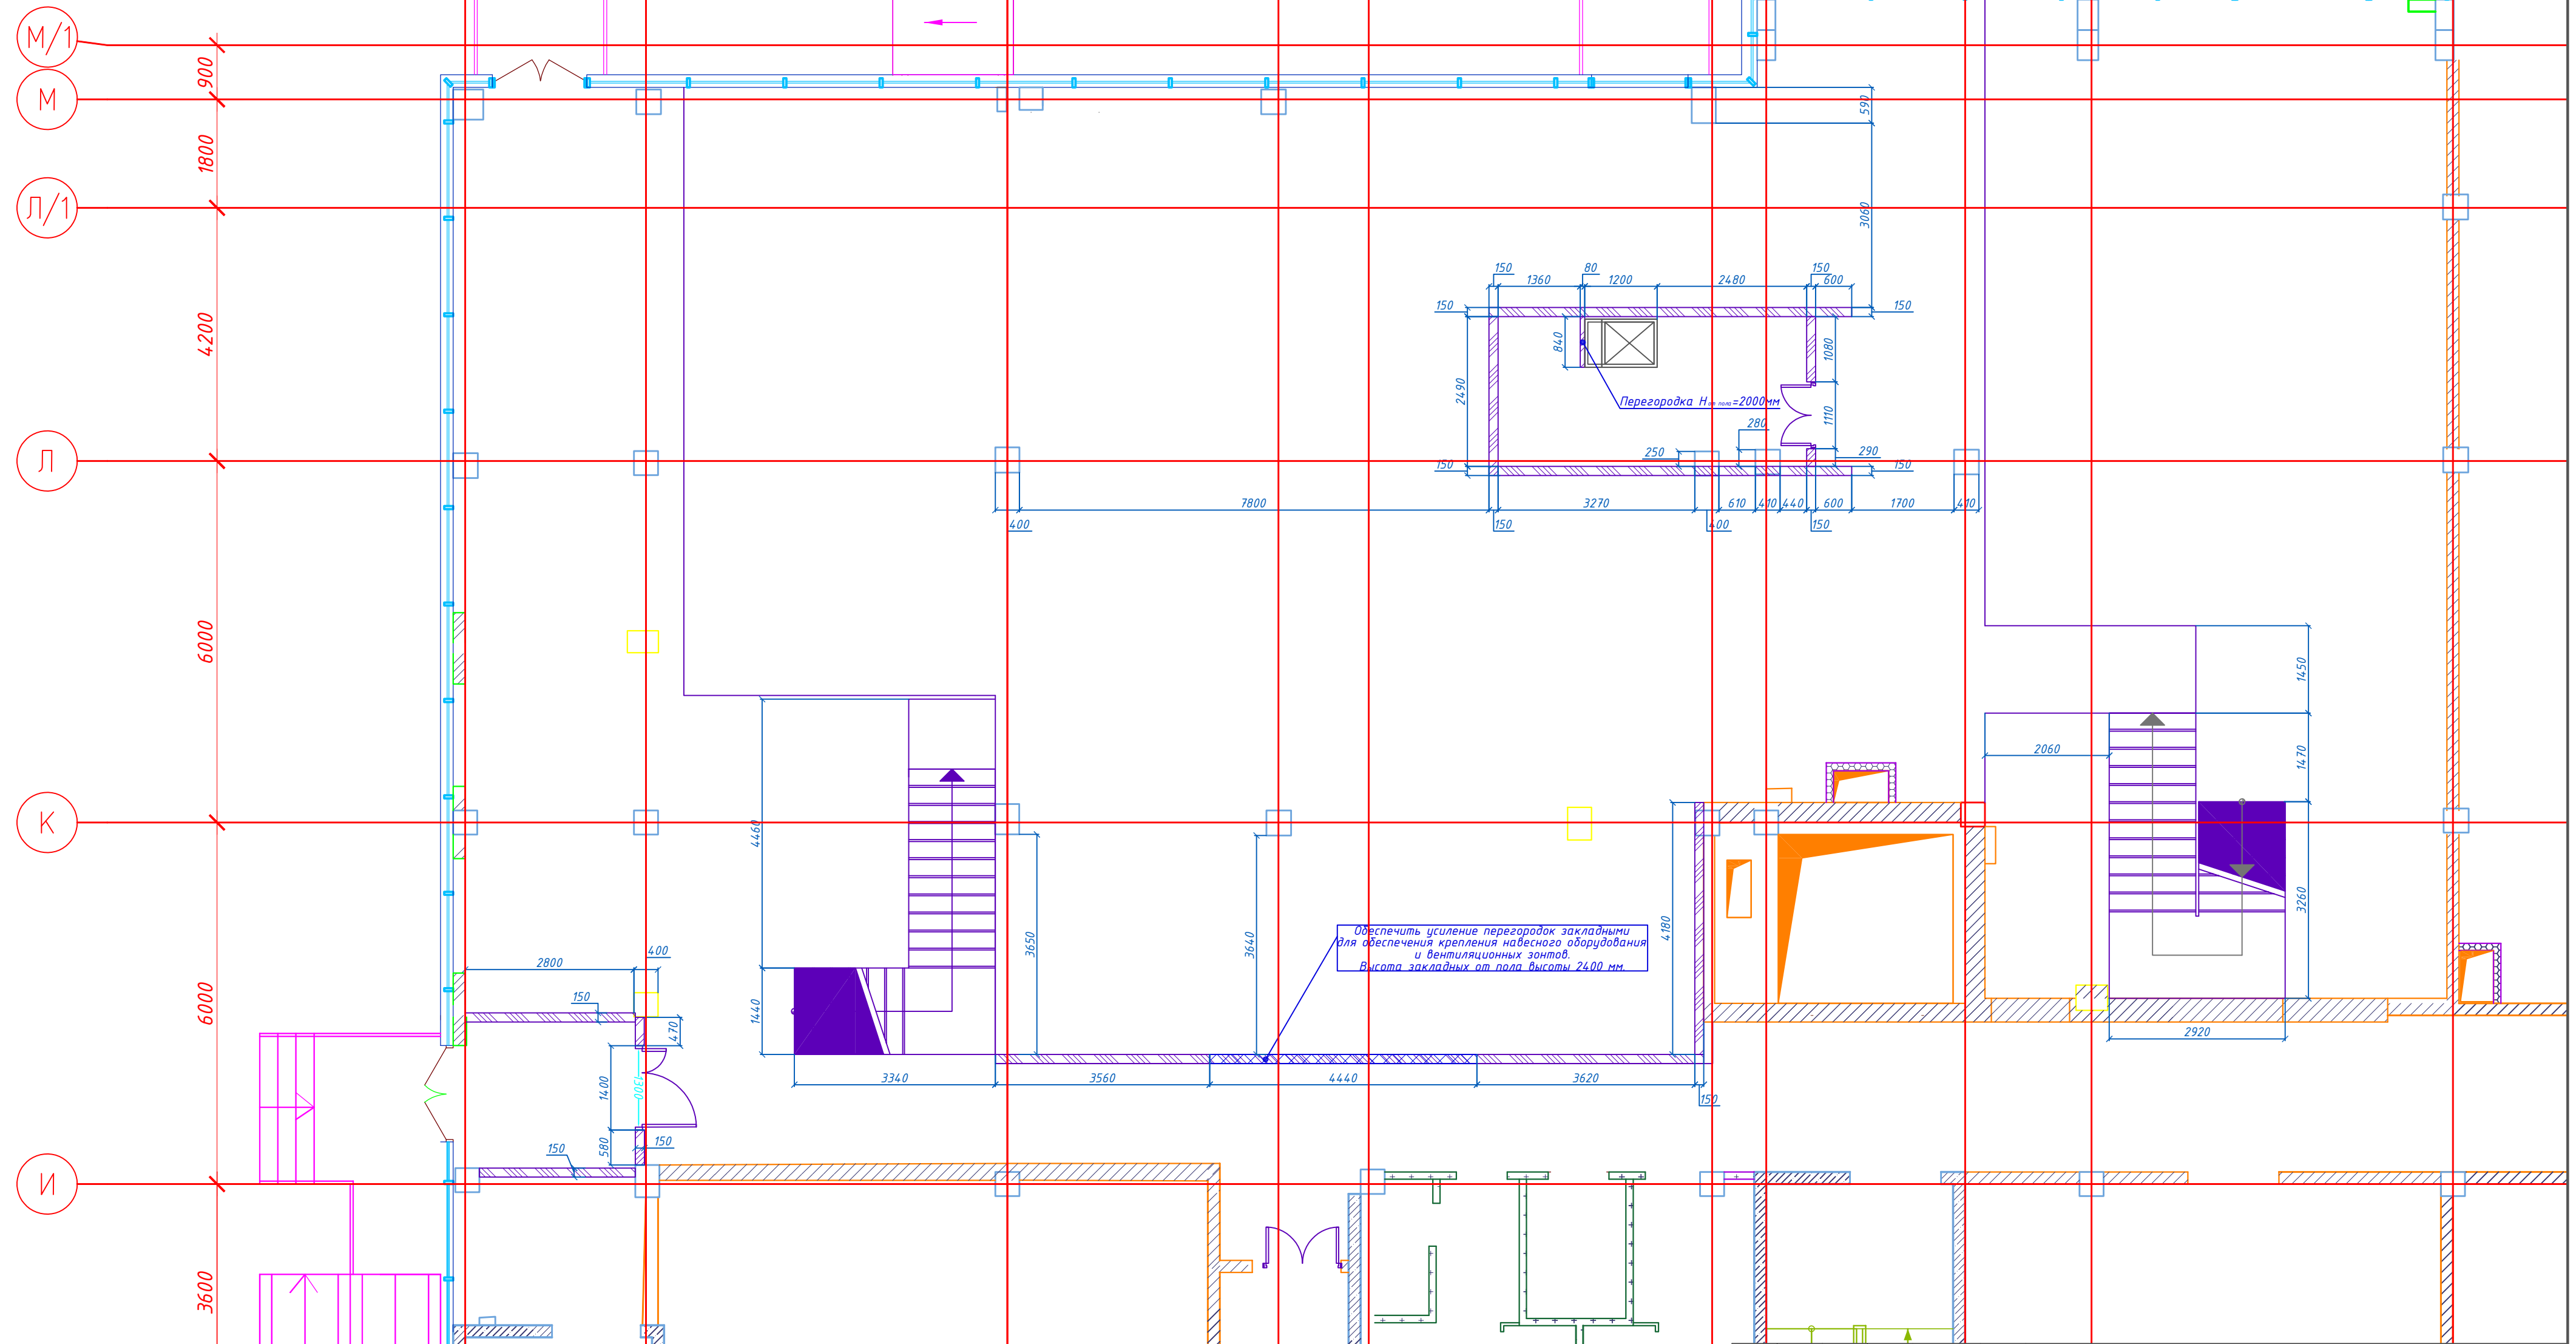

Примечания

- Толщина перегородок в помещениях принята 150 мм;
- Все размеры указаны в мм от чистого пола и стен.
- полы должны быть строго горизонтальными, уклон полов не более +/- 5 мм относительно нулевой линии на длине 2 м.
- Необходимо предусмотреть требуемые размеры дверных проёмов для обеспечения заноса оборудования в помещения.
- Для установки навесного оборудования (полок, панелей, пристенных и центральных вентиляционных зонтов) требуется предусмотреть закладные элементы, обеспечивающие надёжное крепление вышеуказанного оборудования.

						 526 ТХ.
						Технопарк Московского физико-технического института по адресу: г. Москва, Долгопрудненское шоссе, пр. №226
Изм.	Кол.уч.	Лист	док.	Подпись	Дата	
Рук.пр-та.		Юрьева			04.07.2018	Кафе и Столовая с общей произв. зоной П Лист Листов 5
Технолог		Савочкин			04.07.2018	
						План расположения перегородок План на отметке +3.200 ООО "Уникальные технологии"
Заказчик						