


3 вариант

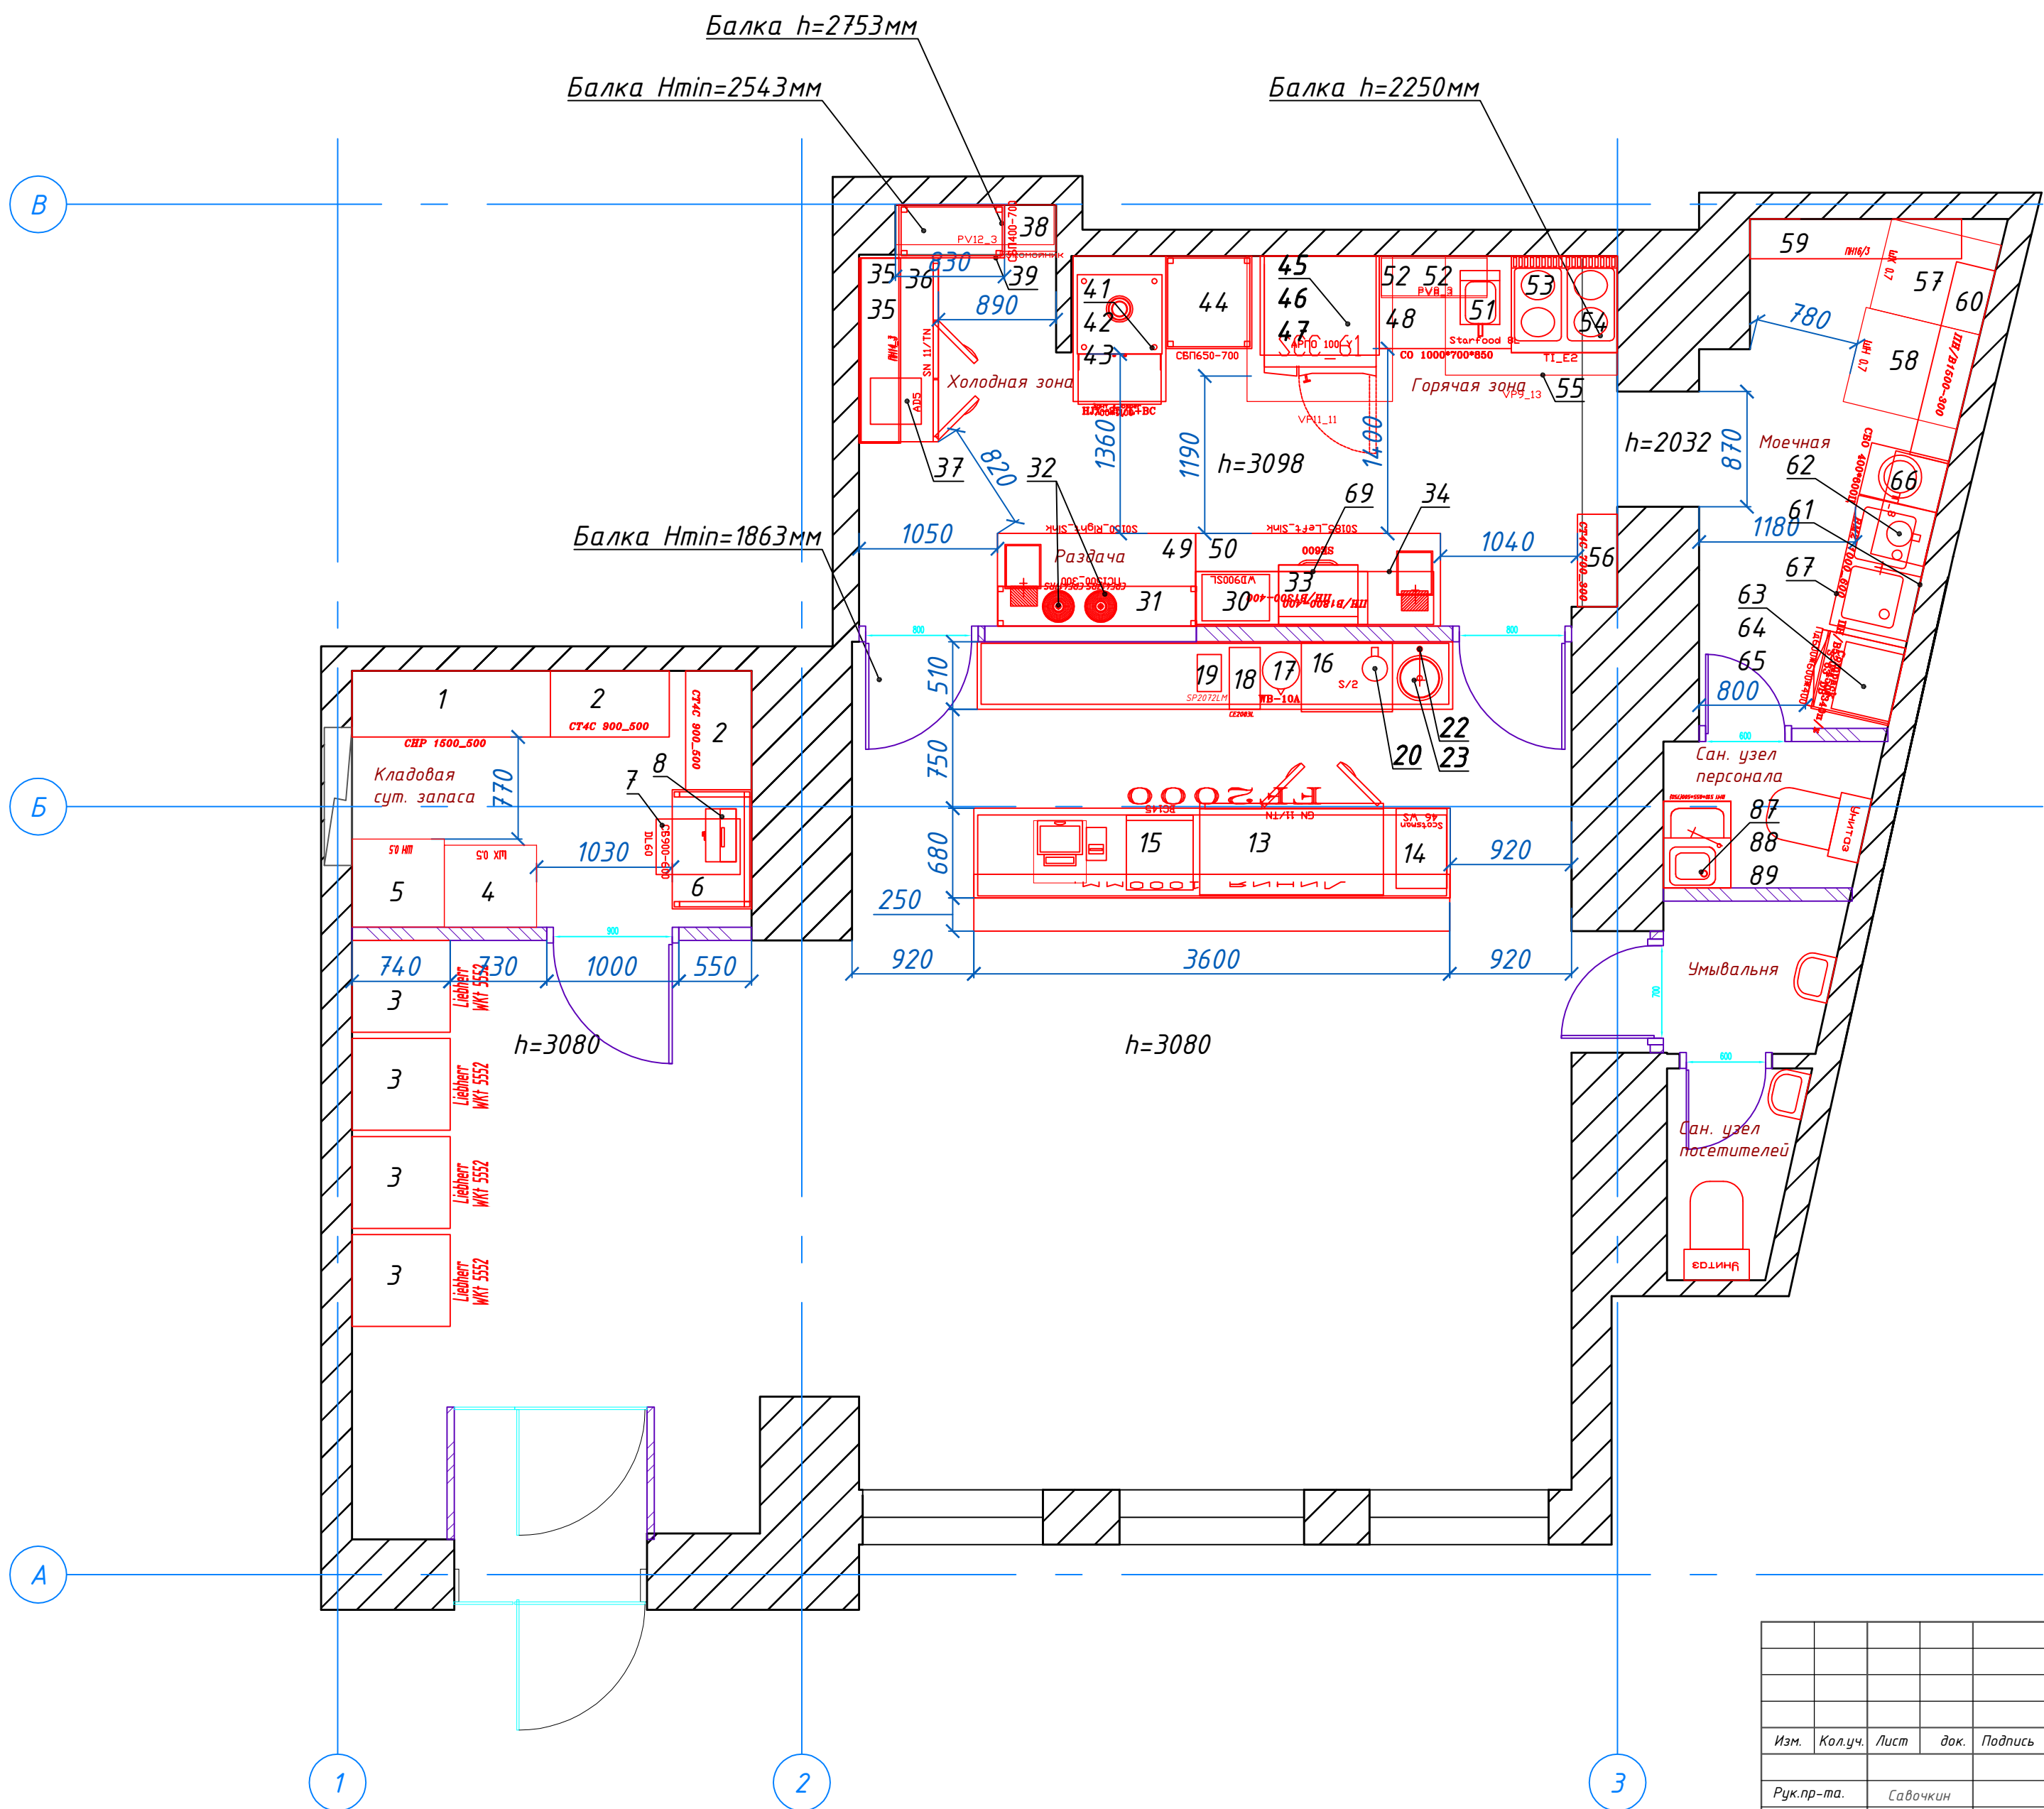


Масштаб 1:40

606.TX					
Г.Москва, Б. Никитская, д.19/13					
Изм.	Колуч.	Лист	док.	Подпись	Дата
Рук.пр-та.	Савочкин				01.08.2018
Технолог	Скрипкин				01.08.2018
Проверил	Савочкин				01.08.2018
Заказчик					
Кафе на 40 пос. мест				Стадия	Лист
План расстановки технологического оборудования План на отметке +0.000				РД	5

Согласовано

Инд. № подл. Подп. и дата Взам. инд. №


3 вариант

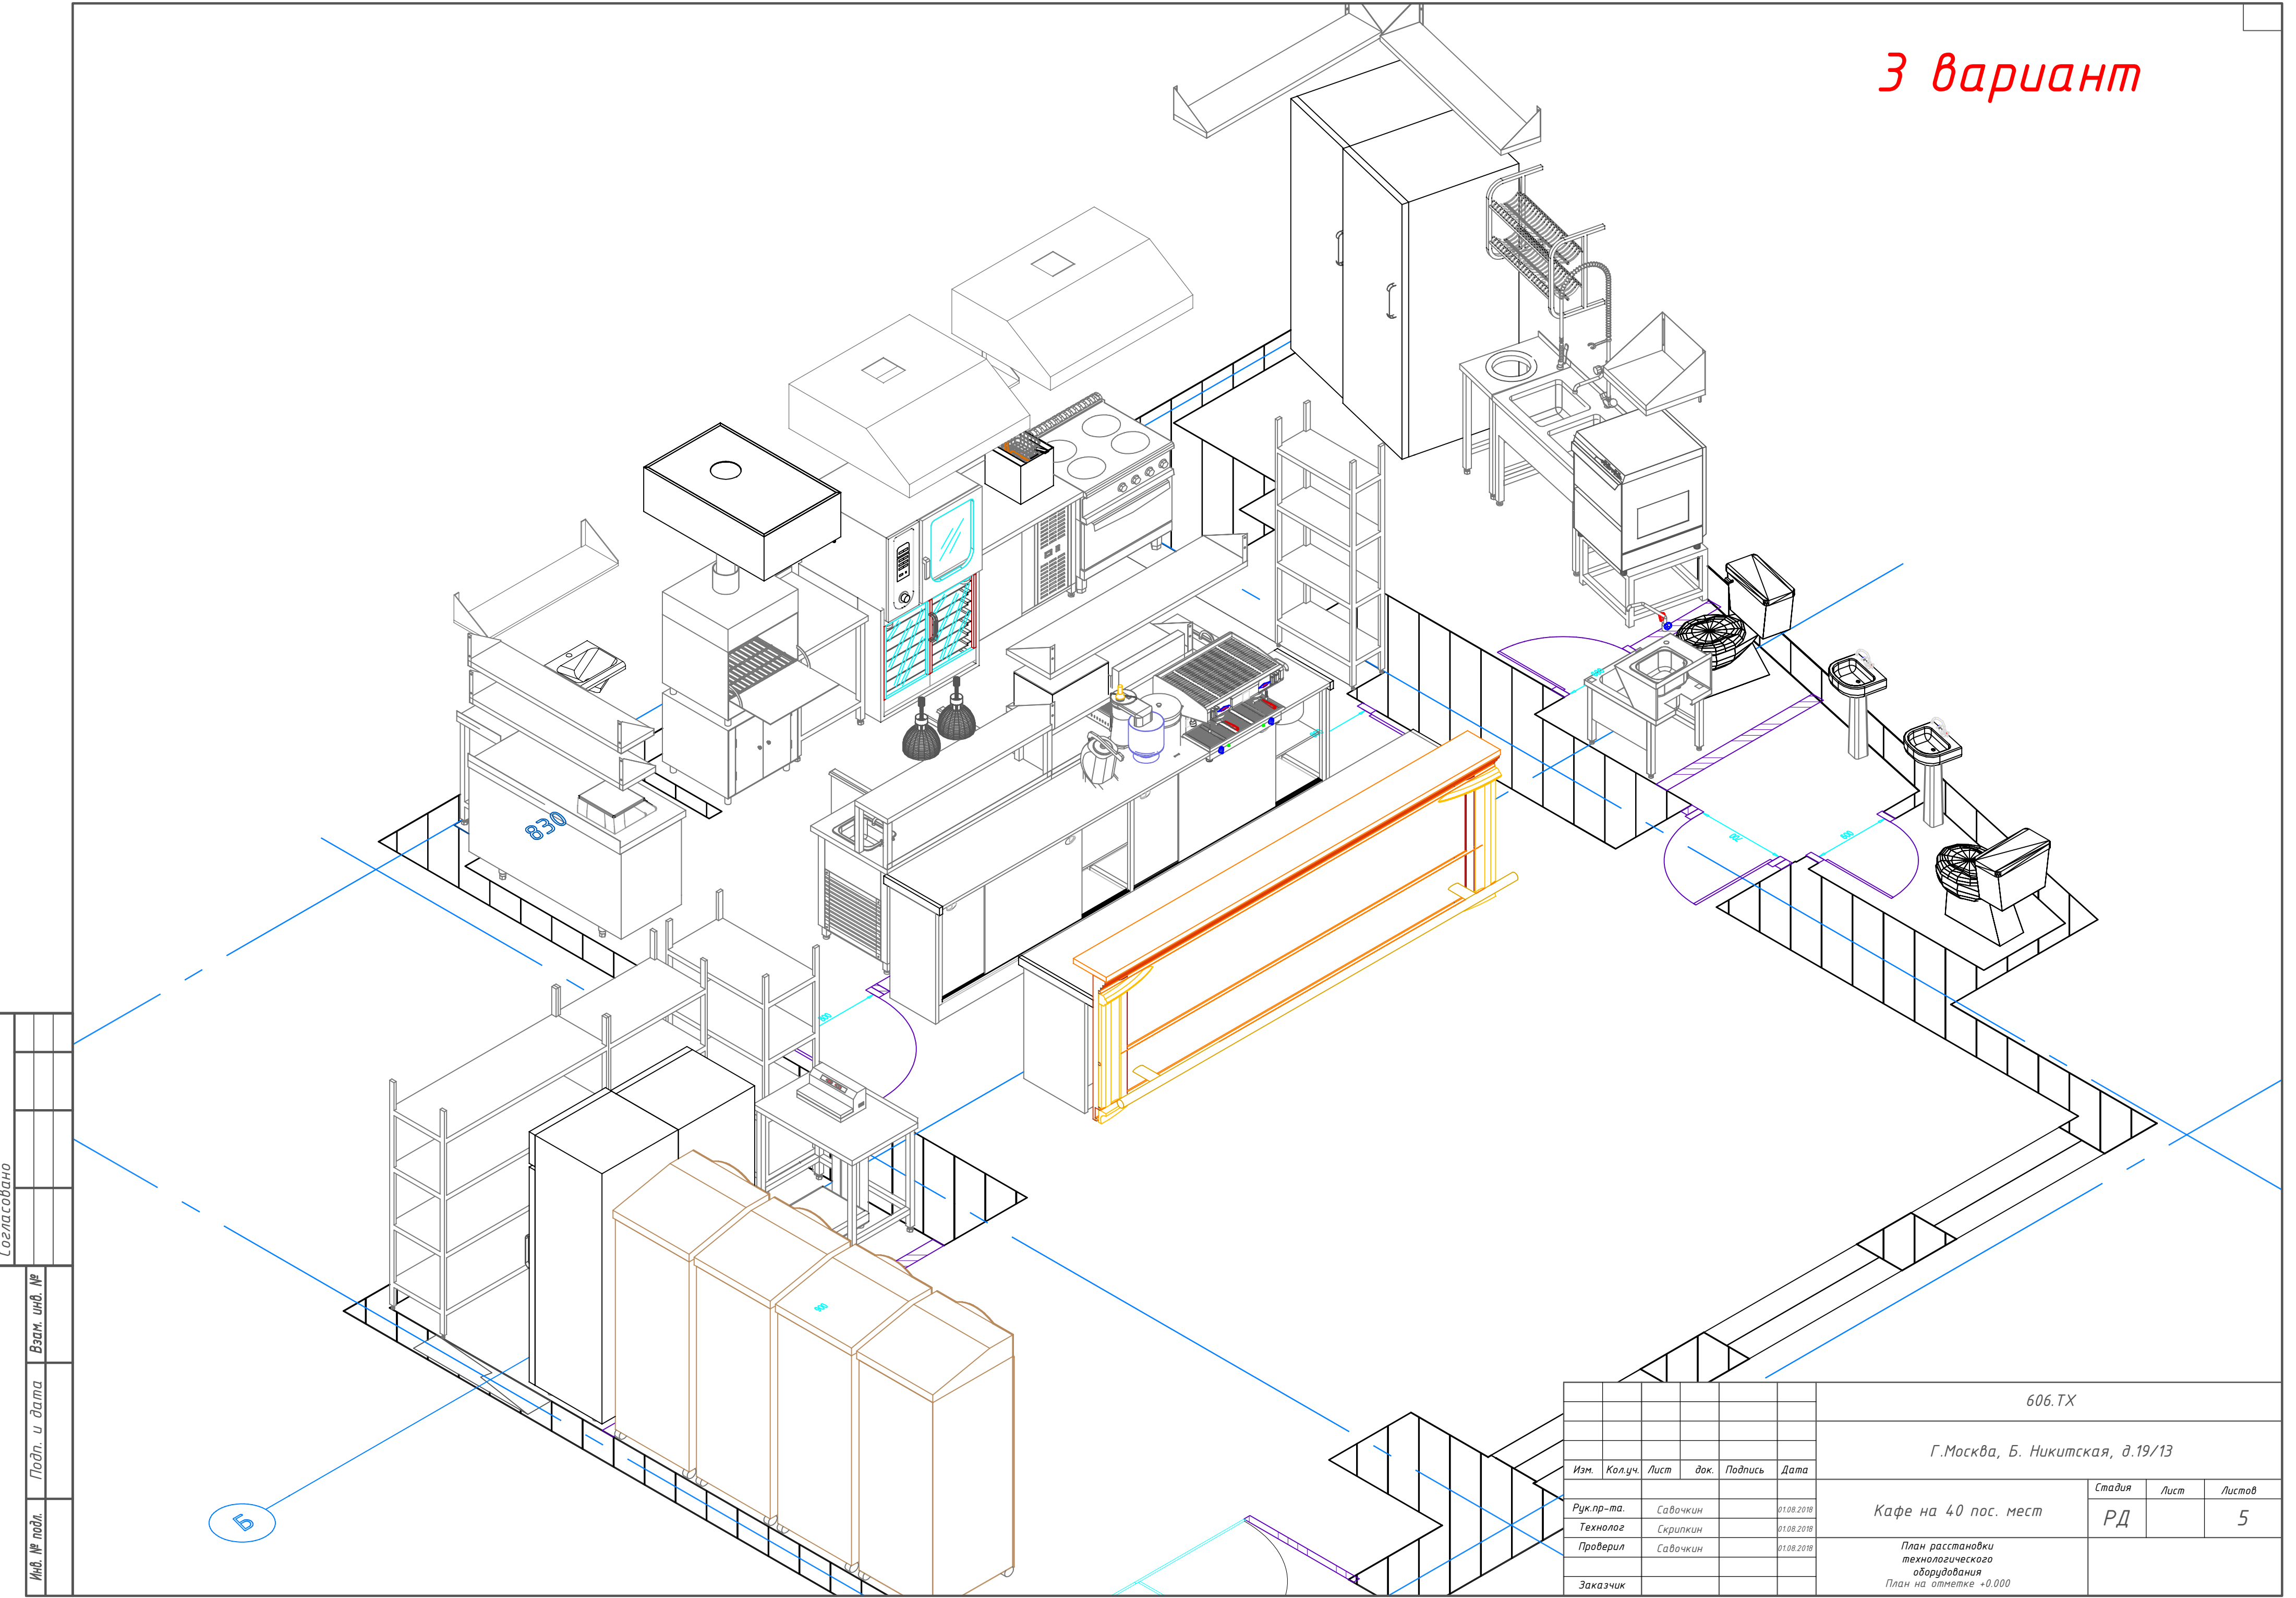

Согласовано			
Инд. № подл.	Подп. и дата	Взам. инд. №	

						606.ТХ			
						Г.Москва, Б. Никитская, д.19/13			
Изм.	Колуч.	Лист	док.	Подпись	Дата	Кафе на 40 пос. мест	Стадия	Лист	Листов
Рук.пр-та.	Савочкин				01.08.2018		РД		5
Технолог	Скрипкин				01.08.2018				
Проверил	Савочкин				01.08.2018				
Заказчик									
						План расстановки технологического оборудования План на отметке +0.000			

3 вариант

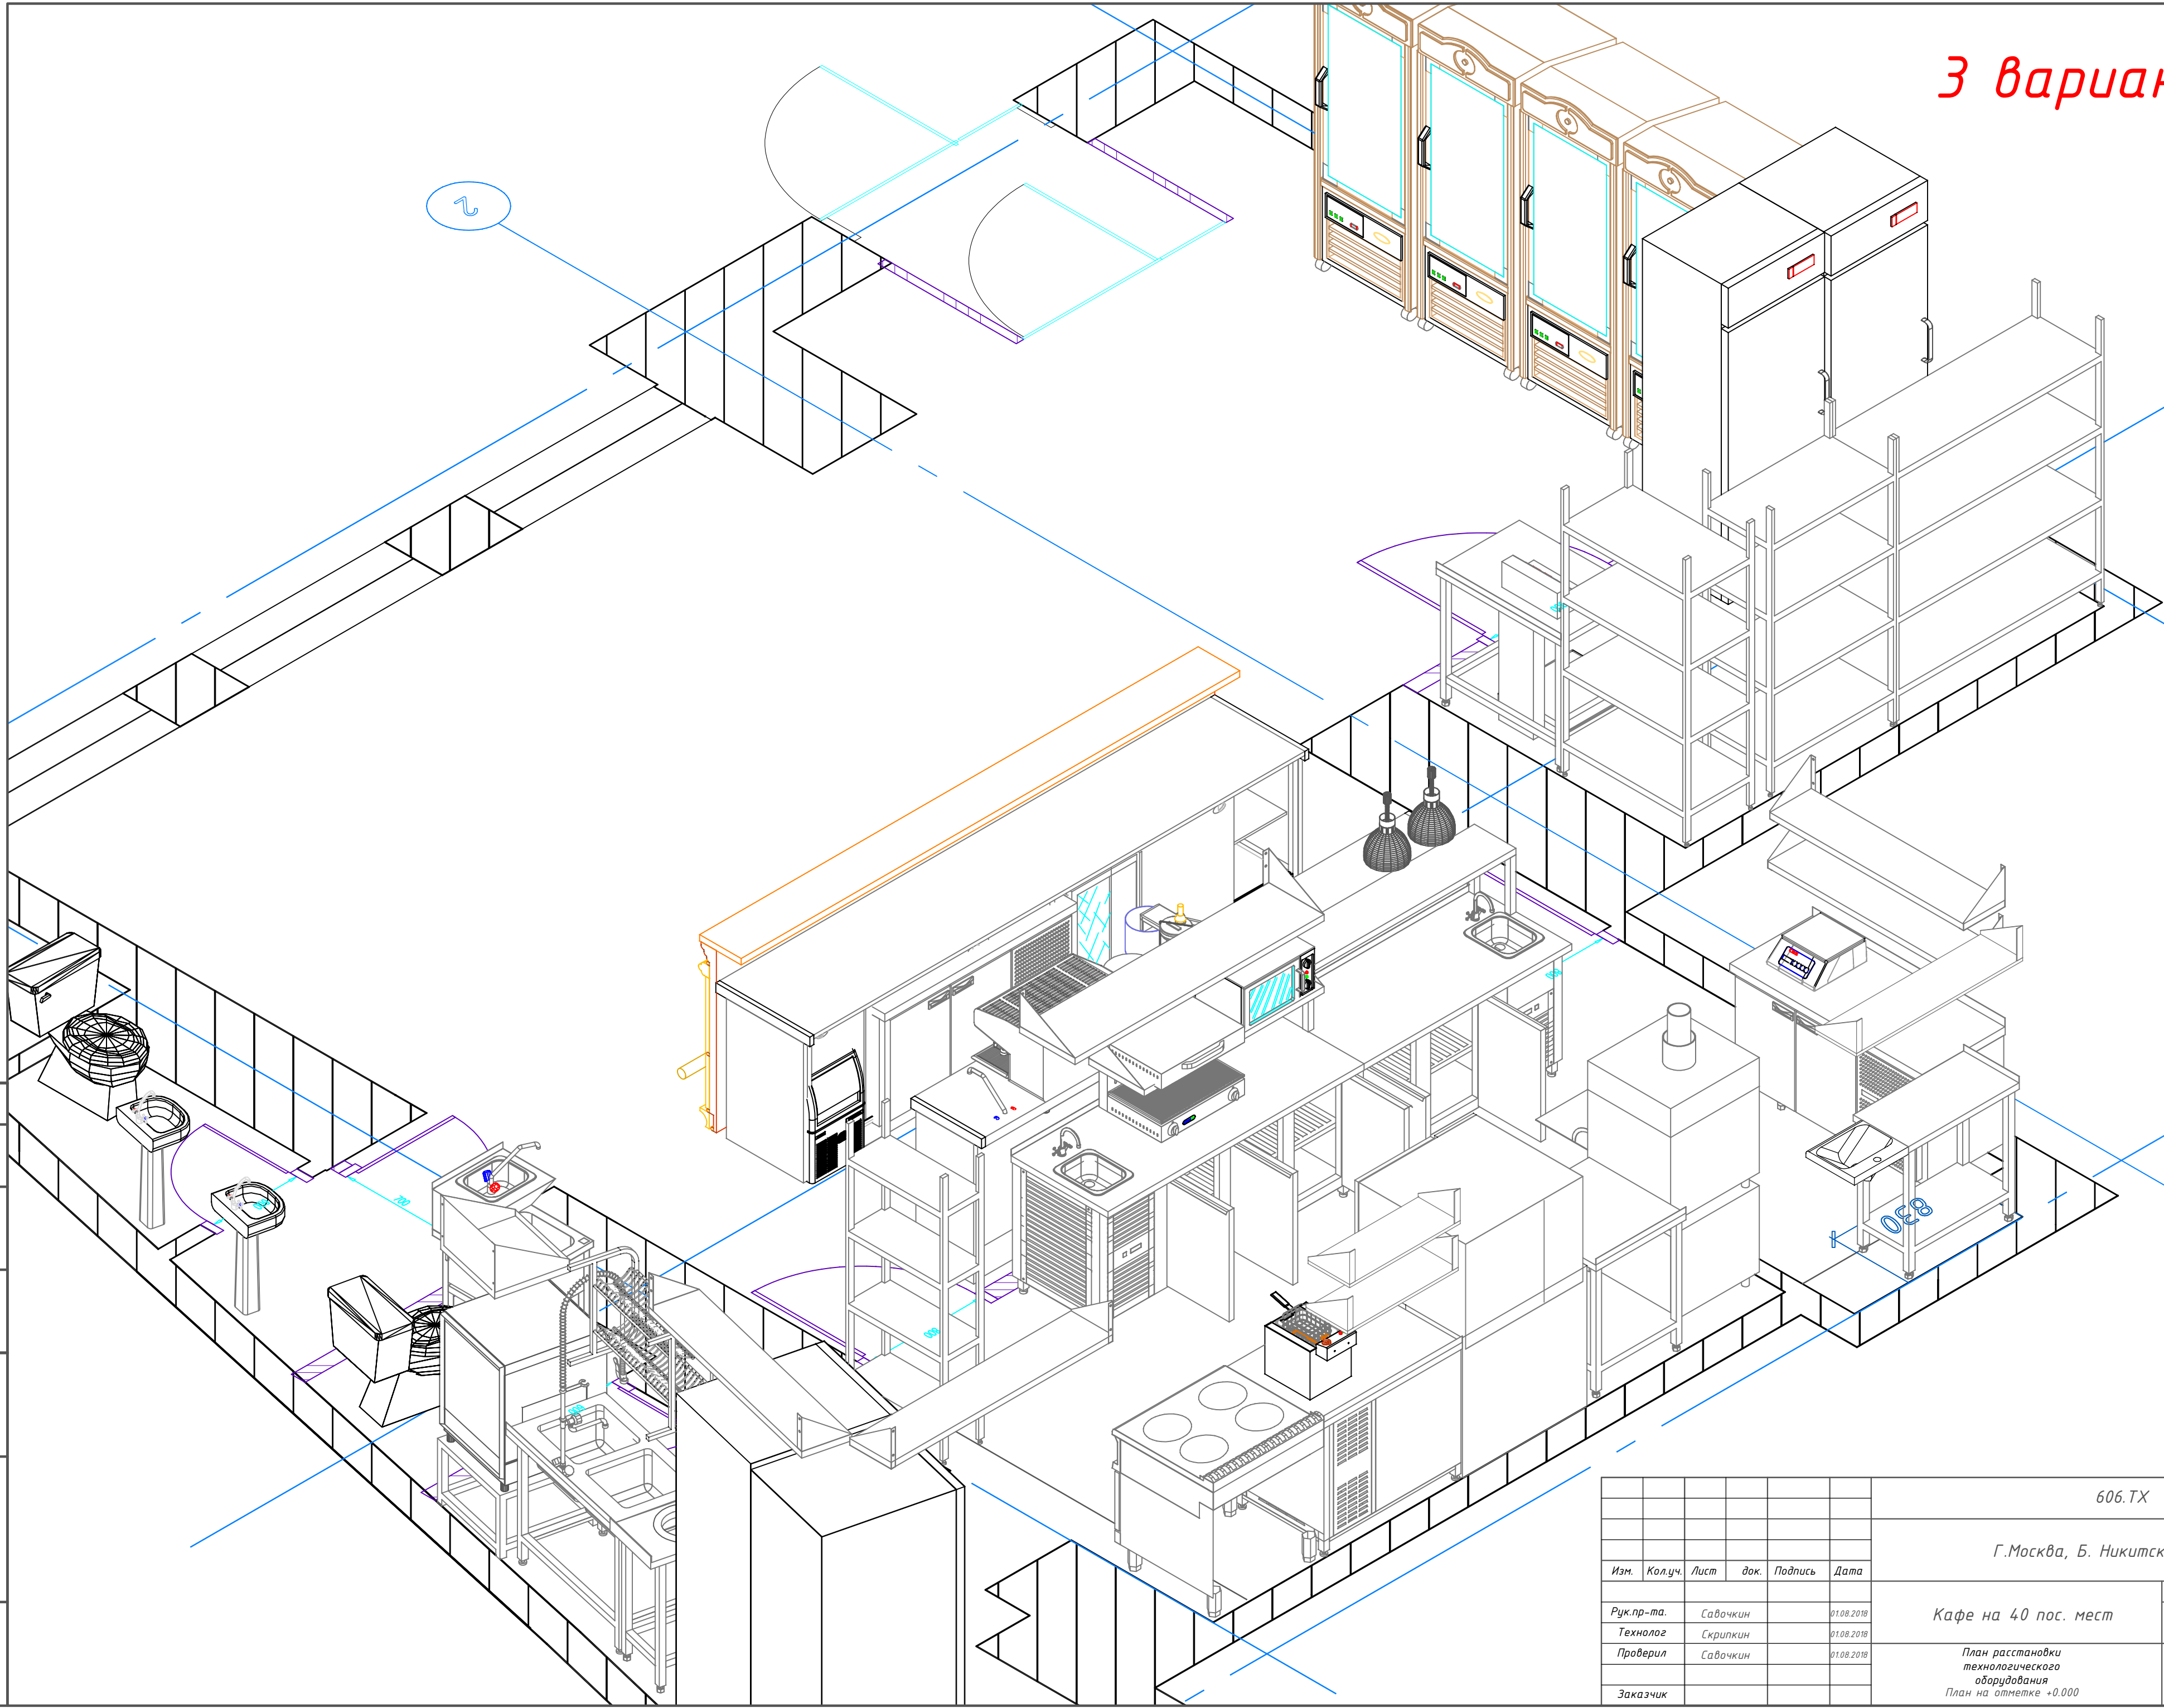

						606.ТХ			
						Г.Москва, Б. Никитская, д.19/13			
Изм.	Кол.уч.	Лист	док.	Подпись	Дата	Кафе на 40 пос. мест	Стадия	Лист	Листов
Рук.пр-та.	Савочкин				01.08.2018		РД		5
Технолог	Скрипкин				01.08.2018				
Проверил	Савочкин				01.08.2018				
Заказчик									
						План расстановки технологического оборудования План на отметке +0.000			