


Согласовано

Взам. инв. №

Подп. и дата

Инв. № подл.

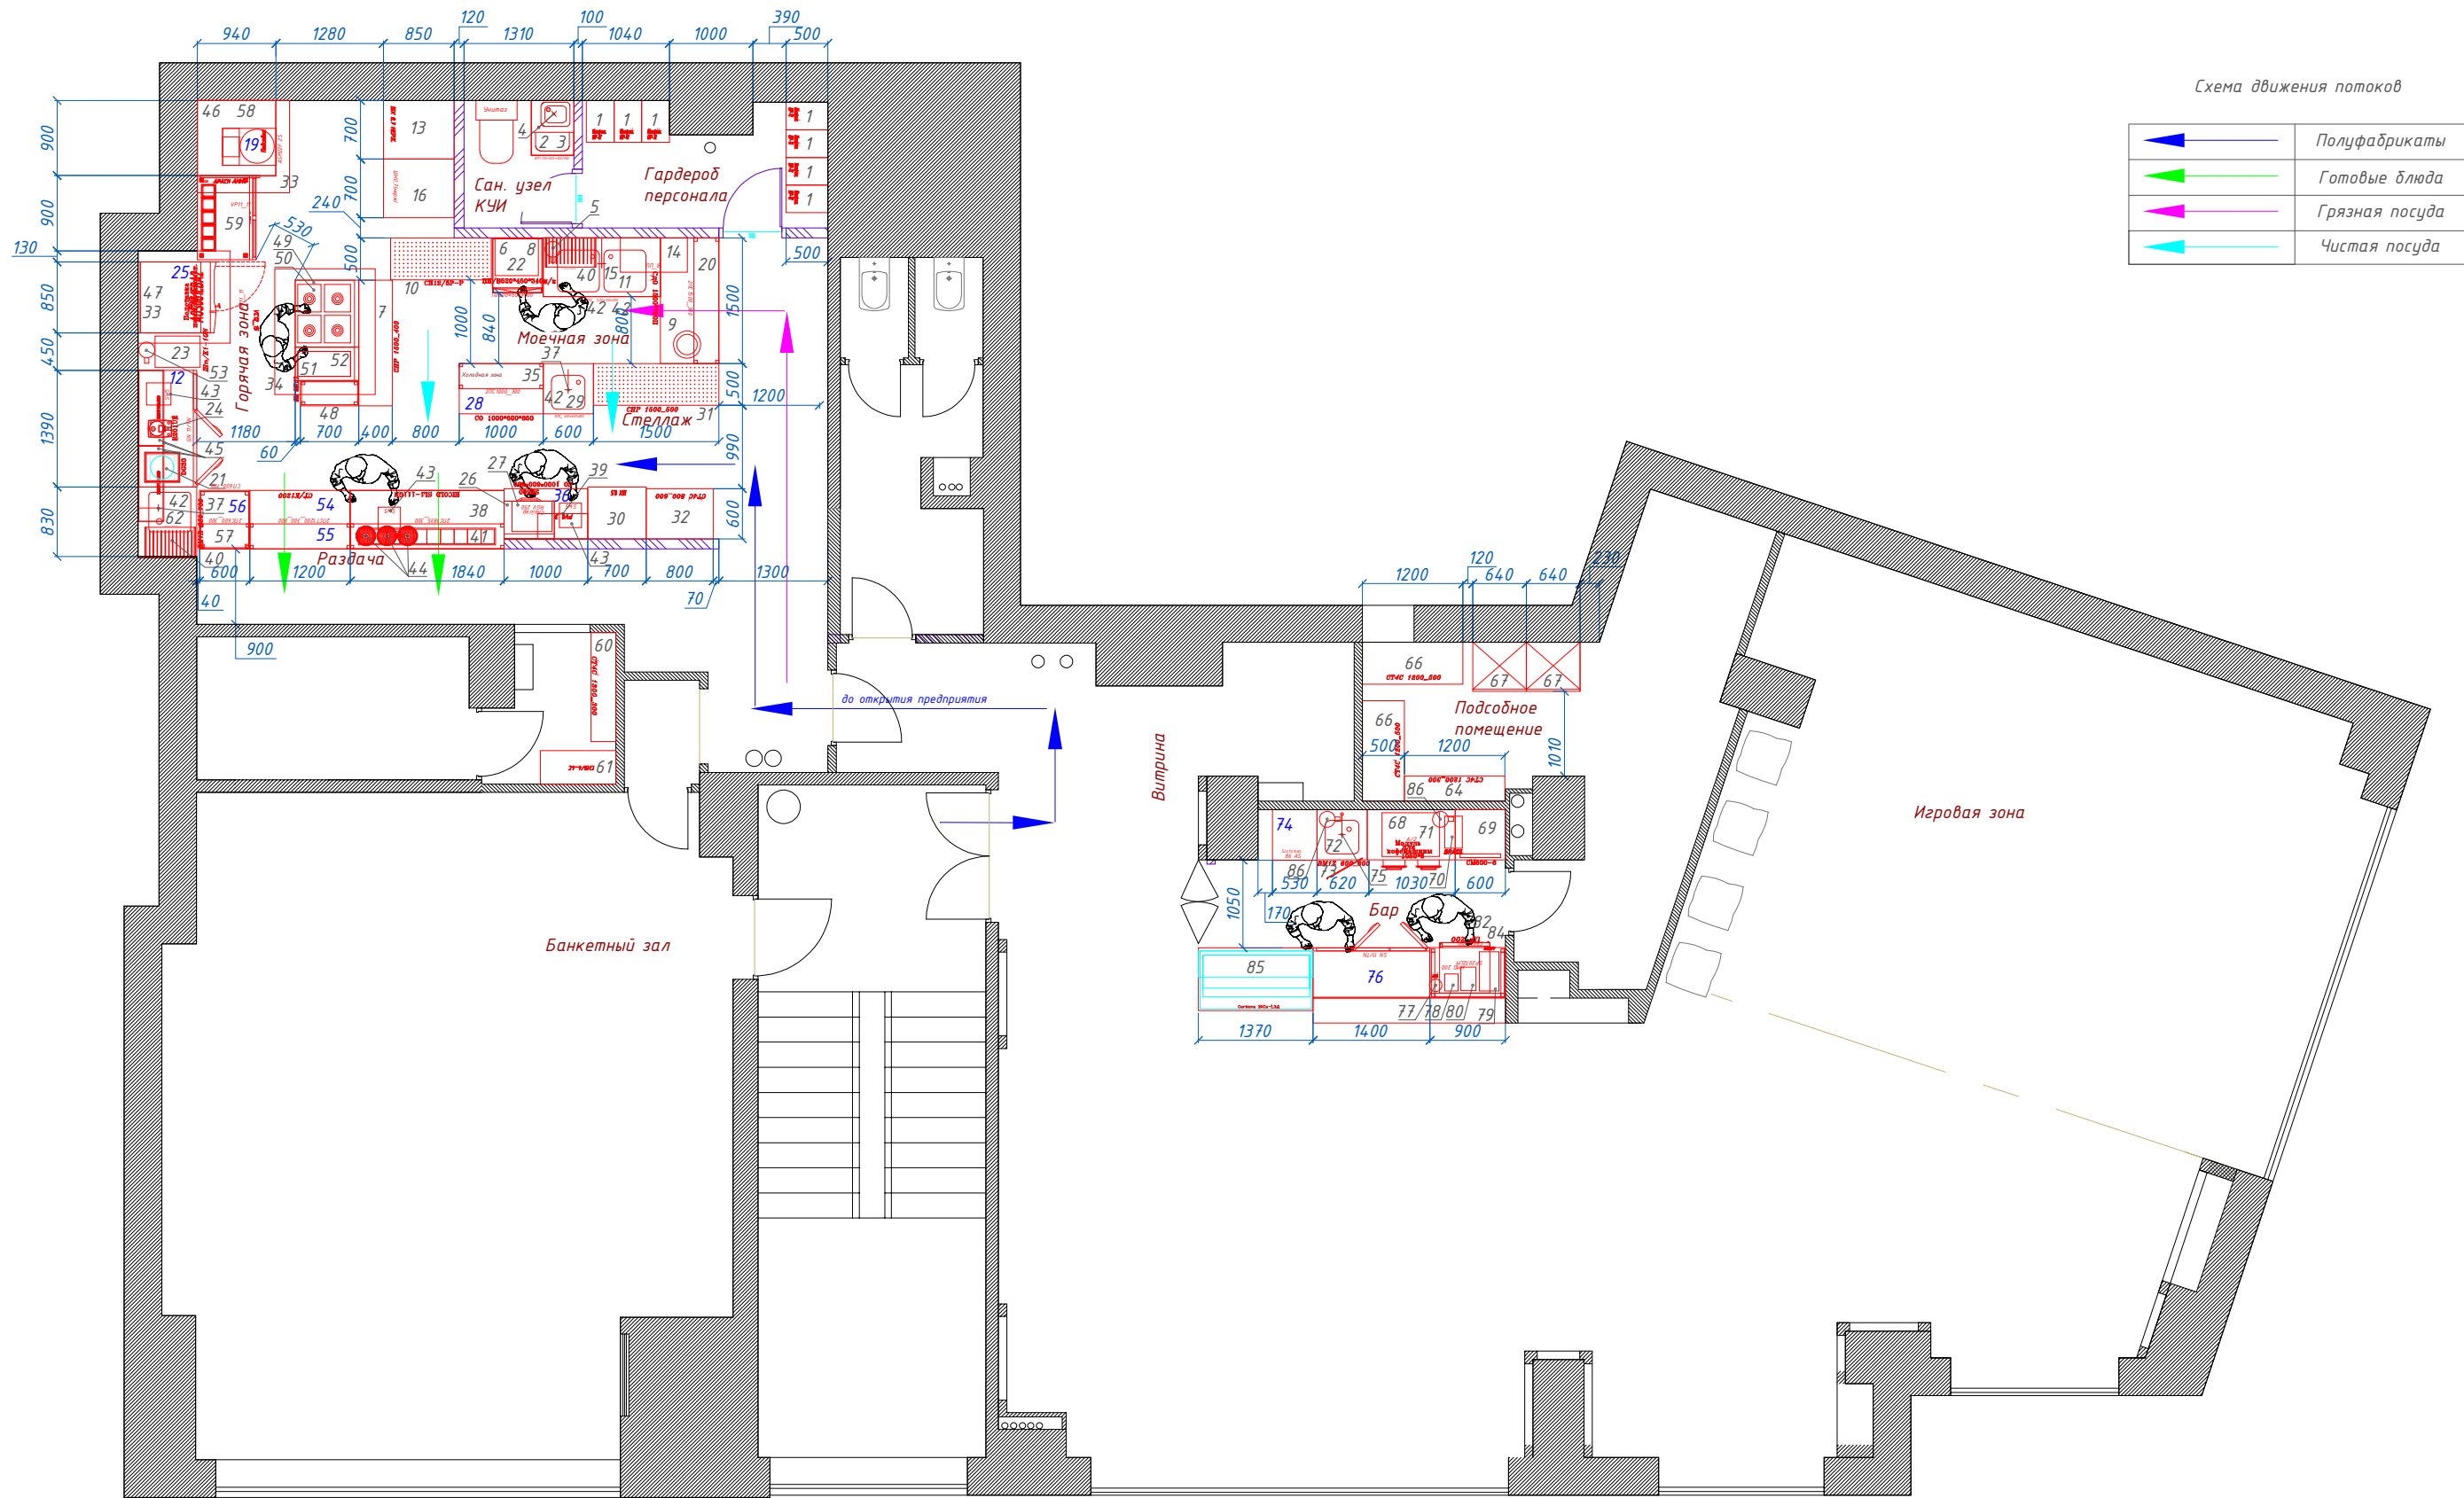

Масштаб 1:80

						945.ТХ			
						Г. Москва, Шелепихинская набережная, д.34, к1			
Изм.	Кол.уч.	Лист	док.	Подпись	Дата	Кафе "Сердце" на 48 пос мест, банкетный зал на 30 пос. мест	Стадия	Лист	Листов
Рук.пр-та.		Сухов			05.02.2021		П	1	13
Технолог		Савочкин			05.02.2021				
						План расстановки технологического оборудования План второго этажа	000 "Уникальные техенологии"		


Согласовано

Взам. инв. №

Подп. и дата

Инв. № подл.

Масштаб 1:40

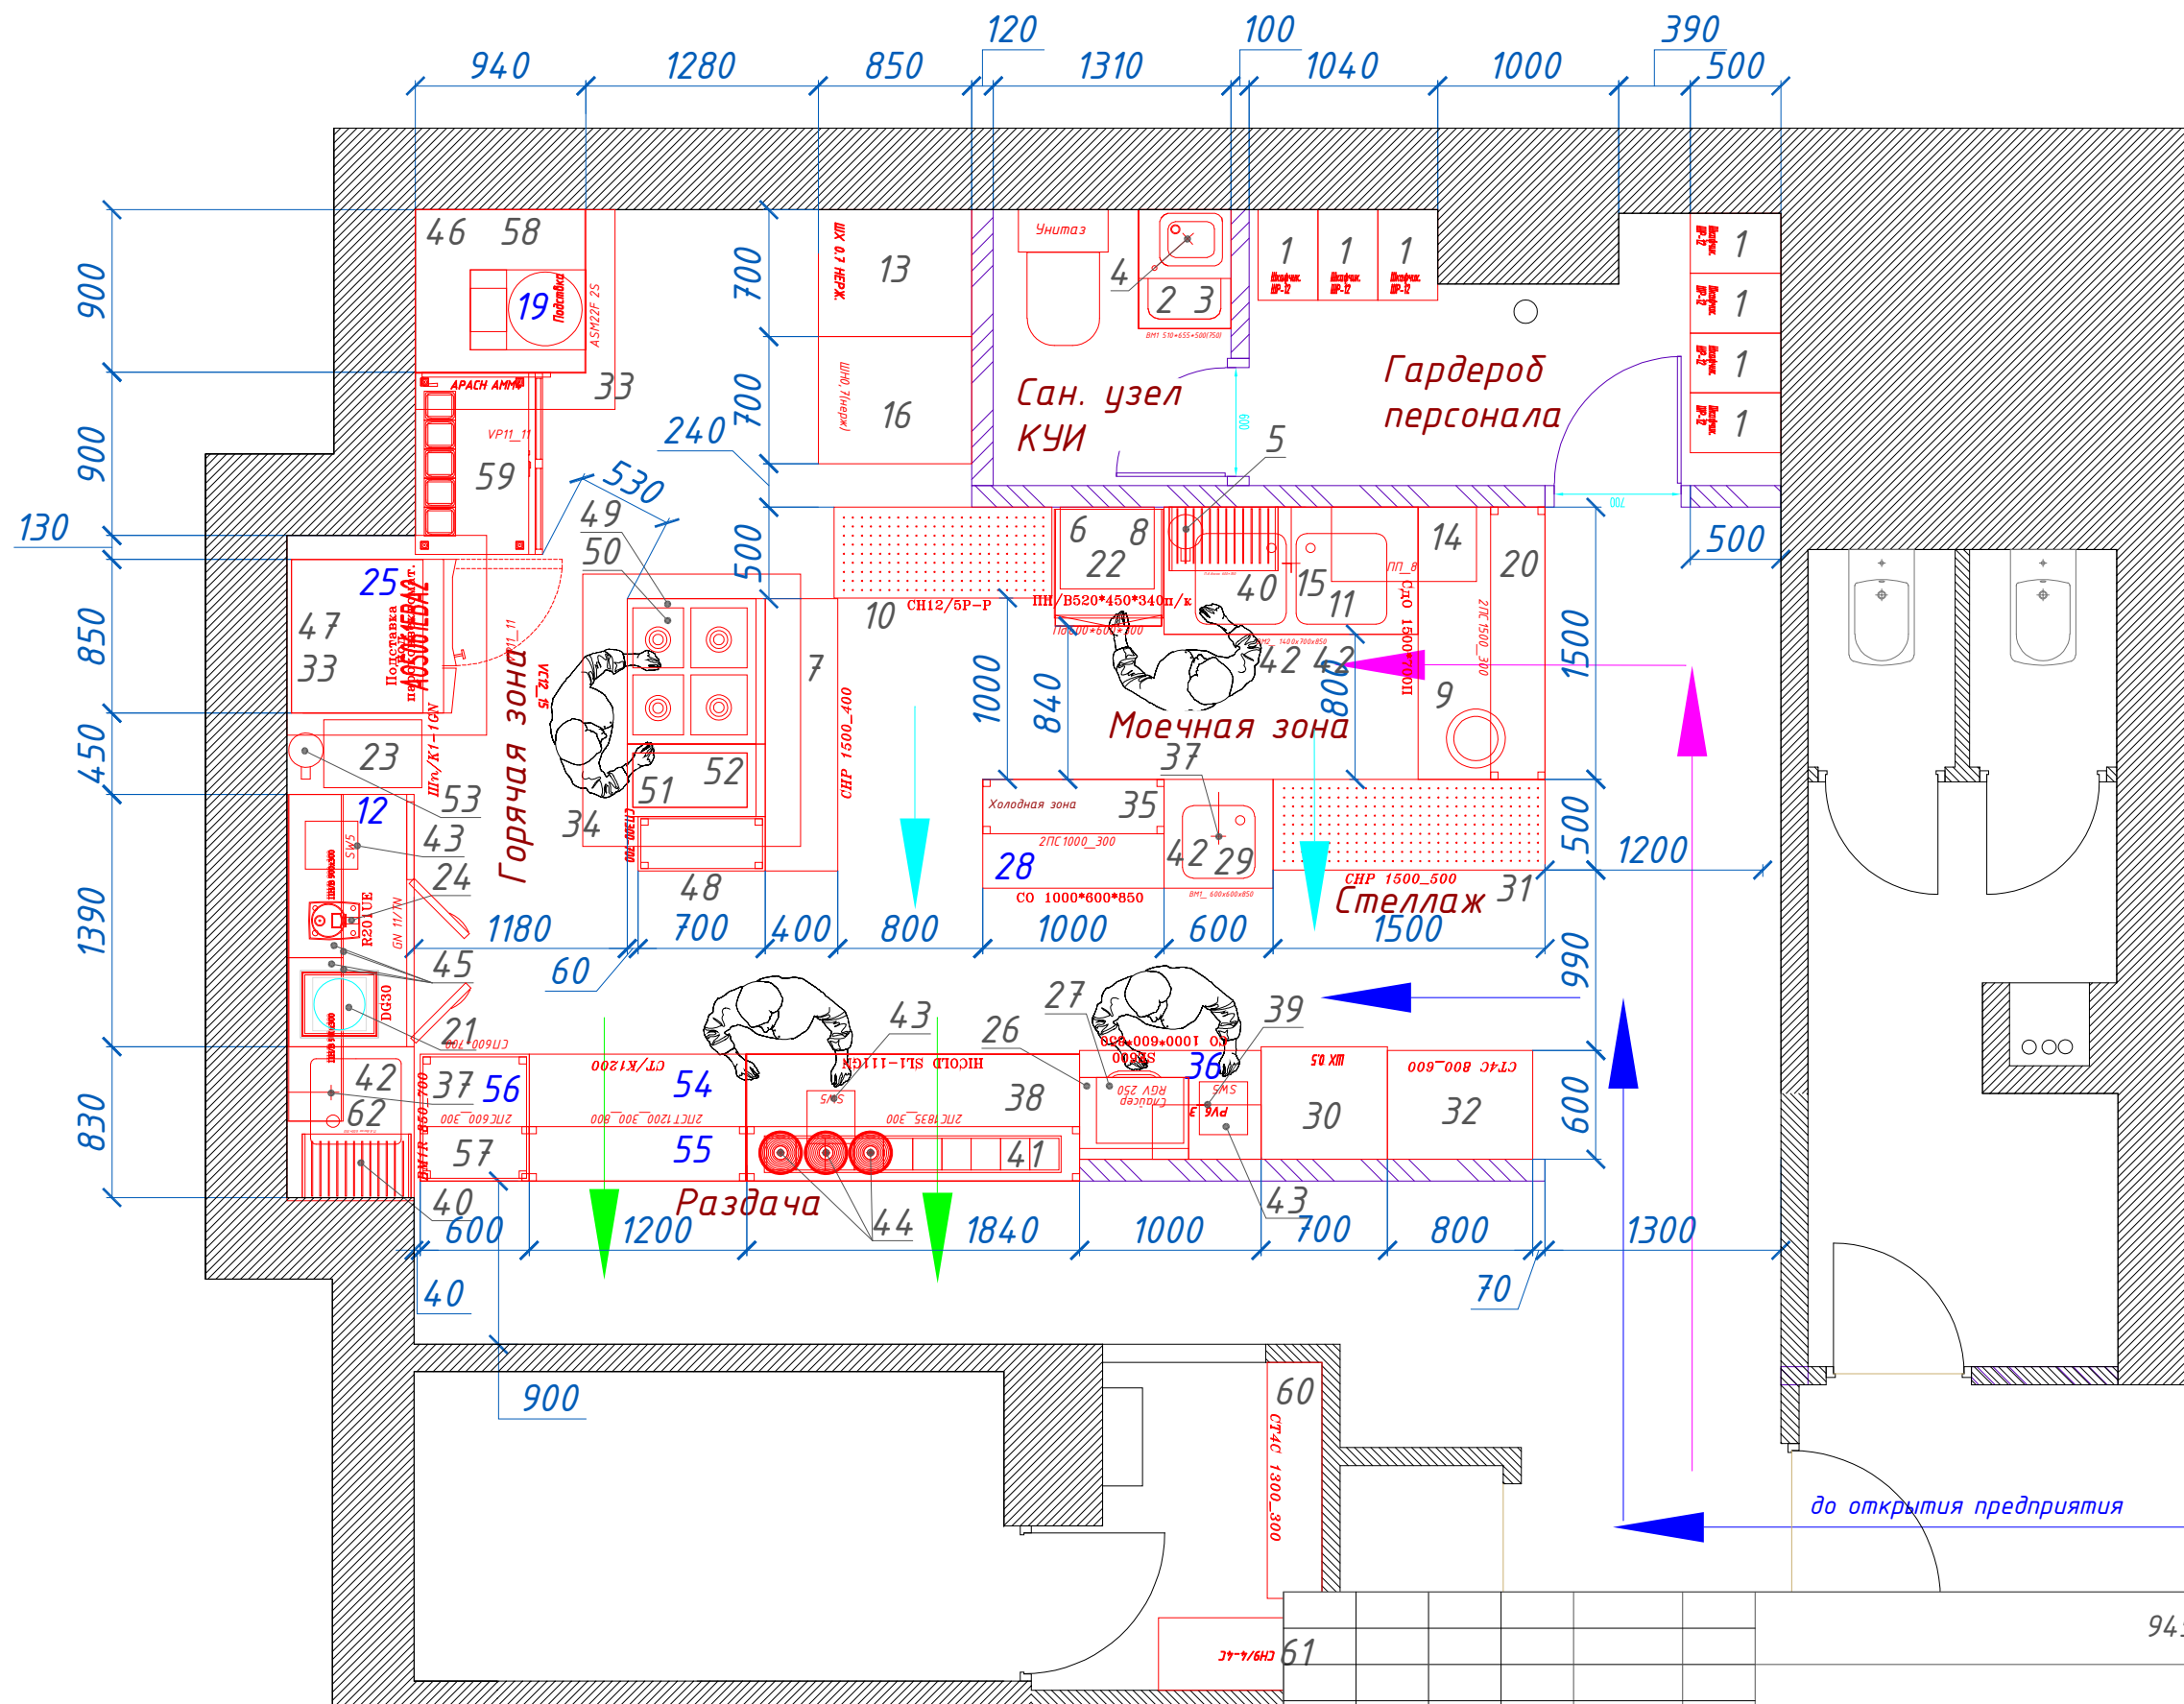


Изм.	Кол.уч.	Лист	док.	Подпись	Дата
Рук.пр-та.	Сухов				05.02.2021
Технолог	Савочкин				05.02.2021

945.ТХ			
Г. Москва, Шелепихинская набережная, д.34, к1			
Кафе "Сердце" на 48 пос мест, банкетный зал на 30 пос. мест	Стадия	Лист	Листов
	П	2	13
План расстановки технологического оборудования План на отметке +0.000	ООО "Уникальные техенологии"		

Согласовано

Инв. № подл. Подп. и дата Взам. инв. №


Масштаб 1:40

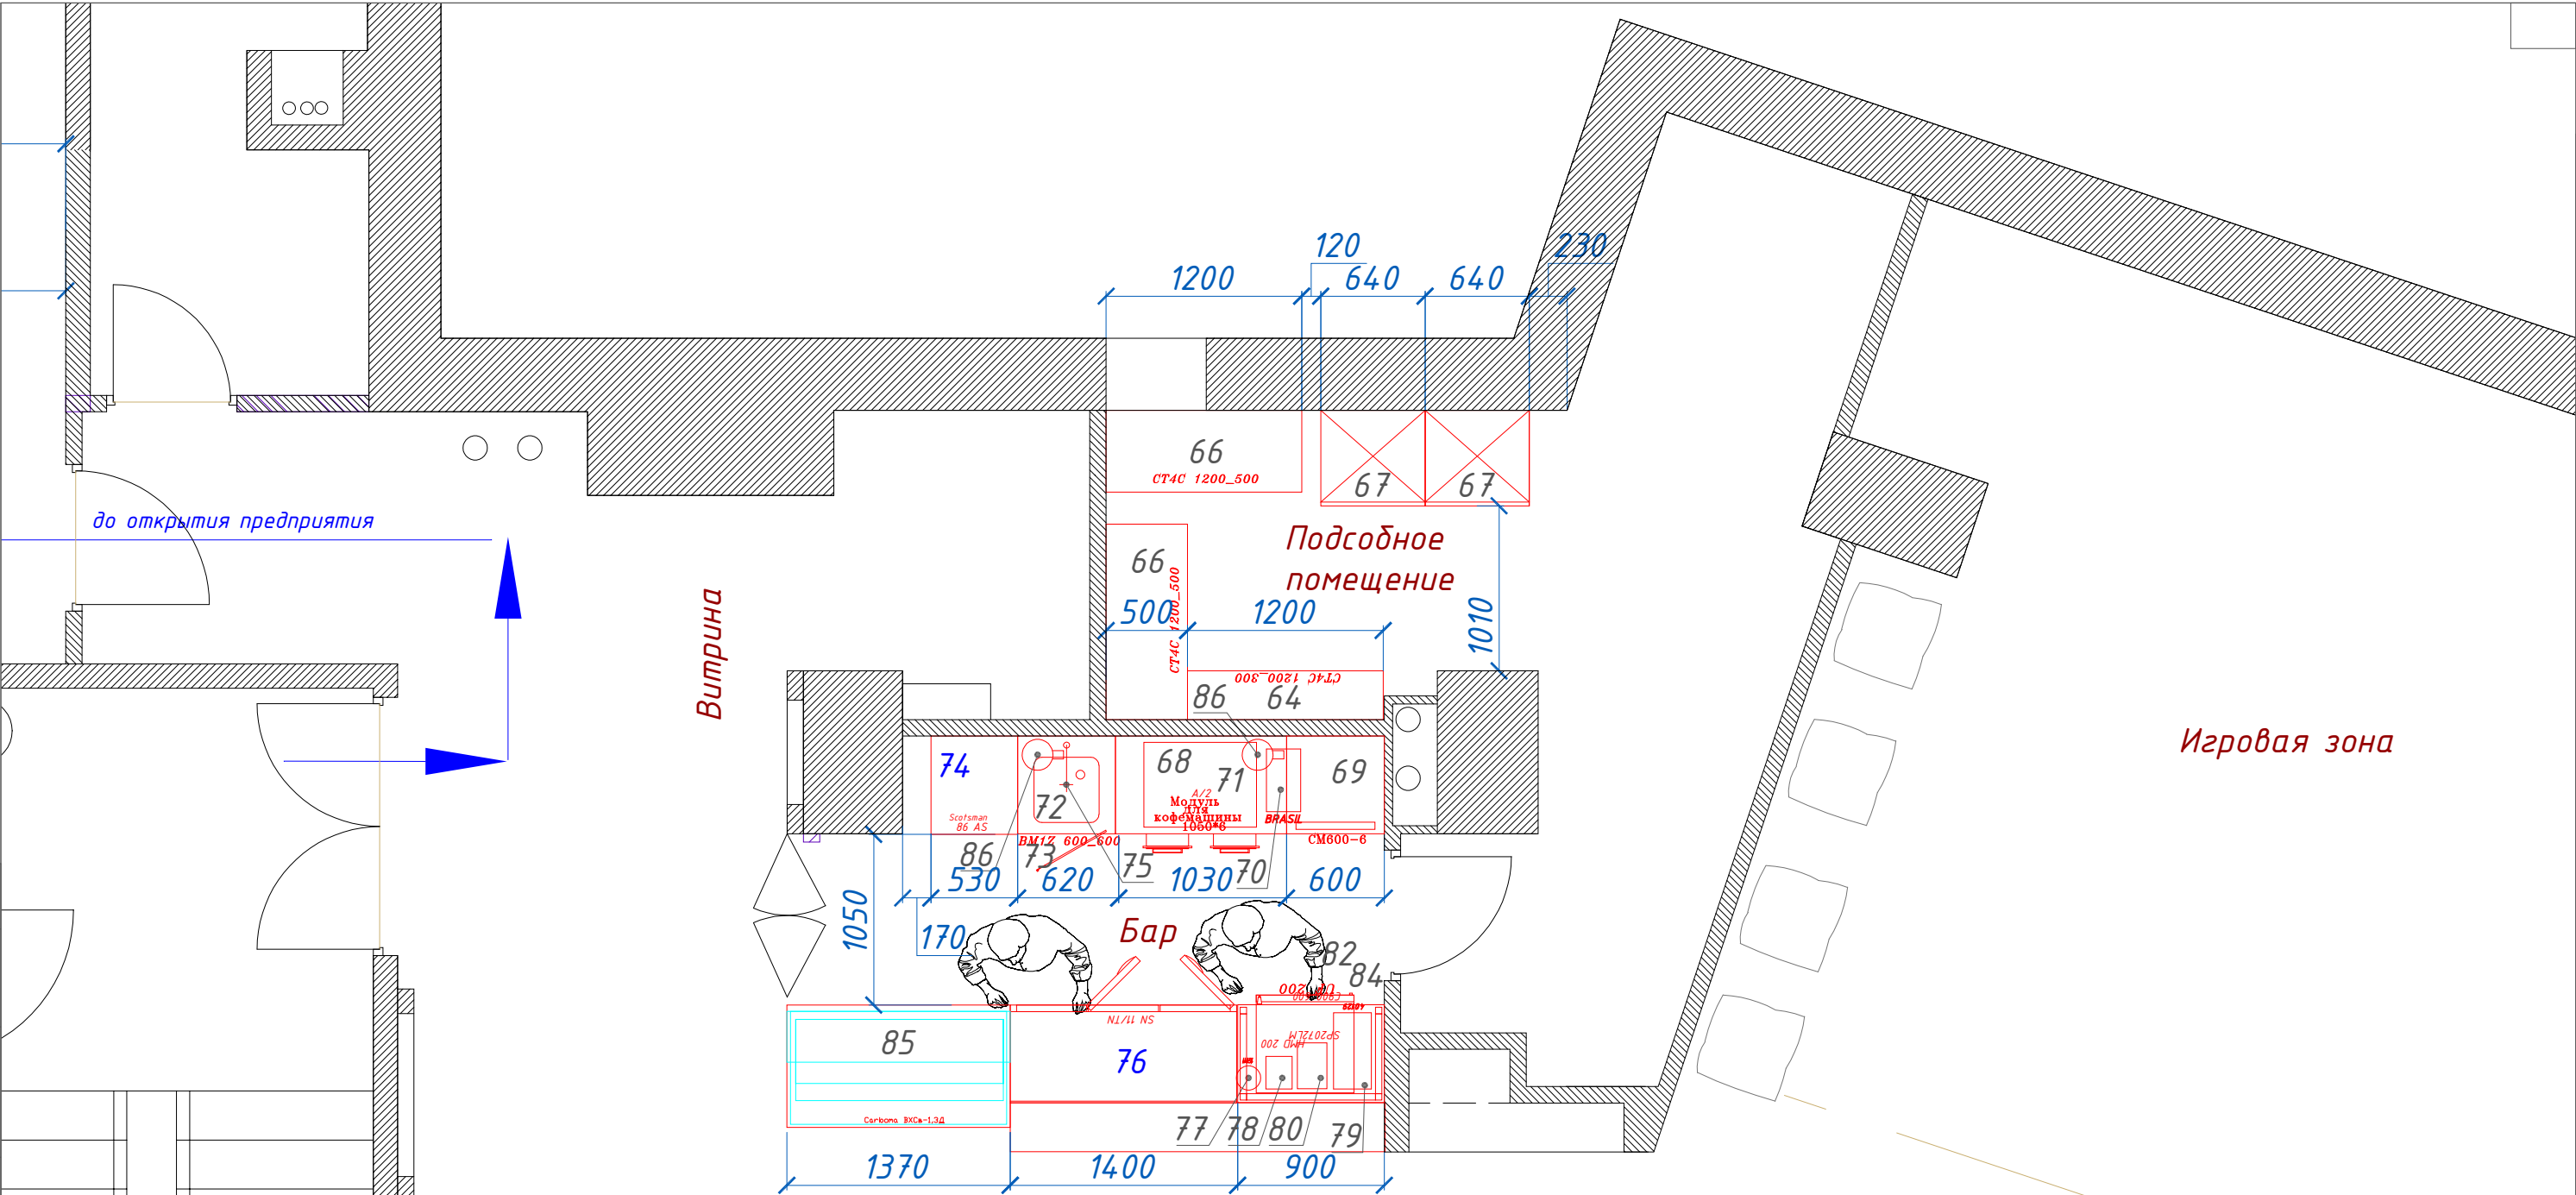

						945.TX		
						Г. Москва, Шелепихинская набережная, д.34, к1		
Изм.	Кол.уч.	Лист	док.	Подпись	Дата	Кафе "Сердце" на 48 пос мест, банкетный зал на 30 пос. мест	Стадия	Лист
Рук.пр-та.		Сухов			05.02.2021		П	3
Технолог		Савочкин			05.02.2021			13
						План расстановки технологического оборудования План на отметке +0.000	ООО "Уникальные техенологии"	

Условные обозначения

Э – подвод электроэнергии
Ф – фазность тока
Р – однофазная розетка с заземлением
ШР – штепсельная розетка с рабочим нулем и заземлением
h – высота подводов от чистого пола в мм
L – длина свободного провода в мм
380В / 220В – напряжение в сети
* – условное значение предполагаемого оборудования, перед подключением обязательно смотреть паспорт производителя

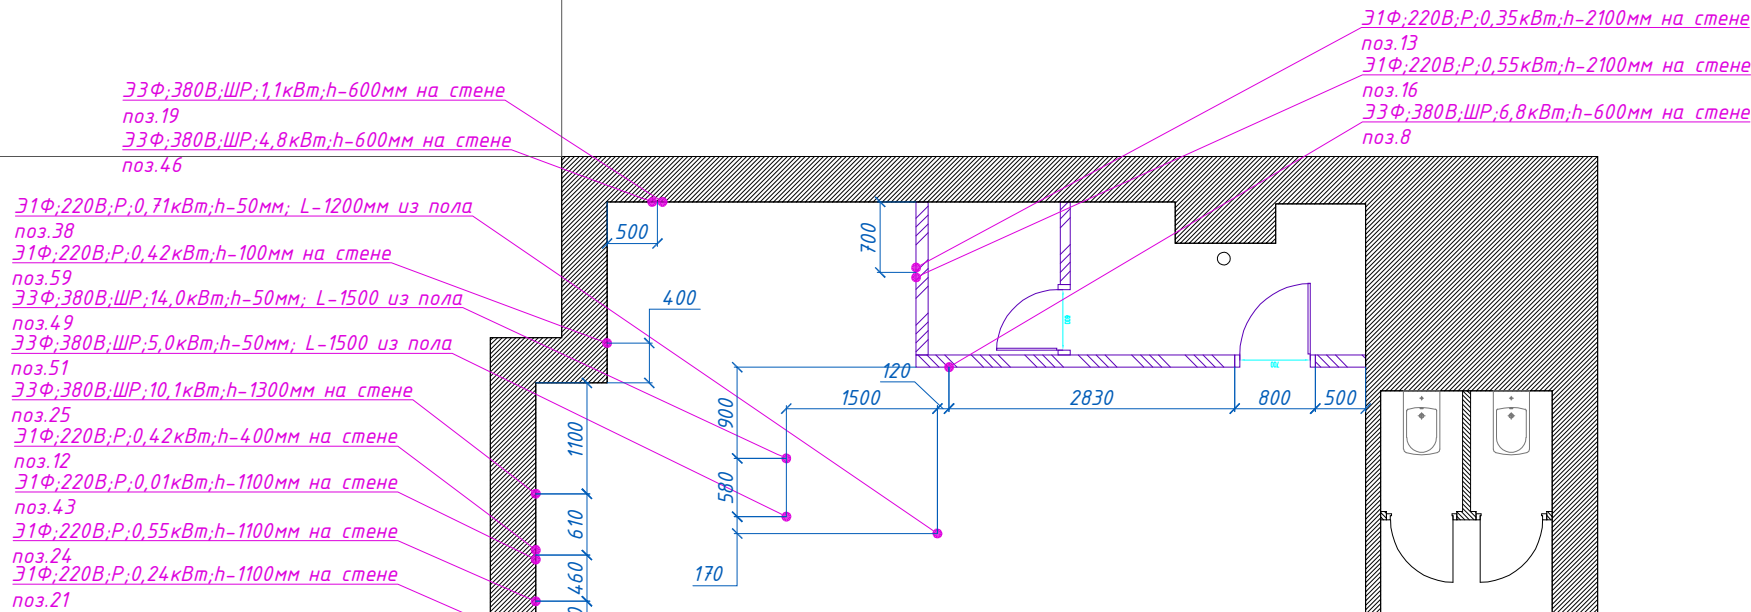

31Ф, 220В, Р, 1,05кВт, h-50мм, L-1200мм из пола
поз.54
31Ф, 220В, Р, 0,15кВт, h-50мм, L-1200мм из пола
поз.28
31Ф, 220В, Р, 0,01кВт, h-50мм, L-1200мм из пола
поз.43

31Ф, 220В, 0,25кВт, L-2500мм с потолка
поз.44
31Ф, 220В, Р, 0,15кВт, h-1100мм на стене
поз.27
33Ф, 380В, ШР, 4,0кВт, h-1500мм на стене
поз.26
31Ф, 220В, Р, 0,15кВт, h-100мм на стене
поз.36
31Ф, 220В, Р, 0,01кВт, h-1100мм на стене
поз.43
31Ф, 220В, Р, 0,35кВт, h-2100мм на стене
поз.30

31Ф, 220В, Р, 0,3кВт, h-400мм на стене
поз.67
31Ф, 220В, Р, 0,3кВт, h-400мм на стене
поз.67

31Ф, 220В, Р, 0,33кВт, h-100мм на стене
поз.74
33Ф, 380В, ШР, 7,3кВт, h-1300мм на стене
поз.68
31Ф, 220В, Р, 0,22кВт, h-1100мм на стене
поз.70
31Ф, 220В, Р, 0,41кВт, h-100мм на стойке
поз.85
31Ф, 220В, Р, 0,42кВт, h-100мм на стойке
поз.76
31Ф, 220В, Р, 0,75кВт, h-1100мм на стене
поз.77
31Ф, 220В, Р, 0,3кВт, h-1100мм на стене
поз.78
31Ф, 220В, Р, 0,4кВт, h-1100мм на стене
поз.79
31Ф, 220В, Р, 0,45кВт, h-1100мм на стене
поз.80
31Ф, 220В, Р, 0,15кВт, h-400мм на стене
поз.82

Примечания


- Прокладка электросетей должна осуществляться в плоскости стен и пола, согласно требованиям ПУЭ по трёх или пятипроводной схеме, в зависимости от подключаемого технологического оборудования
- В случае подключения оборудования путём ввода кабеля напрямую, без установки разъёма, необходим выход МЯГКОГО (МНОГОЖИЛЬНОГО) кабеля, длиной 2500мм, согласно заданным высотам
- Установленные силовые разъёмы необходимо укомплектовать ответной частью.

Масштаб 1:75

						945.ТХ			
						Г. Москва, Шелепихинская набережная, д.34, к1			
Изм.	Кол.уч.	Лист	док.	Подпись	Дата	Кафе "Сердце" на 48 пос мест, банкетный зал на 30 пос. мест	Стадия	Лист	Листов
Рук.пр-та.	Сухов				05.02.2021		П	4	13
Технолог	Савочкин				05.02.2021				
						План расположения электропроводов План второго этажа	ООО "Уникальные техенологии"		

Условные обозначения

Х.В. – подвод холодной воды
Х.Г.В – подвод холодной и горячей воды
d – диаметр трубопровода
К – отвод в канализацию
h – высота подводов от чистого пола в мм
Трап d=100мм
Габариты трапа должны быть 500х230мм. Центр
ливневки определяется привязкой указанной на плане

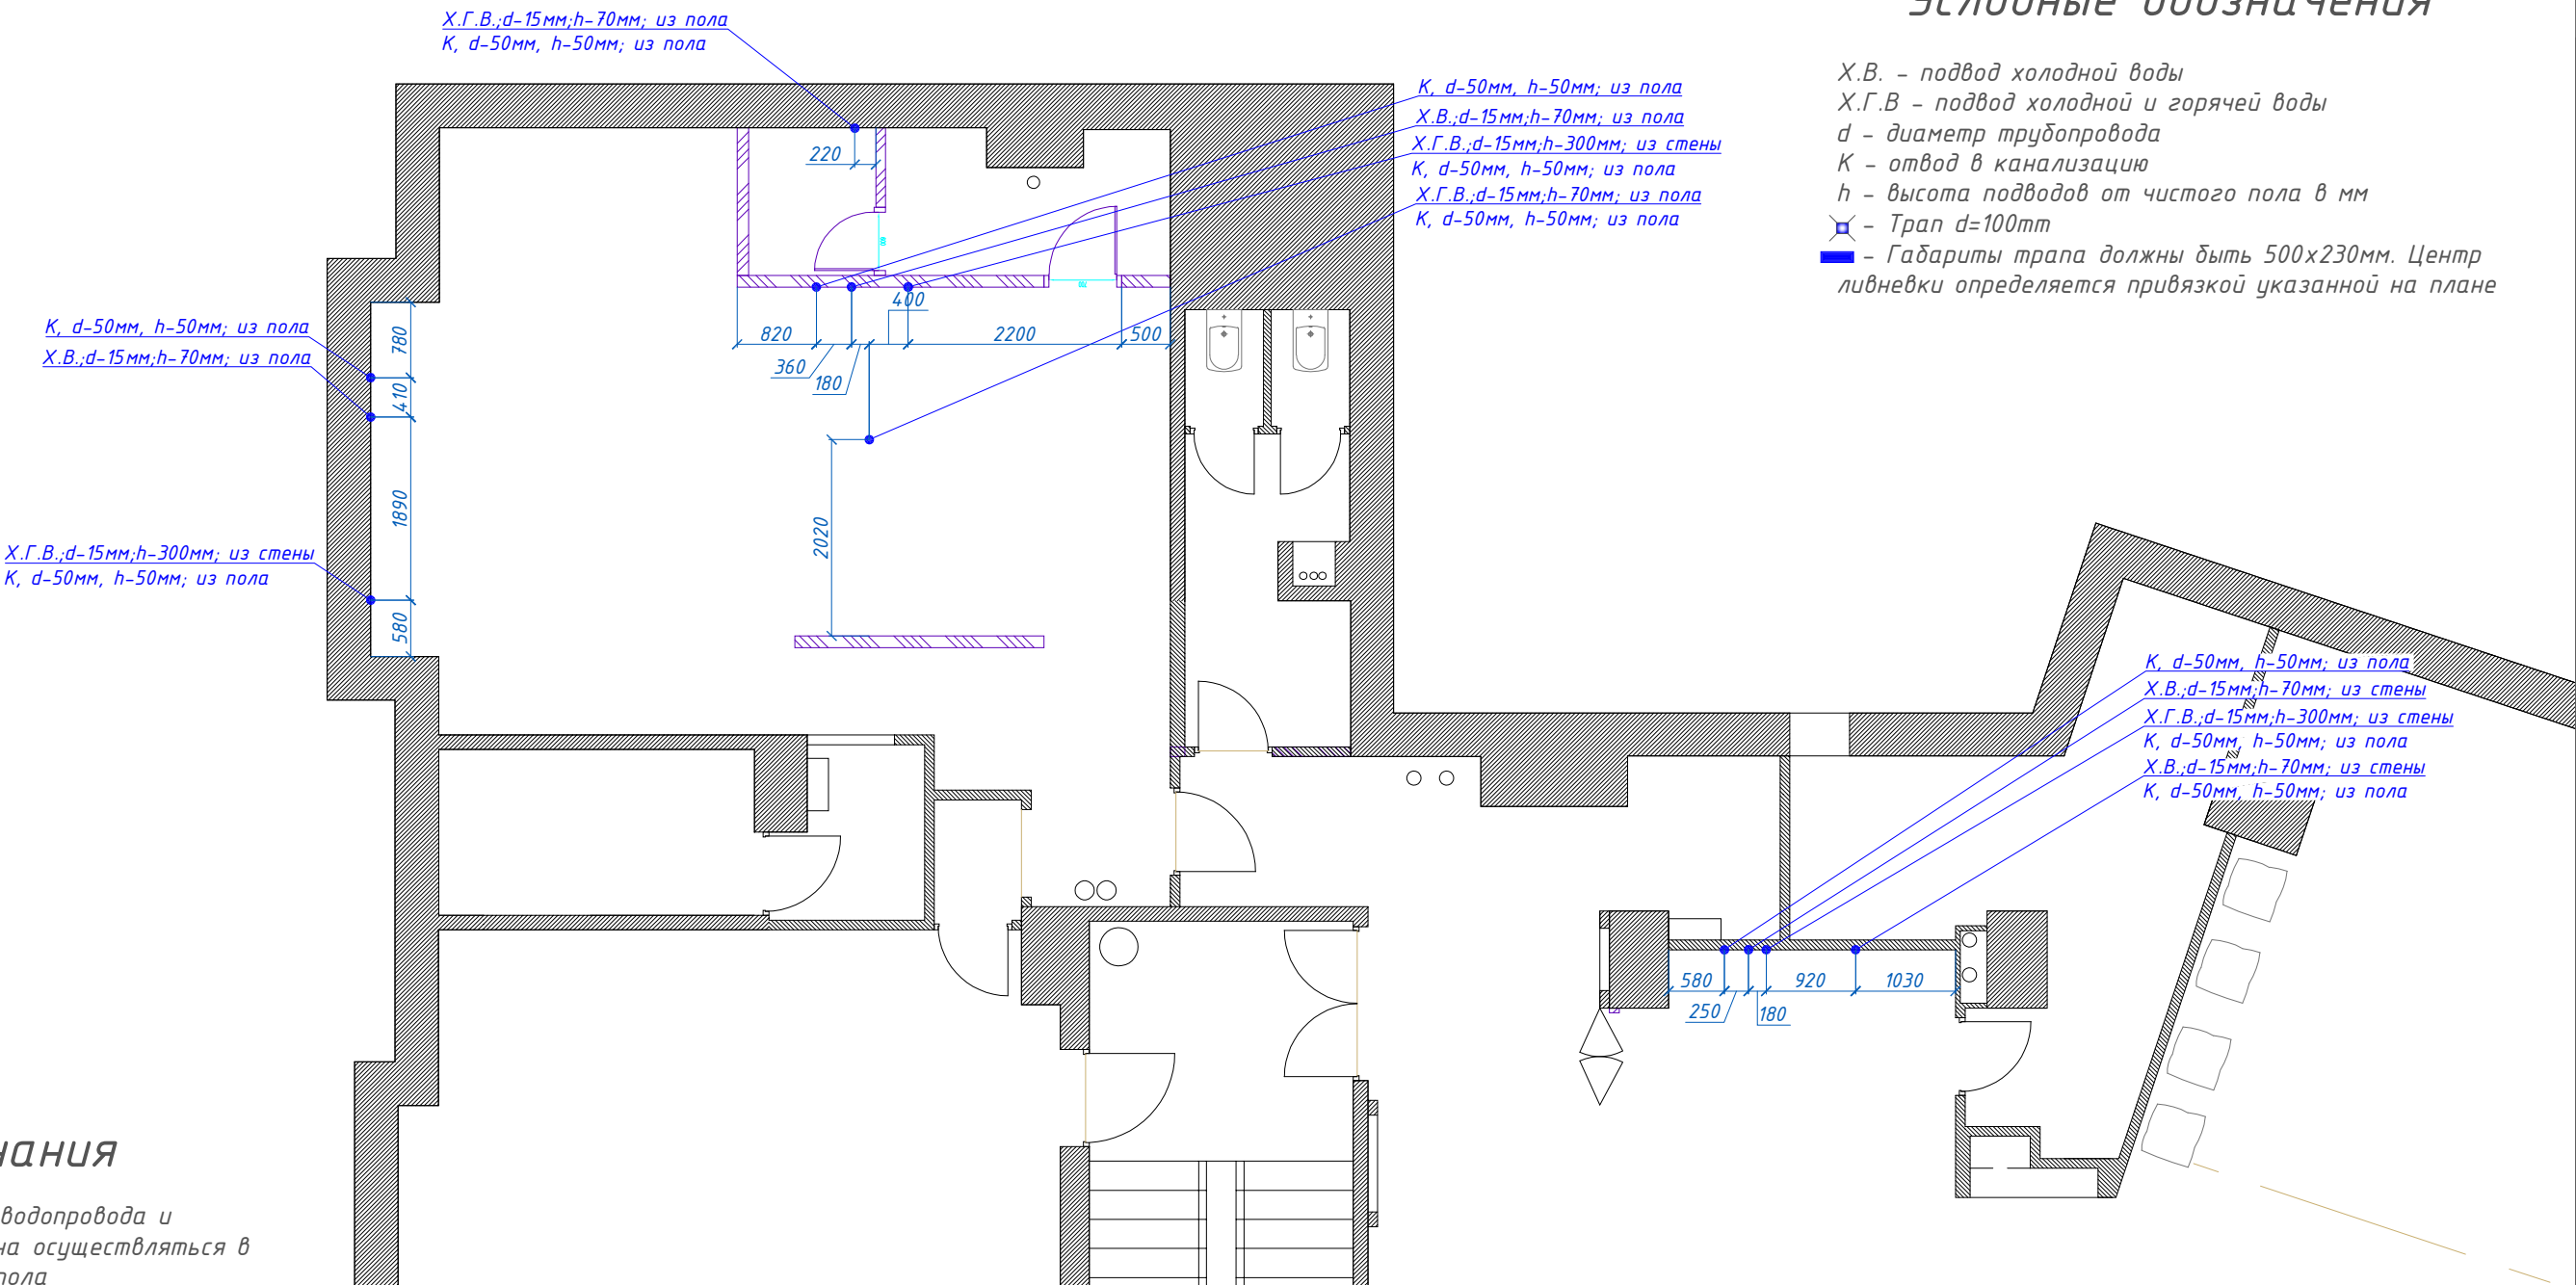

Примечания

- Прокладка труб водопровода и канализации должна осуществляться в плоскости стен и пола
- Все производственные помещения следует оборудовать сливными трапами.
- Слив от оборудования в канализацию предусмотреть в ближайший трап или канализационную сеть с разрывом струи не менее 20мм.
- Выводы из пола должны быть выполнены максимально приближенными к примыкающей стене, или отнесены от неё на расстояние 150мм.
- Вентили G 1/2" возможно использовать угловые или прямые полнопроходные, монтировать максимально приближенно к стене
- Давление холодной и горячей воды в системе водоснабжения в пределах 150 кПа ÷ 600 кПа; при необходимости с установкой насоса, повышающего давление либо понижающего редуктора

Масштаб 1:75

						945.ТХ			
						Г. Москва, Шелепихинская набережная, д.34, к1			
Изм.	Кол.уч.	Лист	док.	Подпись	Дата	Кафе "Сердце" на 48 пос мест, банкетный зал на 30 пос. мест	Стадия	Лист	Листов
Рук.пр-та.		Сухов			05.02.2021		П	5	13
Технолог		Савочкин			05.02.2021				
						План расположения выводов воды и канализации План второго этажа	ООО "Уникальные техенологии"		

Масштаб 1:75

Примечания

- В местах крепления зонтов необходимо обеспечить достаточную несущую способность поверхностей. Подготовить подвесы в точках крепления /шпилька М8 или цепь/ на высоте 2100 мм от пола. Отверстия в зонтах под крепеж сверлятся по месту
- Вытяжной зонт крепиться на высоте 2000 мм от пола /по нижнему срезу зонта/
- Отверстия в вытяжных зонтах для врезки фланцев выполняются по месту /при подключении/
- В помещении предназначенном под установку холодильных камер с моноблоками или сплит-системами необходимо обеспечить приточно-вытяжную вентиляцию (температура окружающей среды от +5 до +25 градусов Цельсия, влажность воздуха не выше 80%)
- Отопительные приборы, в помещениях предназначенных под установку холодильных камер, следует размещать на расстоянии не менее 1500 мм от стен камер

точки крепления подвесов зонтов
/шпилька М8 или цепь/ Н=2200 мм от пола

Согласовано

Взам. инв. №

Подп. и дата

Инв. № подл.

945.ТХ

Г. Москва, Шелепихинская набережная, д.34, к1

Кафе "Сердце" на 48 пос. мест,
банкетный зал на 30 пос. мест

План расположения
вентиляционных
зонтов
План второго этажа

Стадия	Лист	Листов
П	6	13

ООО "Уникальные
технологии"

