


Согласовано

Взам. инв. №

Подп. и дата

Инв. № подл.

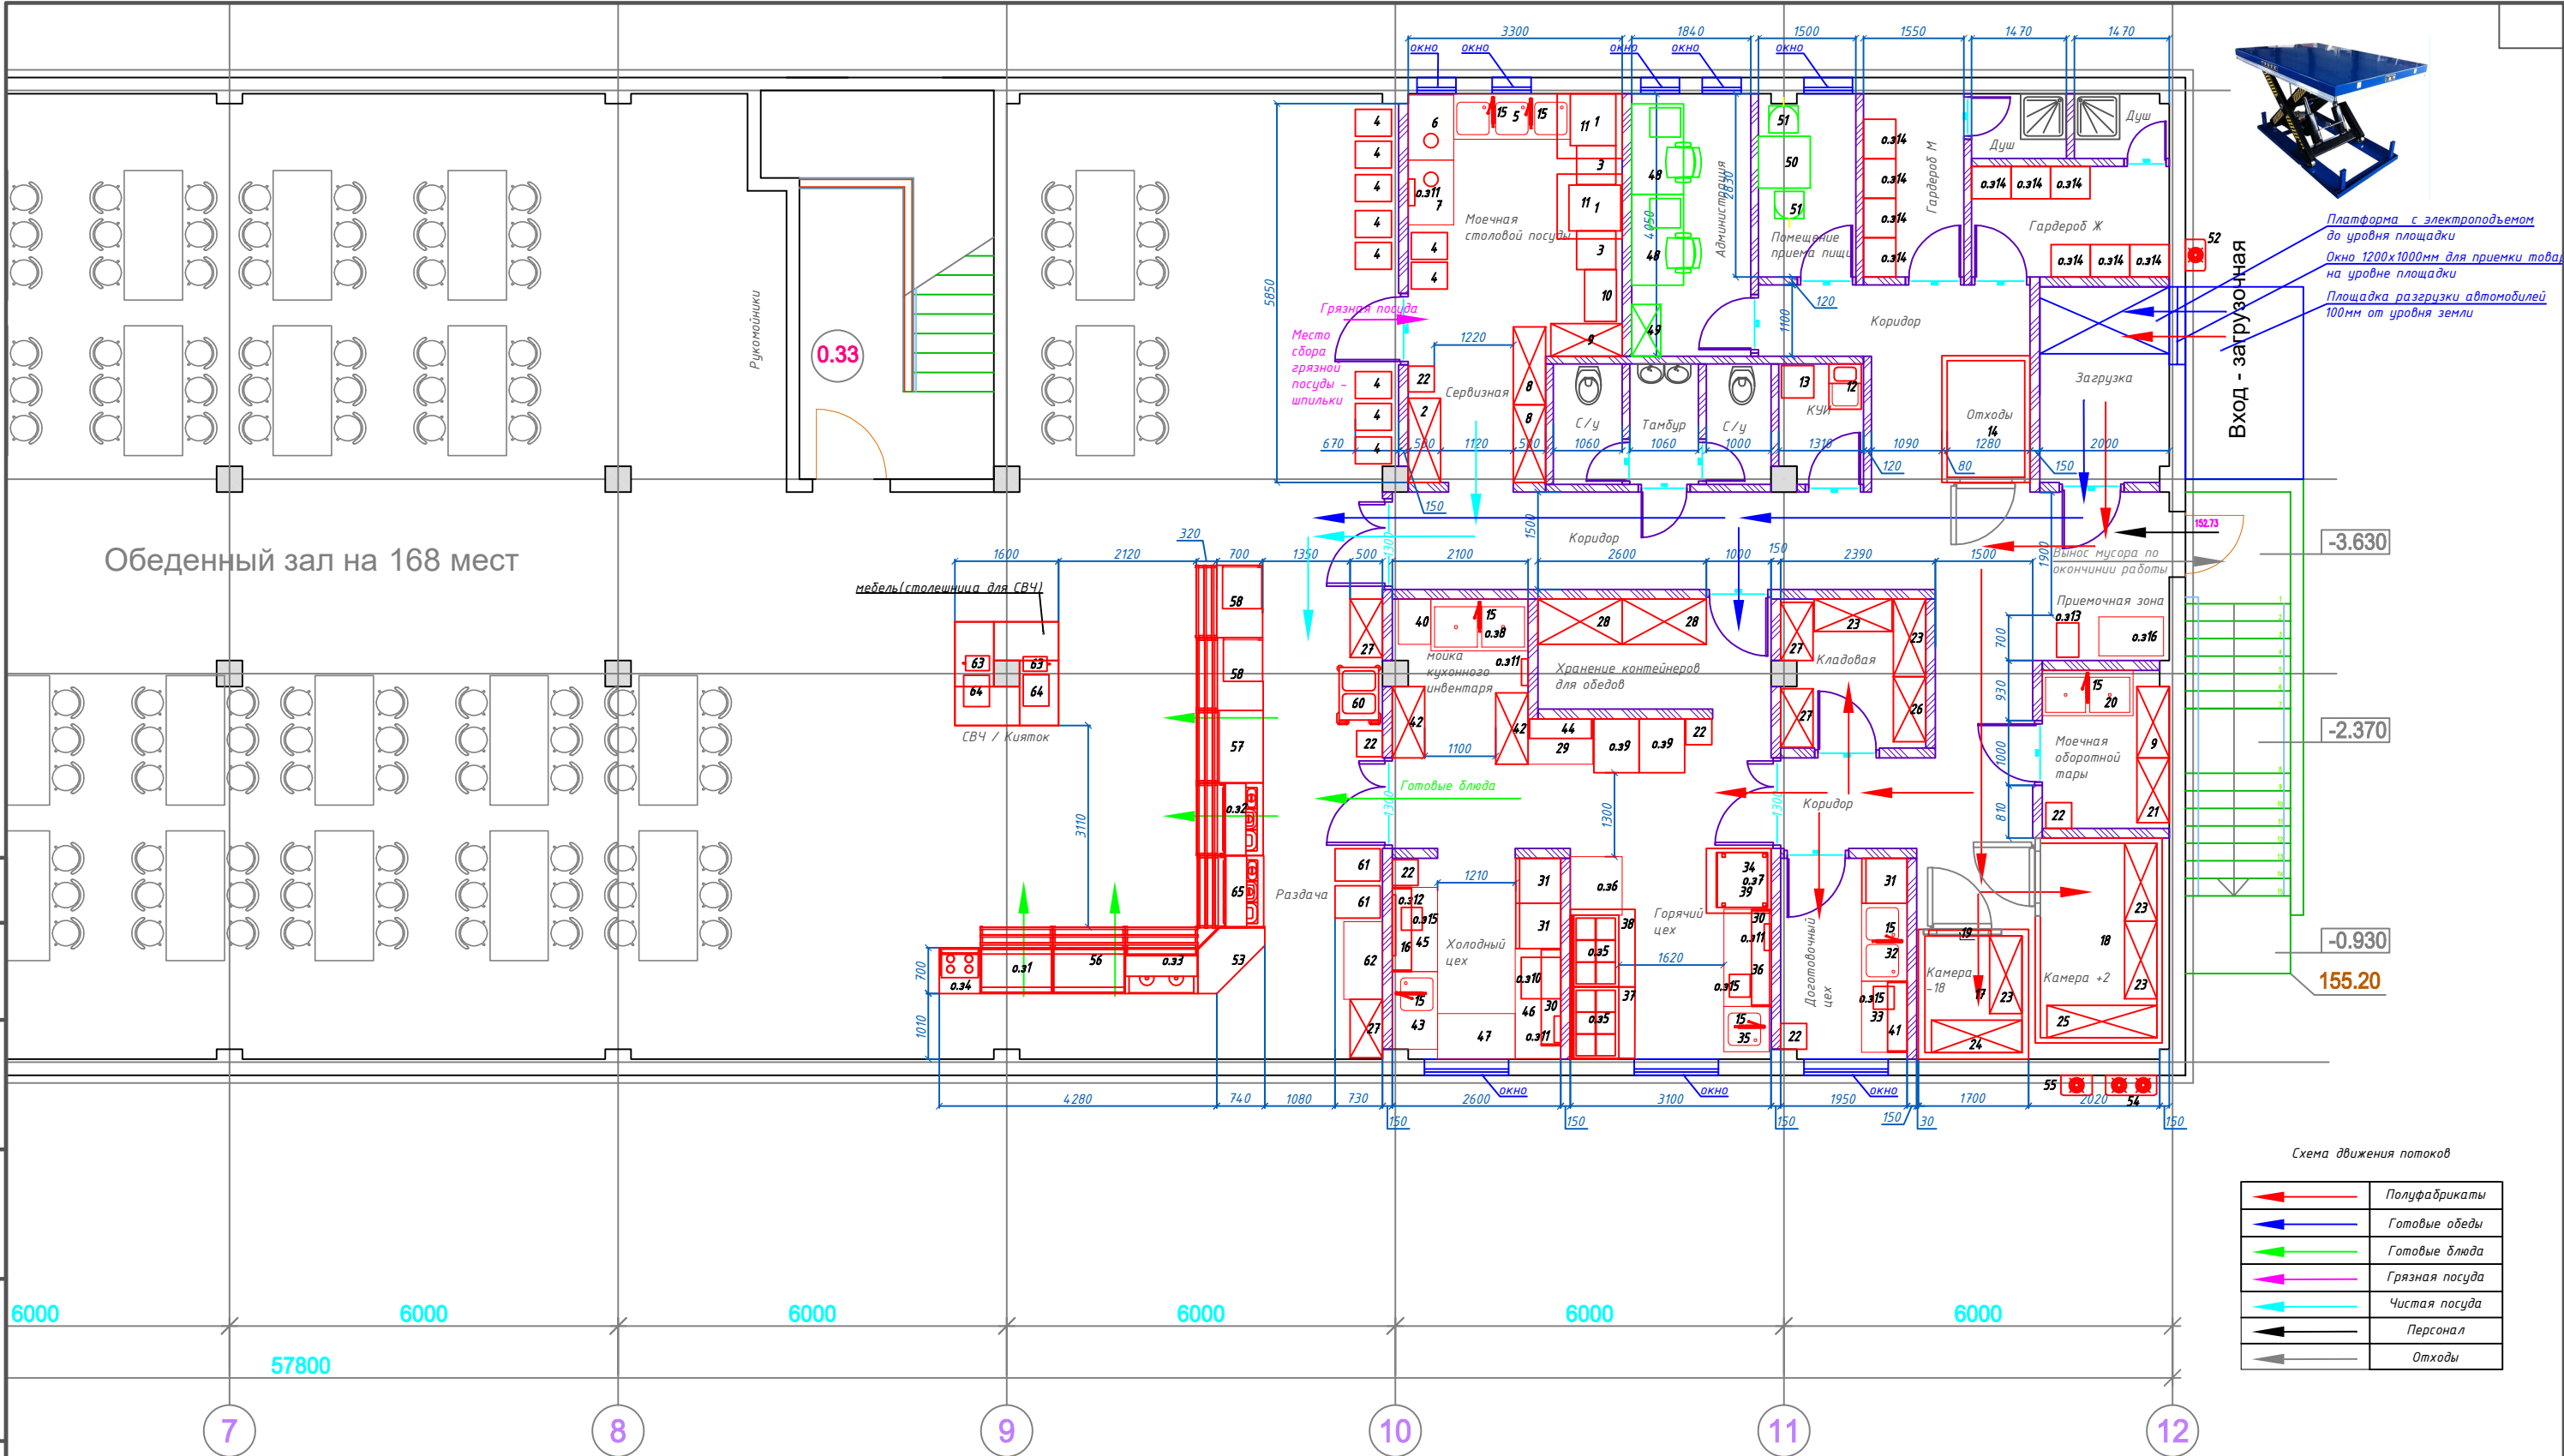

Масштаб 1:100


						951.ТХ		
						"Логопарк МЭЙДЖОР". Третья и четвертая очередь строительства" в границах земельного участка с кадастровым номером 50:08:0050340:157		
Изм.	Кол.уч.	Лист	док.	Подпись	Дата	Столовая при общежитии на 168 мест	Стадия	Лист
Разработал		Дудин			28.12.2020		П	5
Проверил		Савочкин			28.12.2020	План расстановки технологического оборудования План цокольного этажа		

Согласовано

Взам. инв. №

Подп. и дата

Инв. № подл.

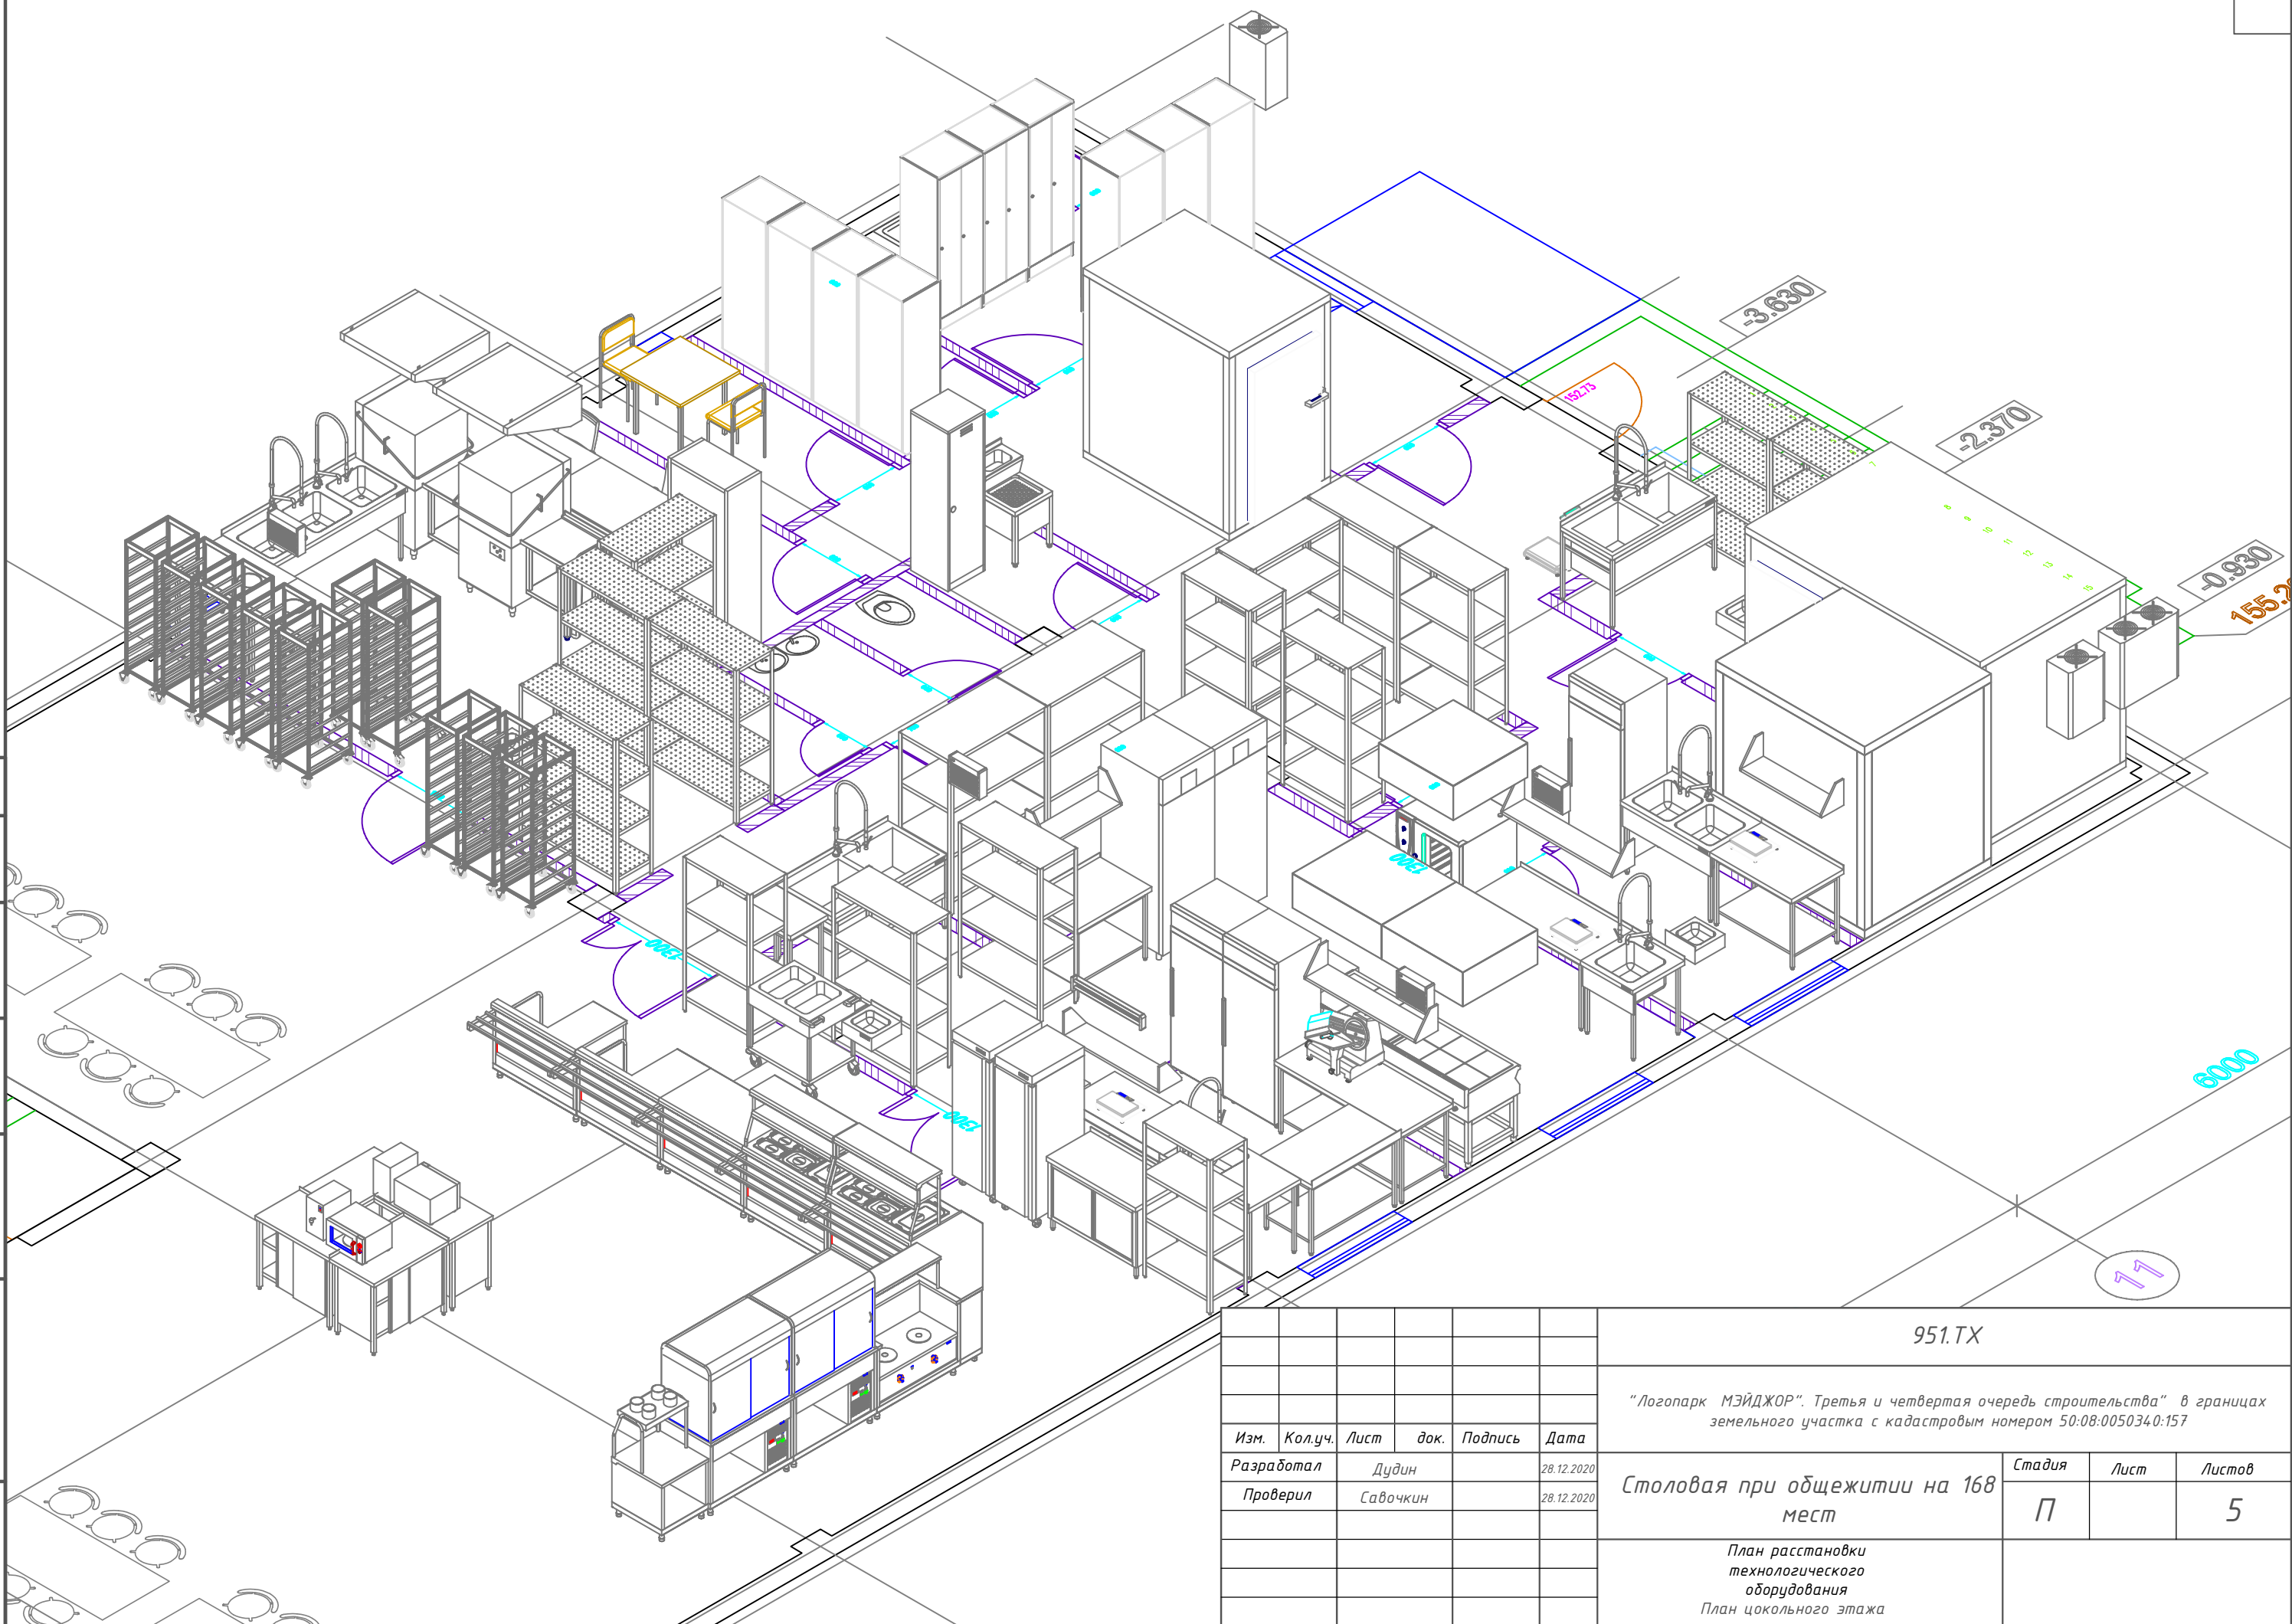


						951.TX		
						"Логопарк МЭЙДЖОР". Третья и четвертая очередь строительства" в границах земельного участка с кадастровым номером 50:08:0050340:157		
Изм.	Кол.уч.	Лист	док.	Подпись	Дата	Столовая при общежитии на 168 мест	Стадия	Лист
Разработал		Дудин			28.12.2020		П	5
Проверил		Савочкин			28.12.2020	План расстановки технологического оборудования План цокольного этажа		

Согласовано

Взам. инв. №

Подп. и дата

Инв. № подл.

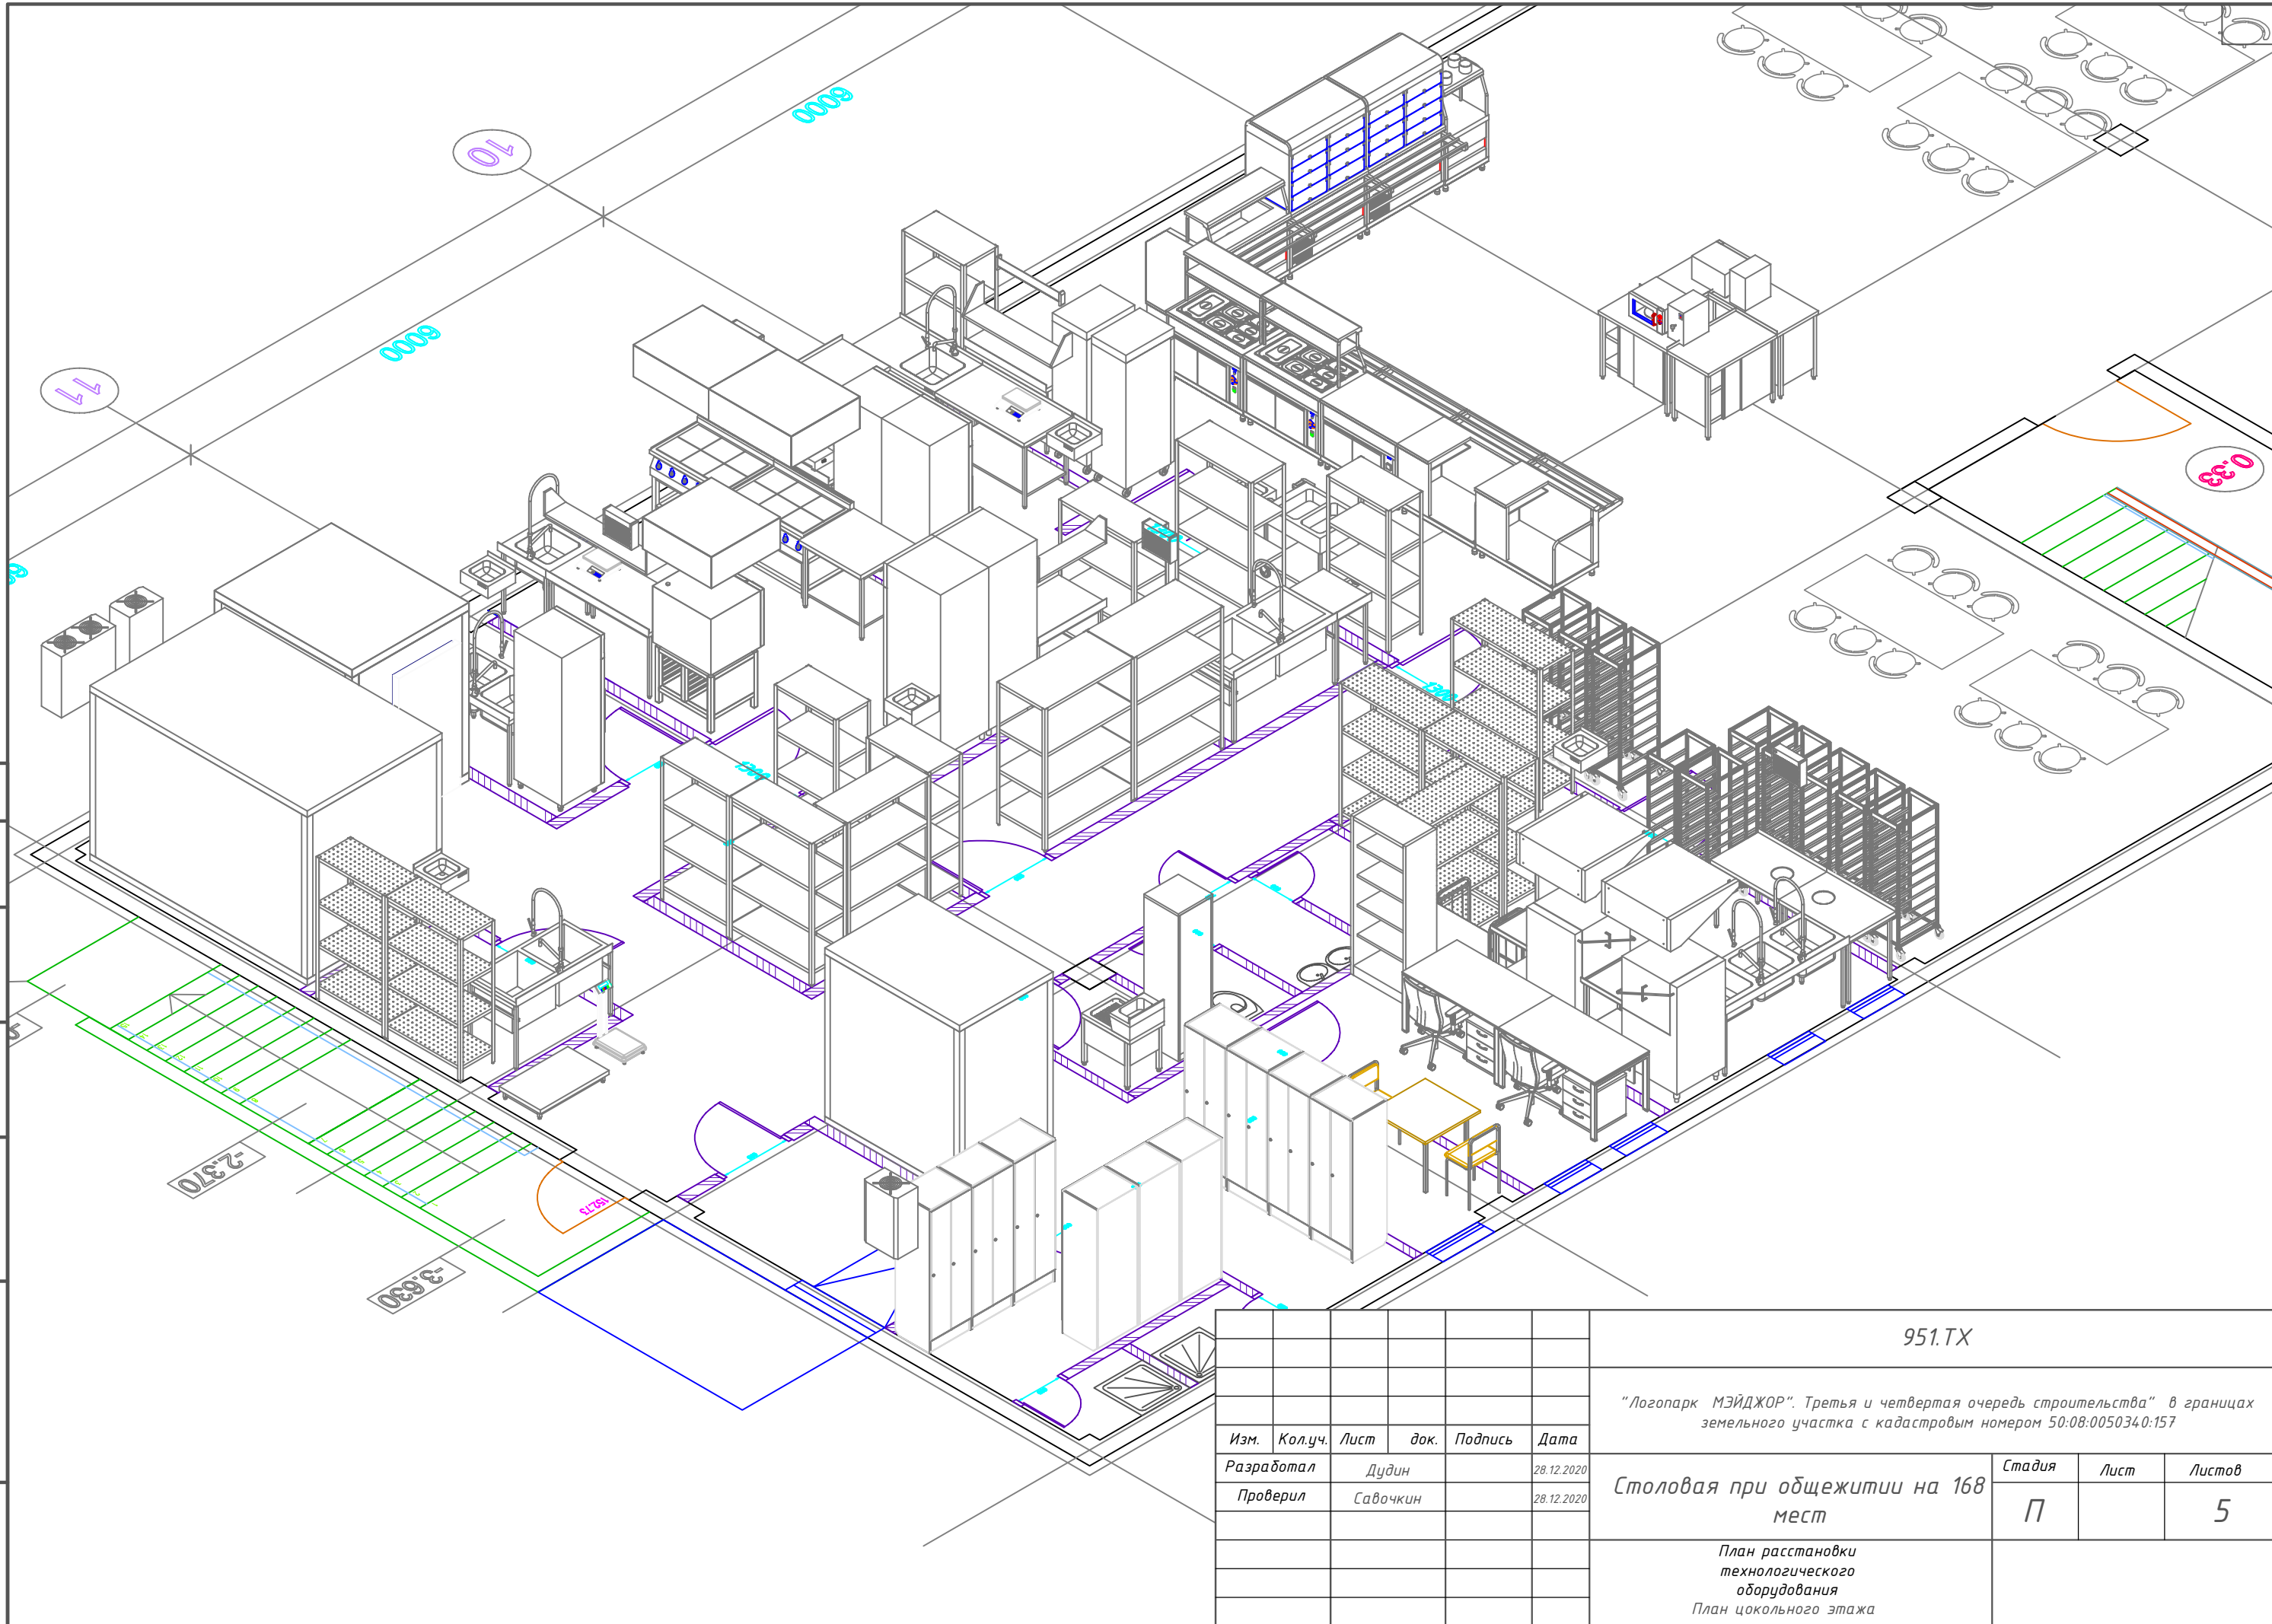


						951. TX		
						"Логопарк МЭЙДЖОР". Третья и четвертая очередь строительства" в границах земельного участка с кадастровым номером 50:08:0050340:157		
Изм.	Кол.уч.	Лист	док.	Подпись	Дата	Столовая при общежитии на 168 мест	Стадия	Лист
Разработал		Дудин			28.12.2020		П	5
Проверил		Савочкин			28.12.2020	План расстановки технологического оборудования План цокольного этажа		

Согласовано

Взам. инв. №

Подп. и дата

Инв. № подл.

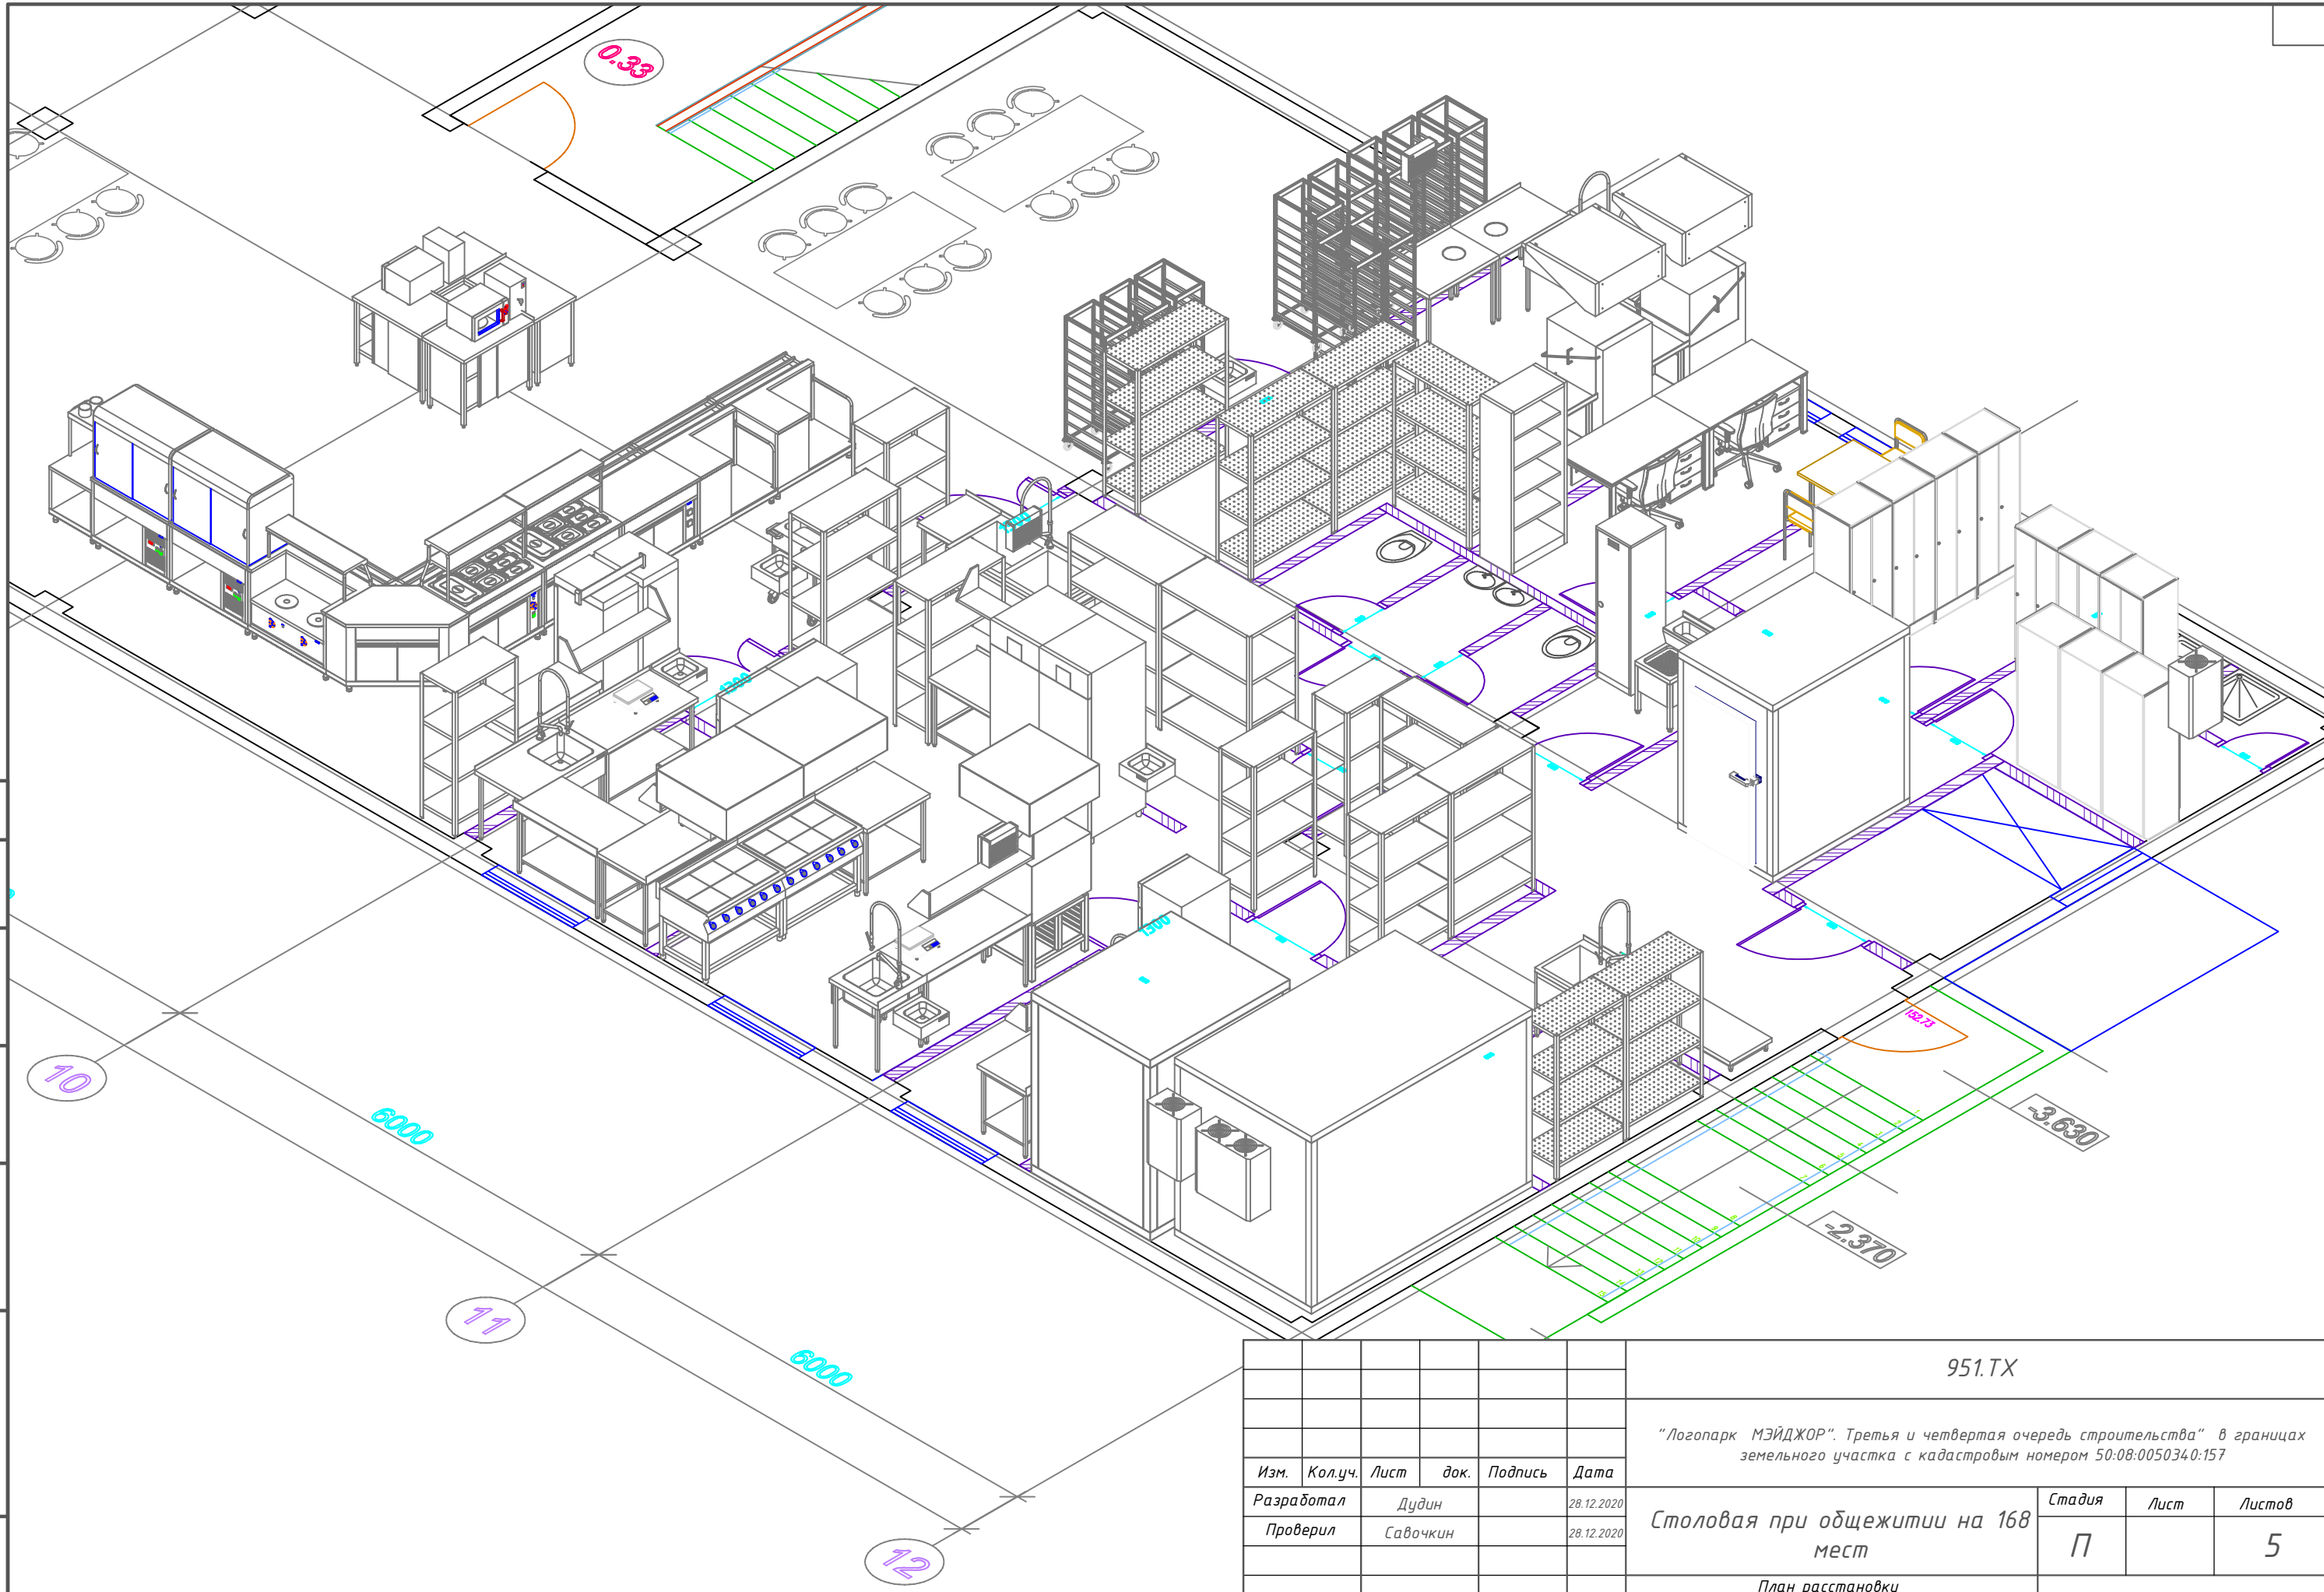

						951.TX		
						"Логопарк МЭЙДЖОР". Третья и четвертая очередь строительства" в границах земельного участка с кадастровым номером 50:08:0050340:157		
Изм.	Кол.уч.	Лист	док.	Подпись	Дата	Столовая при общежитии на 168 мест	Стадия	Лист
Разработал		Дудин			28.12.2020		П	5
Проверил		Савочкин			28.12.2020	План расстановки технологического оборудования План цокольного этажа		

